
ДИЗАЙН-ПРОЕКТ ИНТЕРЬЕРА
2-комнатной квартиры

Ведомость рабочих чертежей

Имя листа	№ листа
Титульный лист	01
Ведомость рабочих чертежей	02
Обмерочный чертеж	03
План демонтажа	04
План монтажа	05
Схема монтажа	06
План перепланировки	07
План расстановки мебели и оборудования	08
План формирования дверных проемов	09
План расстановки сантехнического оборудования	10
План потолков	11
План расстановки осветительного оборудования	12
План расположения розеток и выключателей	13
План управления осветительного оборудования	14
План раскладки напольных покрытий	15
Развертка кухонного гарнитура	16

		Подпись	Дата		Стадия	Лист
Руководитель:					ДП	02
Дизайнер:						
Выполнил:				Ведомость рабочих чертежей		
Заказчик:						

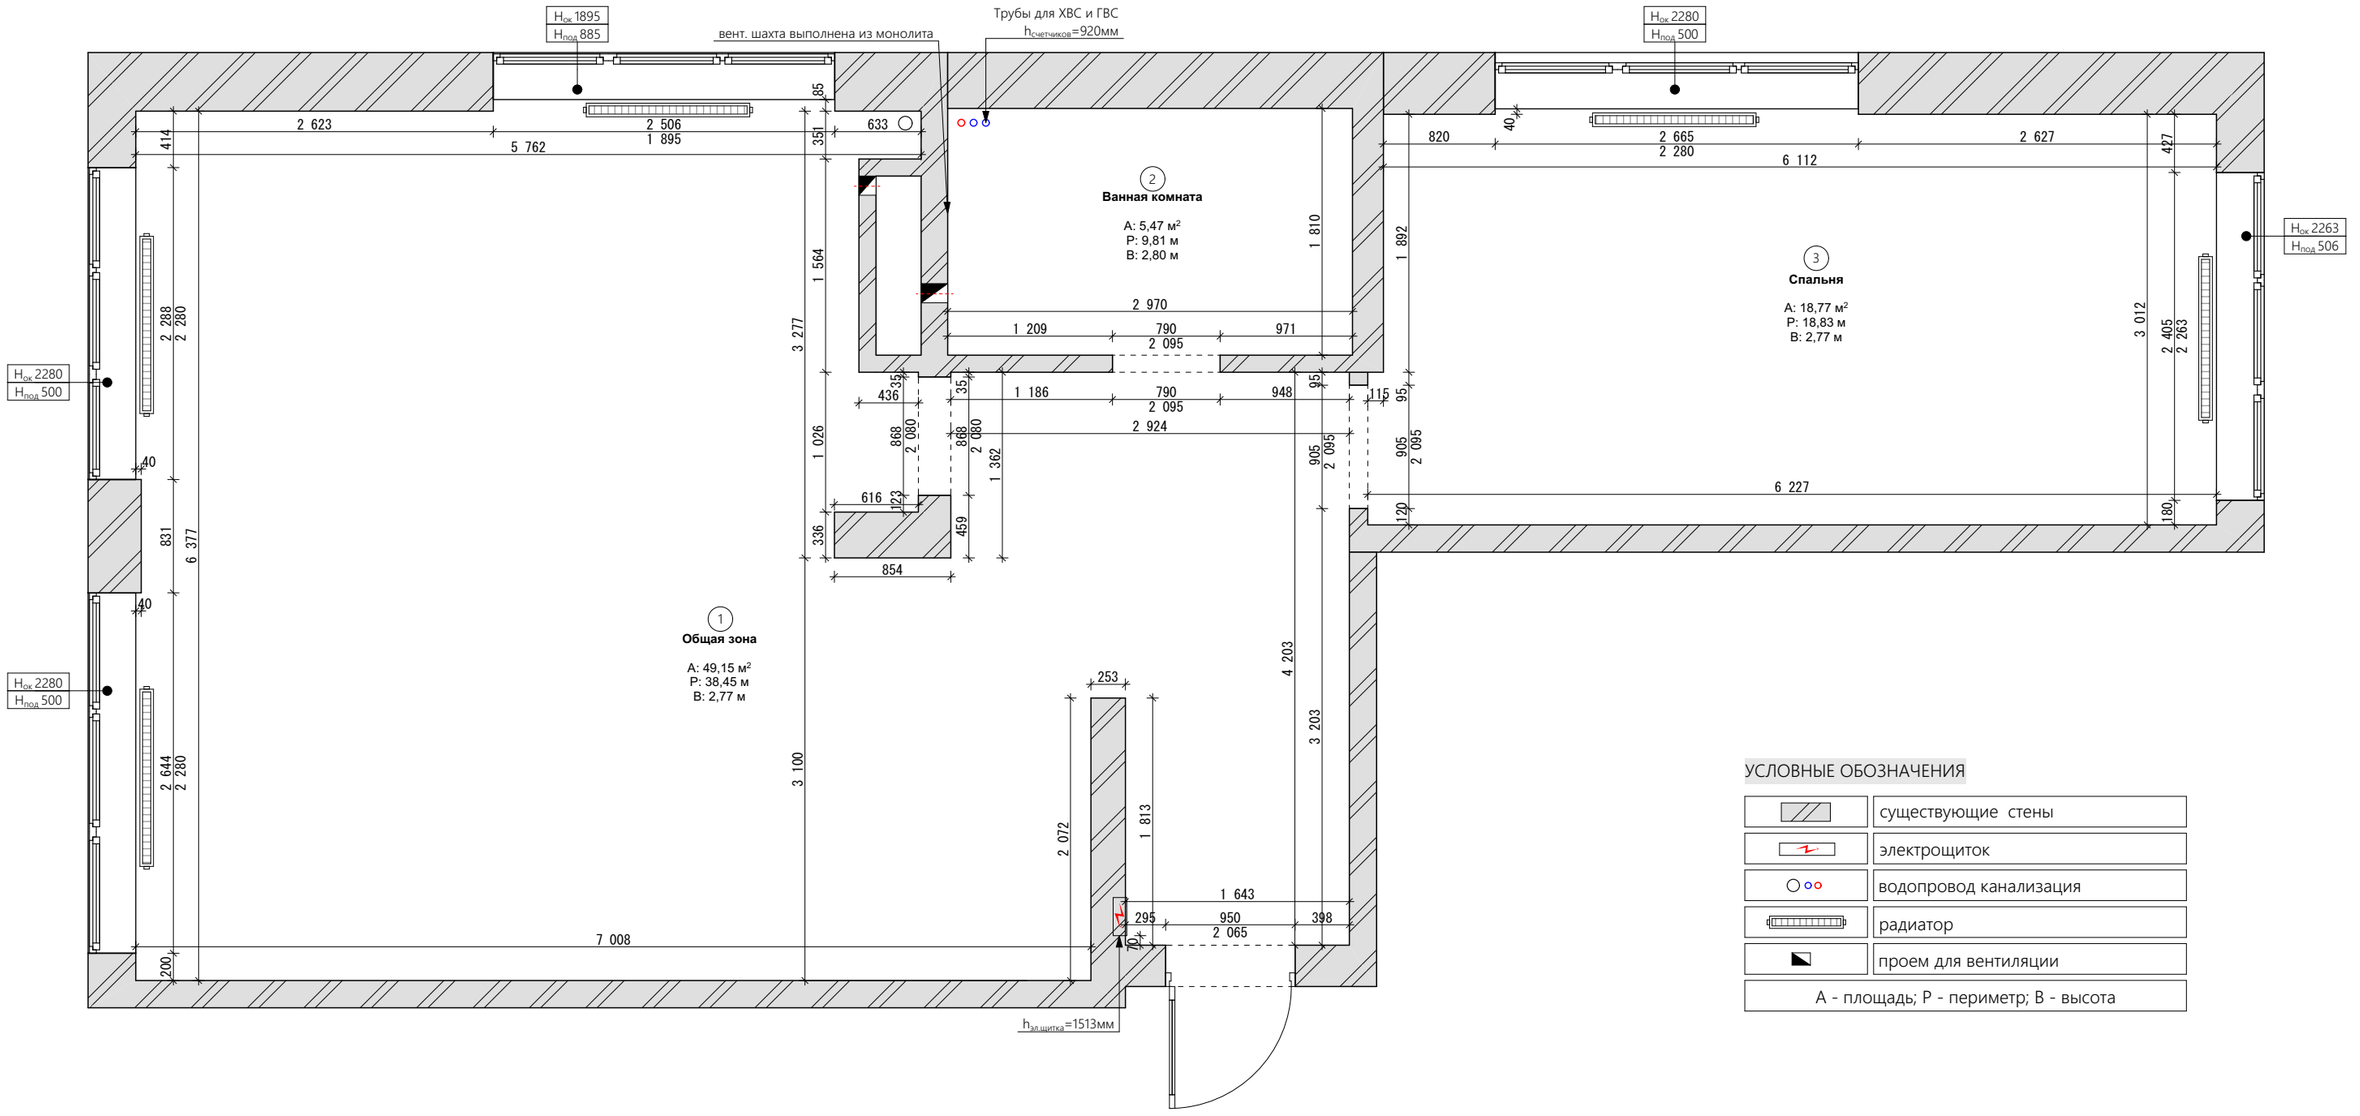

УСЛОВНЫЕ ОБОЗНАЧЕНИЯ

	существующие стены
	электрощиток
	водопровод канализация
	радиатор
	проем для вентиляции

A - площадь; P - периметр; B - высота


ЭКСПЛИКАЦИЯ ПОМЕЩЕНИЙ

№	Наименование помещения	Площадь, м²
1	Прихожая	49,15
2	Ванная комната	5,47
3	Спальня	18,77
Общая площадь = 73,39 м²		

ПРИМЕЧАНИЯ

1. Все размеры указаны в миллиметрах.
2. Все размеры проверить по месту, возможны погрешности.
3. Размеры даны без учета отделочных слоев.
4. В помещениях частичная штукатурка на стенах.

		Подпись	Дата		Стадия	Лист
Руководитель:					ДП	03
Дизайнер:						
Выполнил:				Обмерочный чертёж		
Заказчик:						

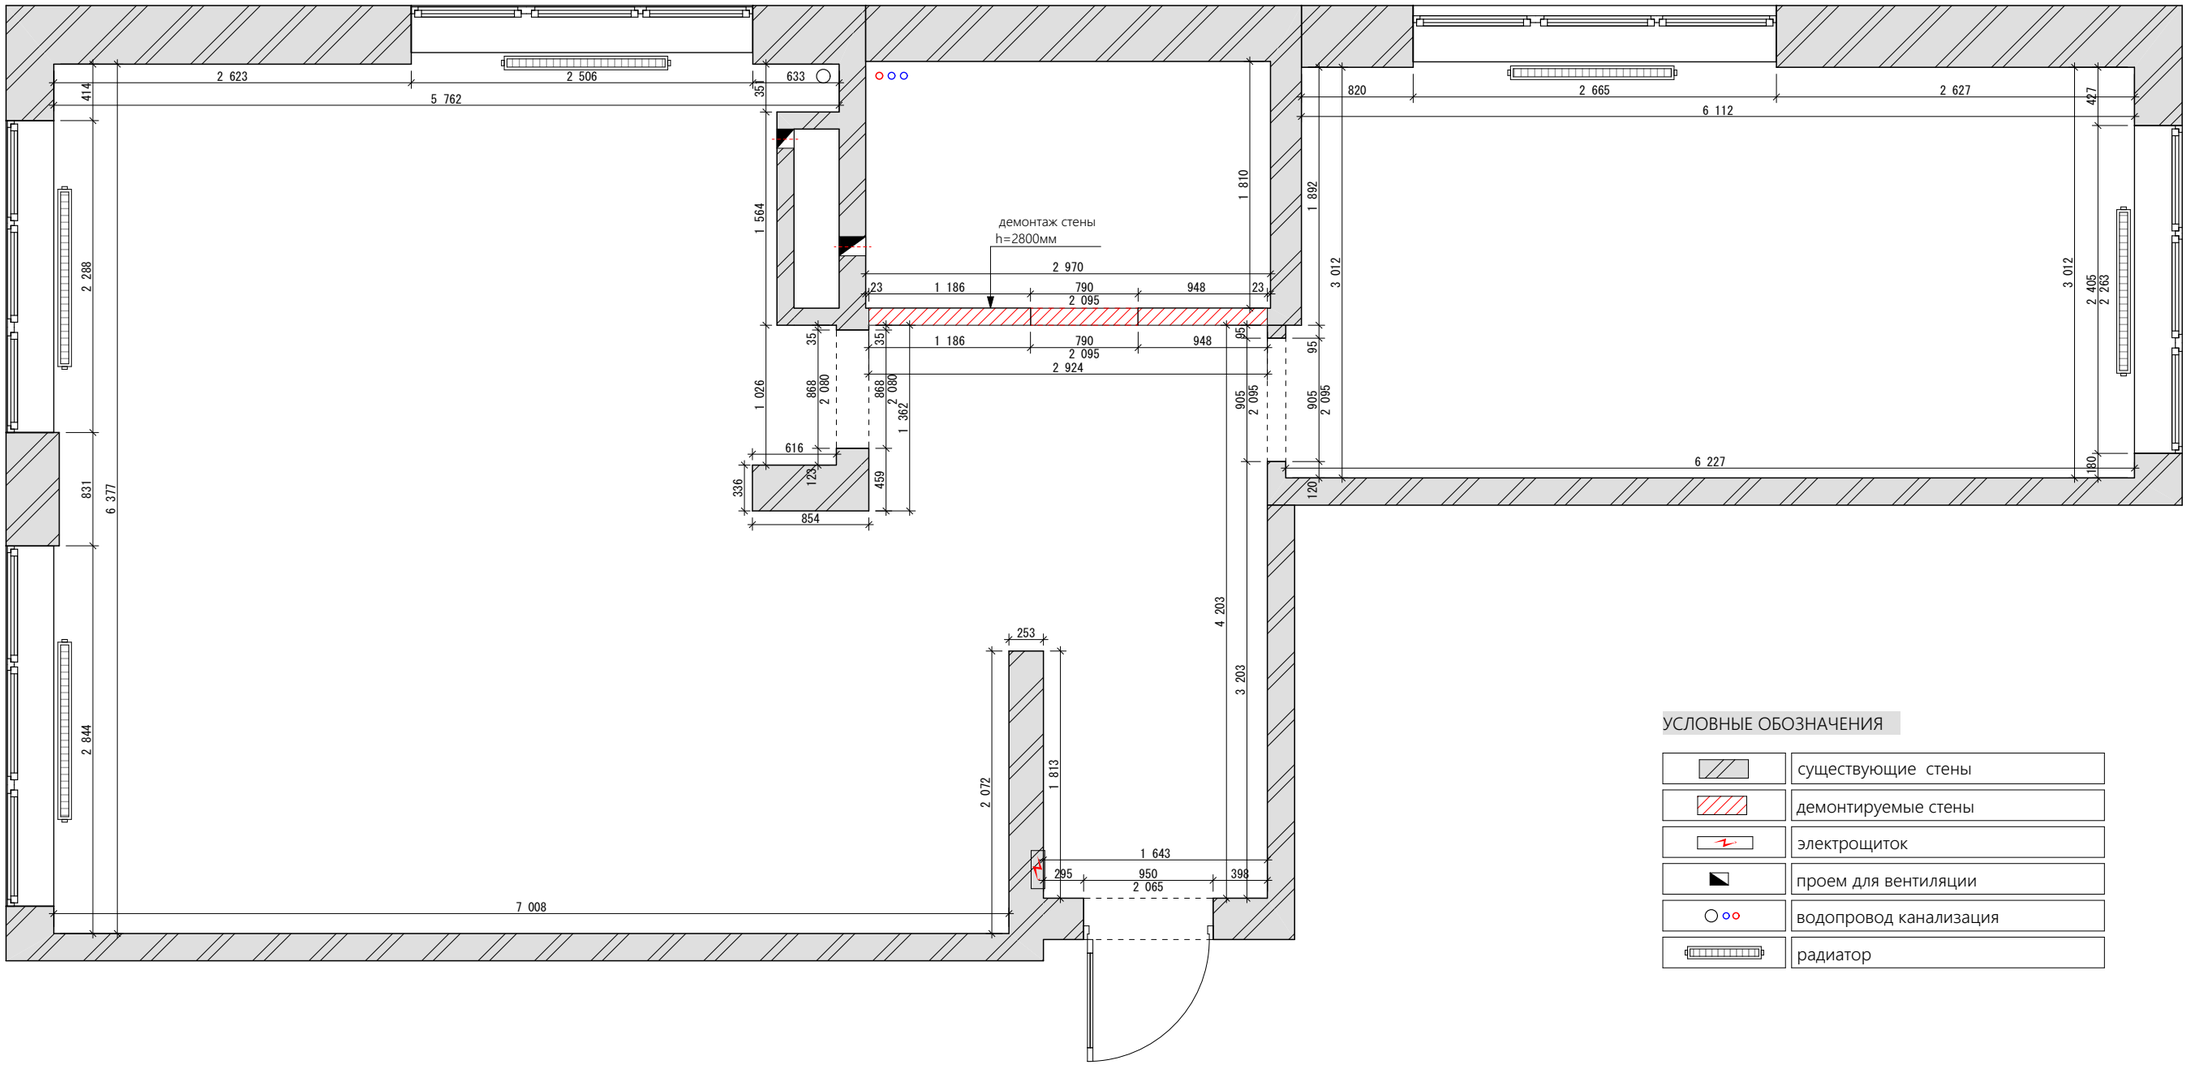


УСЛОВНЫЕ ОБОЗНАЧЕНИЯ

	существующие стены
	демонтируемые стены
	электрощиток
	проем для вентиляции
	водопровод канализация
	радиатор

ПРИМЕЧАНИЯ

1. Все размеры указаны в миллиметрах.
2. Размеры даны без учета отделочных слоев.
3. Все размеры проверить по месту, возможны погрешности.
4. Вносимые изменения в существующую планировку квартиры (демонтаж, монтаж, перенос радиаторов, канализации и т.п.) требуют согласования в государственных и муниципальных учреждениях либо самостоятельно, либо через специализированные организации и являются ответственностью Заказчика.

		Подпись	Дата		Стадия	Лист
Руководитель:					ДП	04
Дизайнер:						
Выполнил:				План демонтажа		
Заказчик:						

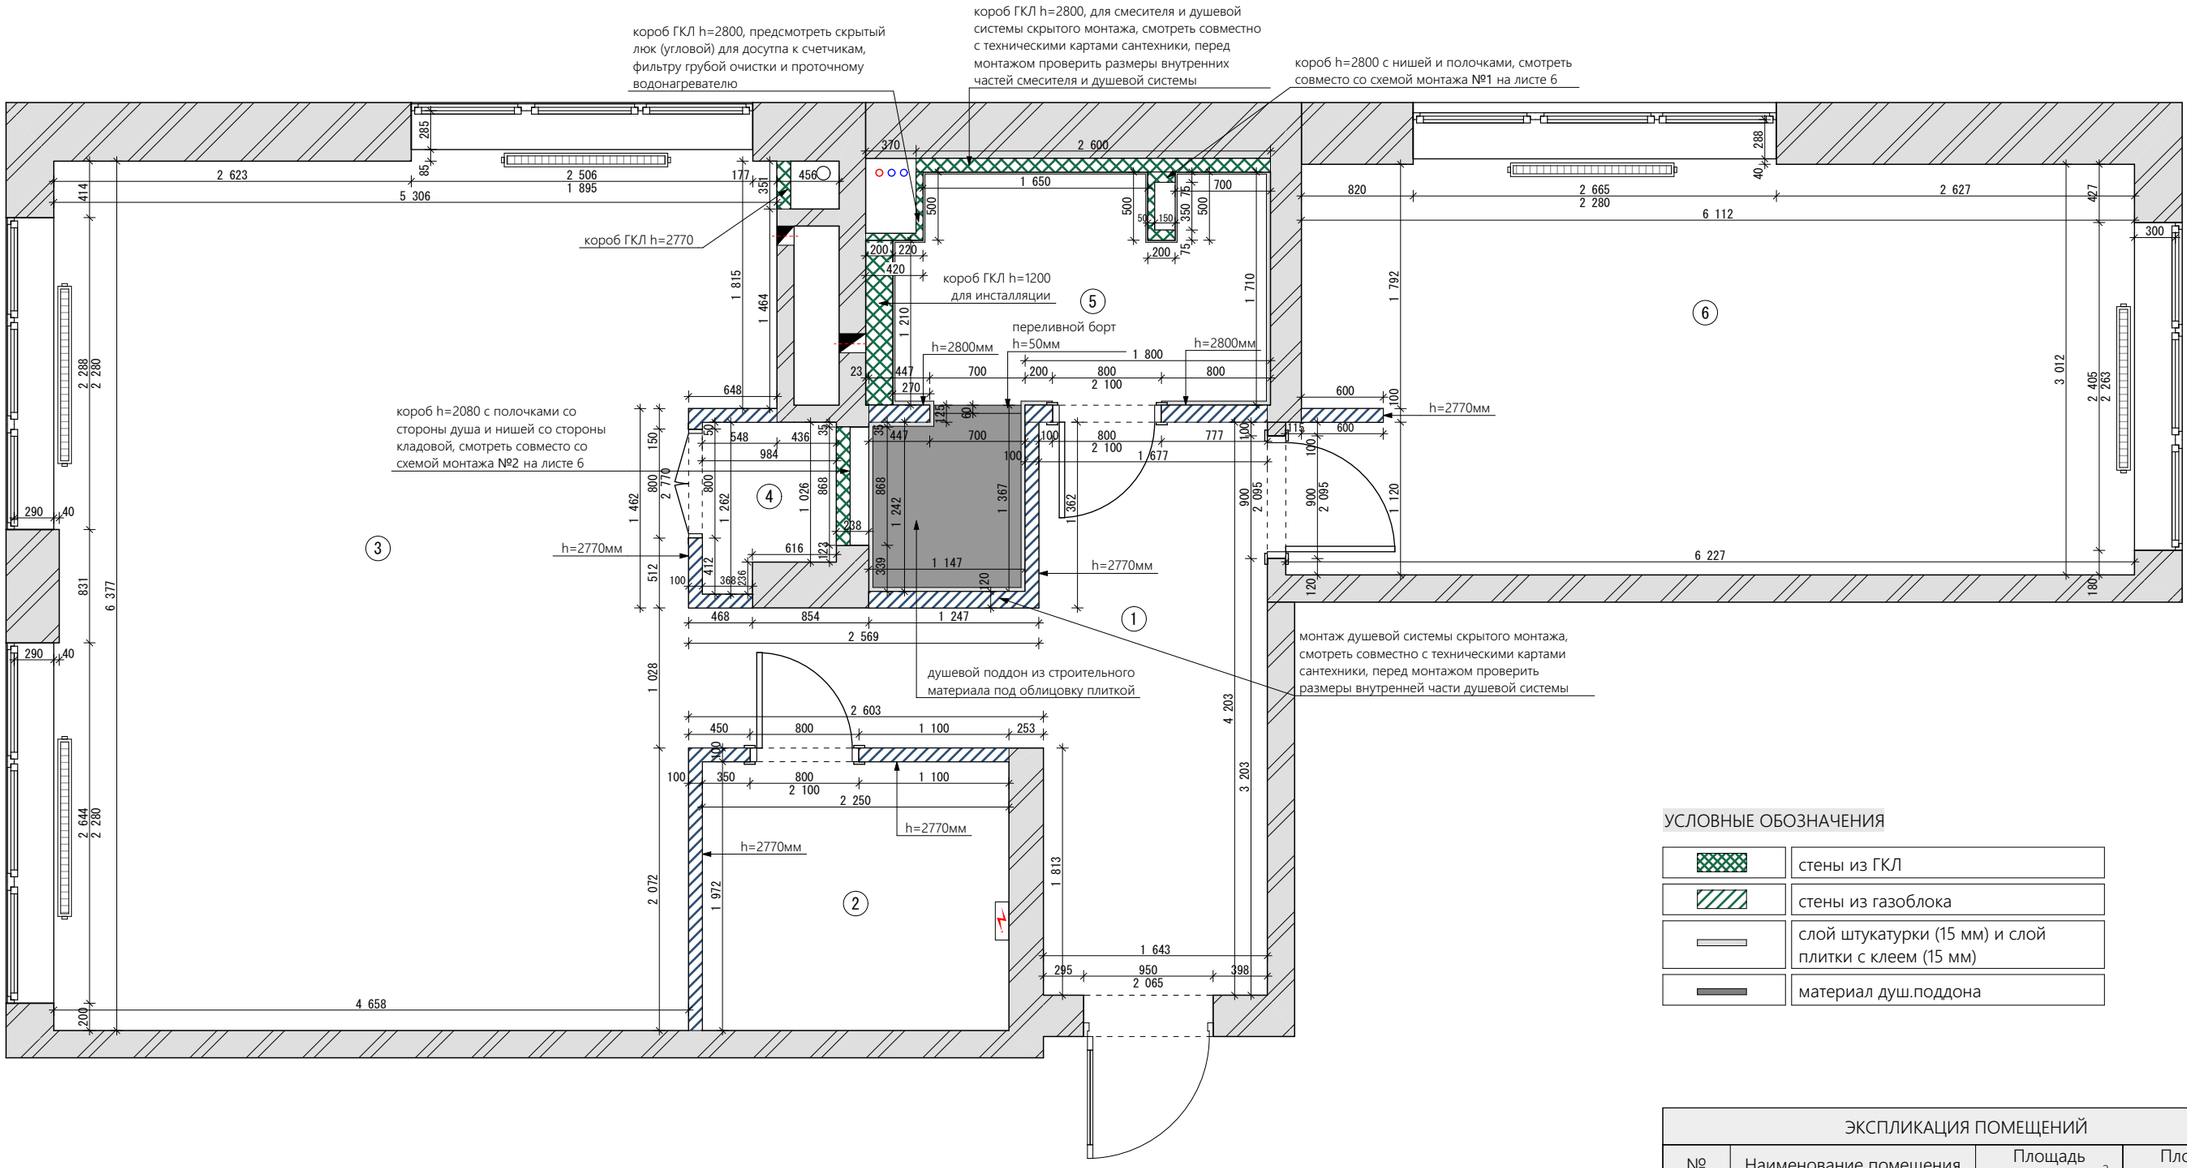

УСЛОВНЫЕ ОБОЗНАЧЕНИЯ

	стены из ГКЛ
	стены из газоблока
	слой штукатурки (15 мм) и слой плитки с клеем (15 мм)
	материал душ.поддона

ЭКСПЛИКАЦИЯ ПОМЕЩЕНИЙ			
№	Наименование помещения	Площадь помещения, м²	Площадь помещения, м²
1	Прихожая	10,02	36,75
2	Гардеробная	4,44	21,71
3	Кухня-гостиная	31,06	47,21
4	Кладовая	1,10	10,76
5	Ванная комната	6,59	36,93
6	Спальня	18,58	43,28
		Sобщ = 71,79 м²	$S_{общ}$ = 205,11 м²


ПРИМЕЧАНИЯ

1. Все размеры указаны в миллиметрах.
2. Размеры даны без учета отделочных слоев.
3. В конструкциях, скрывающих коммуникации предусмотреть лючки.
4. Вносимые изменения в существующую планировку квартиры (демонтаж, монтаж, перенос радиаторов, канализации и т.п.) требуют согласования в государственных и муниципальныз учреждениях либо самостоятельно, либо через специализированные организации и являются ответственностью Заказчика.
5. Высоту и ширину межкомнатных проемов уточнить после окончательного согласования моделей дверей.
6. Площадь возводимых конструкций на чертеже и фактическая площадь могут отличаться по техническим моментам.
7. Краны перекрытия воды предусмотреть по месту с согласованием прораба и заказчика.
8. Вывести углы стен под 90 градусов в санузлах, в местах монтажа плитки на стенах (фартук, декоративные панели) а также на местах монтажа корпусной мебели, панельной отделки, декоративных ГКЛ конструкций.

		Подпись	Дата		Стадия	Лист
Руководитель:					ДП	05
Дизайнер:						
Выполнил:				План монтажа		
Заказчик:						

СХЕМА МОНТАЖА №1
НИША С ПОЛОЧКАМИ У ВАННОЙ

Вид аксонометрии

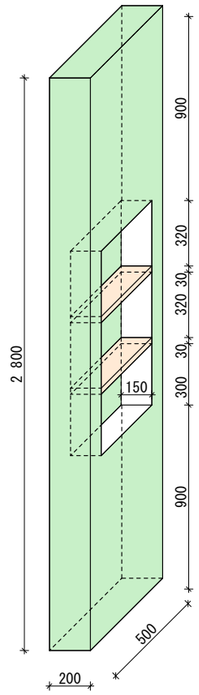

Вид спереди



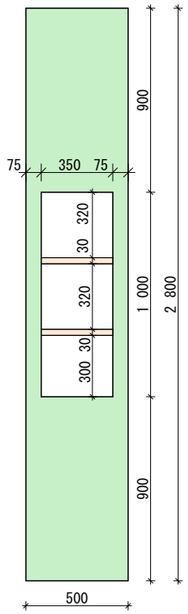


СХЕМА МОНТАЖА №2
КОРОБ С ПОЛОЧКОЙ СО СТОРОНЫ ДУША И С НИШЕЙ СО СТОРОНЫ КЛАДОВОЙ


Ниша возводимая из ГКЛ

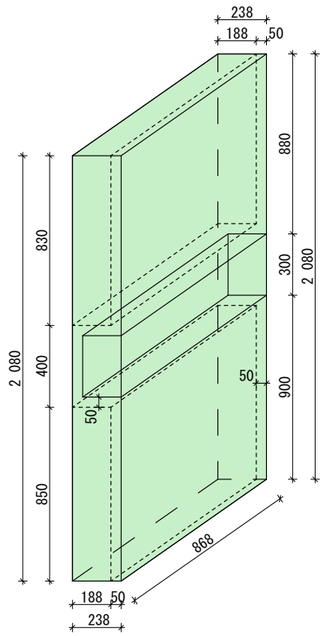


Вид ниши со стороны кладовой

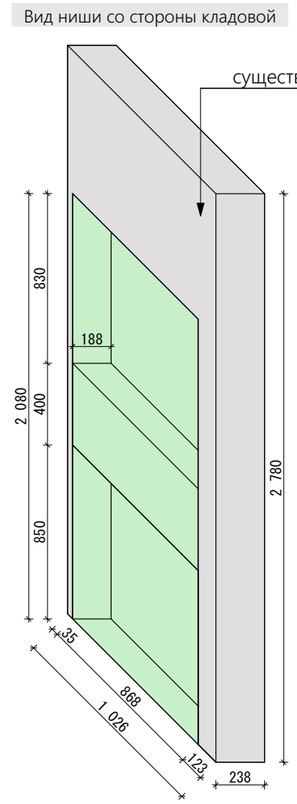

Вид ниши со стороны душа

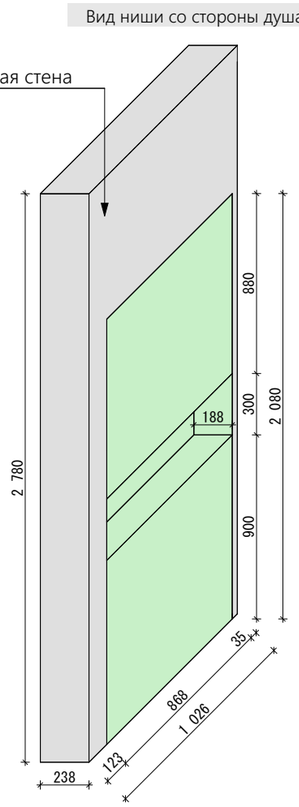

		Подпись	Дата		Стадия	Лист
Руководитель:					ДП	06
Дизайнер:						
Выполнил:				Схемы монтажа		
Заказчик:						

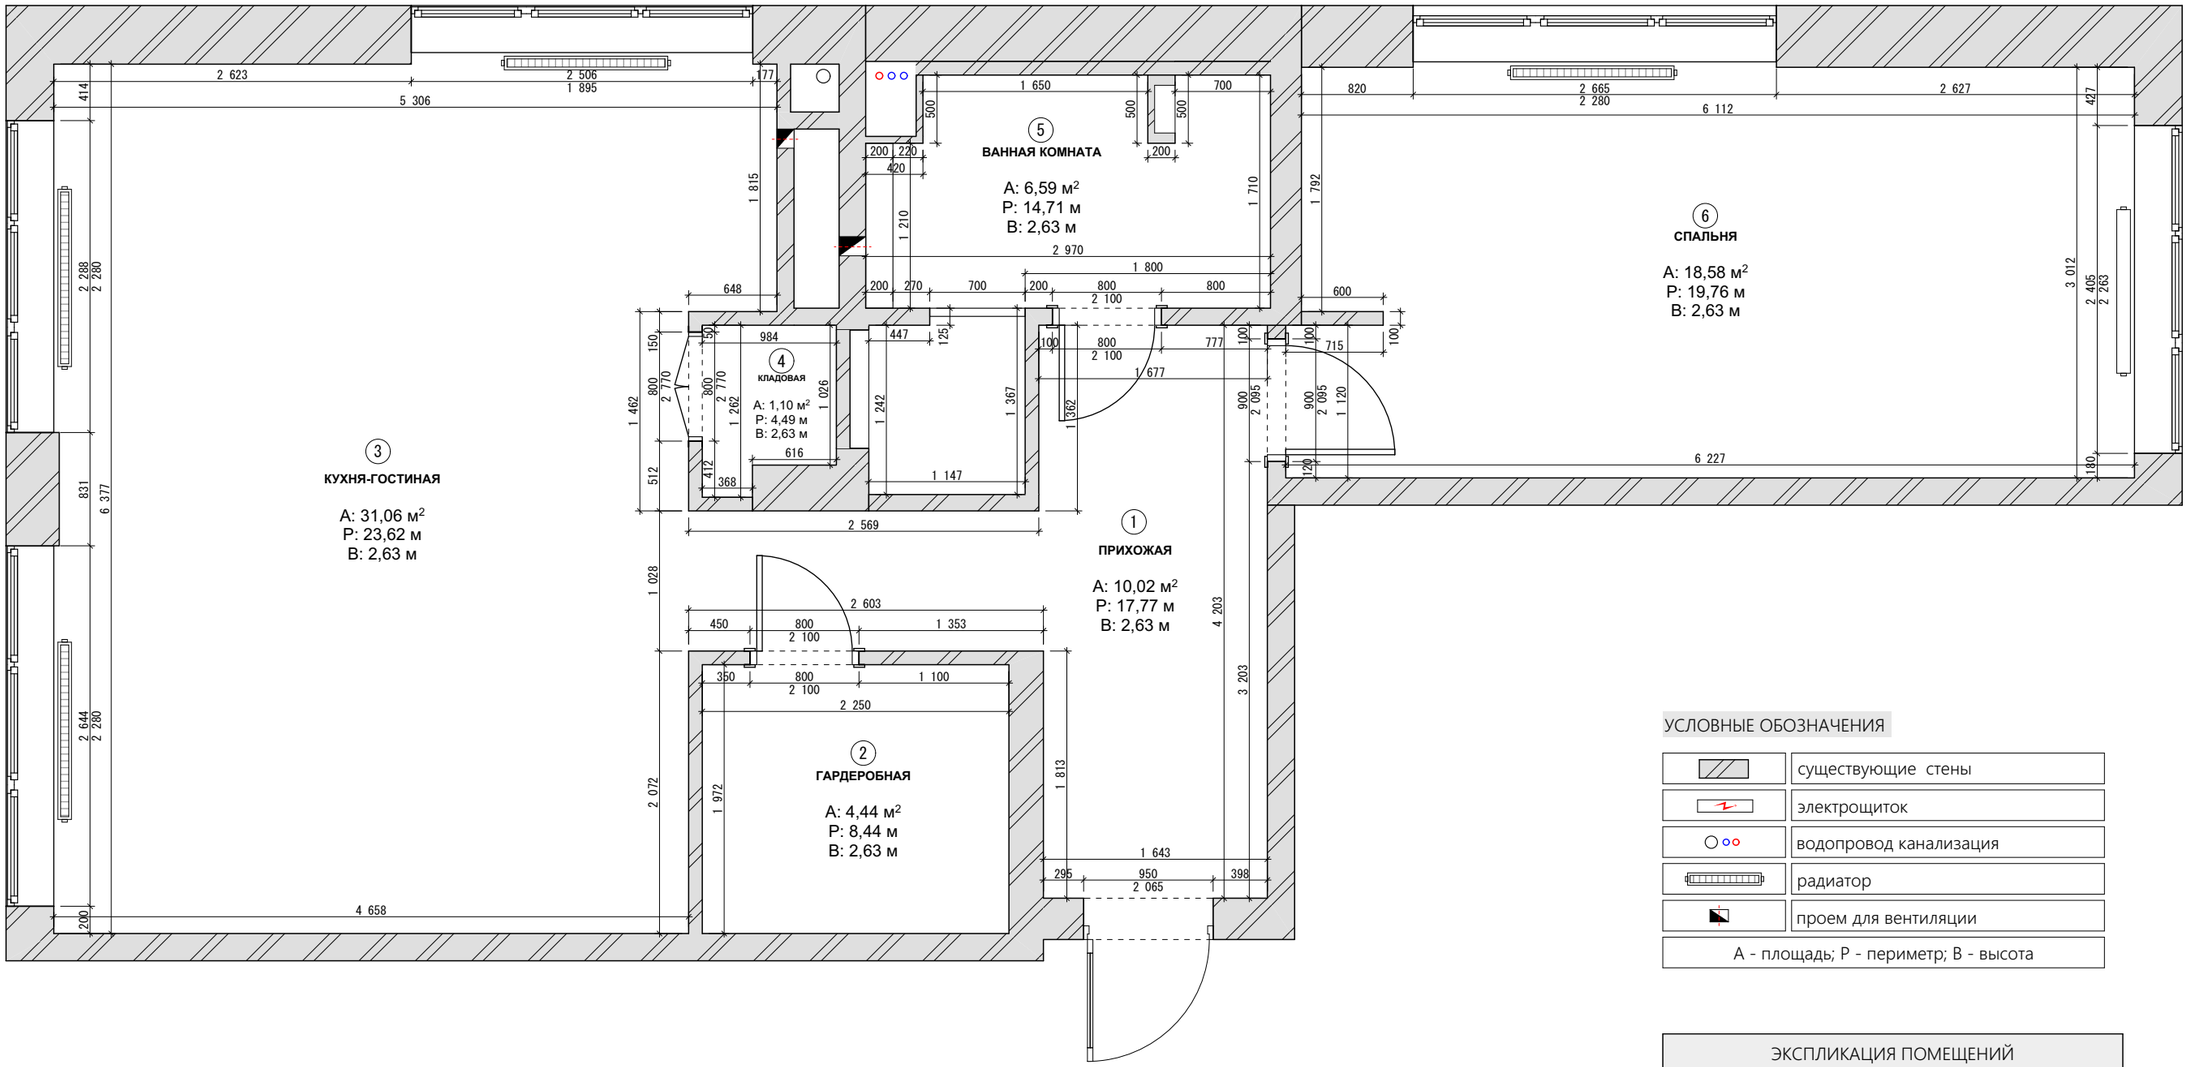

УСЛОВНЫЕ ОБОЗНАЧЕНИЯ

	существующие стены
	электрощиток
	водопровод канализация
	радиатор
	проем для вентиляции

А - площадь; Р - периметр; В - высота


ЭКСПЛИКАЦИЯ ПОМЕЩЕНИЙ

№	Наименование помещения	Площадь, м²
1	Прихожая	10,02
2	Гардеробная	4,44
3	Кухня-гостиная	31,06
4	Кладовая	1,10
5	Ванная комната	6,59
6	Спальня	18,58
Общая площадь = 71,79 м²		

ПРИМЕЧАНИЯ

1. Все размеры указаны в миллиметрах.
2. Размеры даны без учета отделочных слоев.

		Подпись	Дата		Стадия	Лист
Руководитель:					ДП	07
Дизайнер:						
Выполнил:				План перепланировки		
Заказчик:						

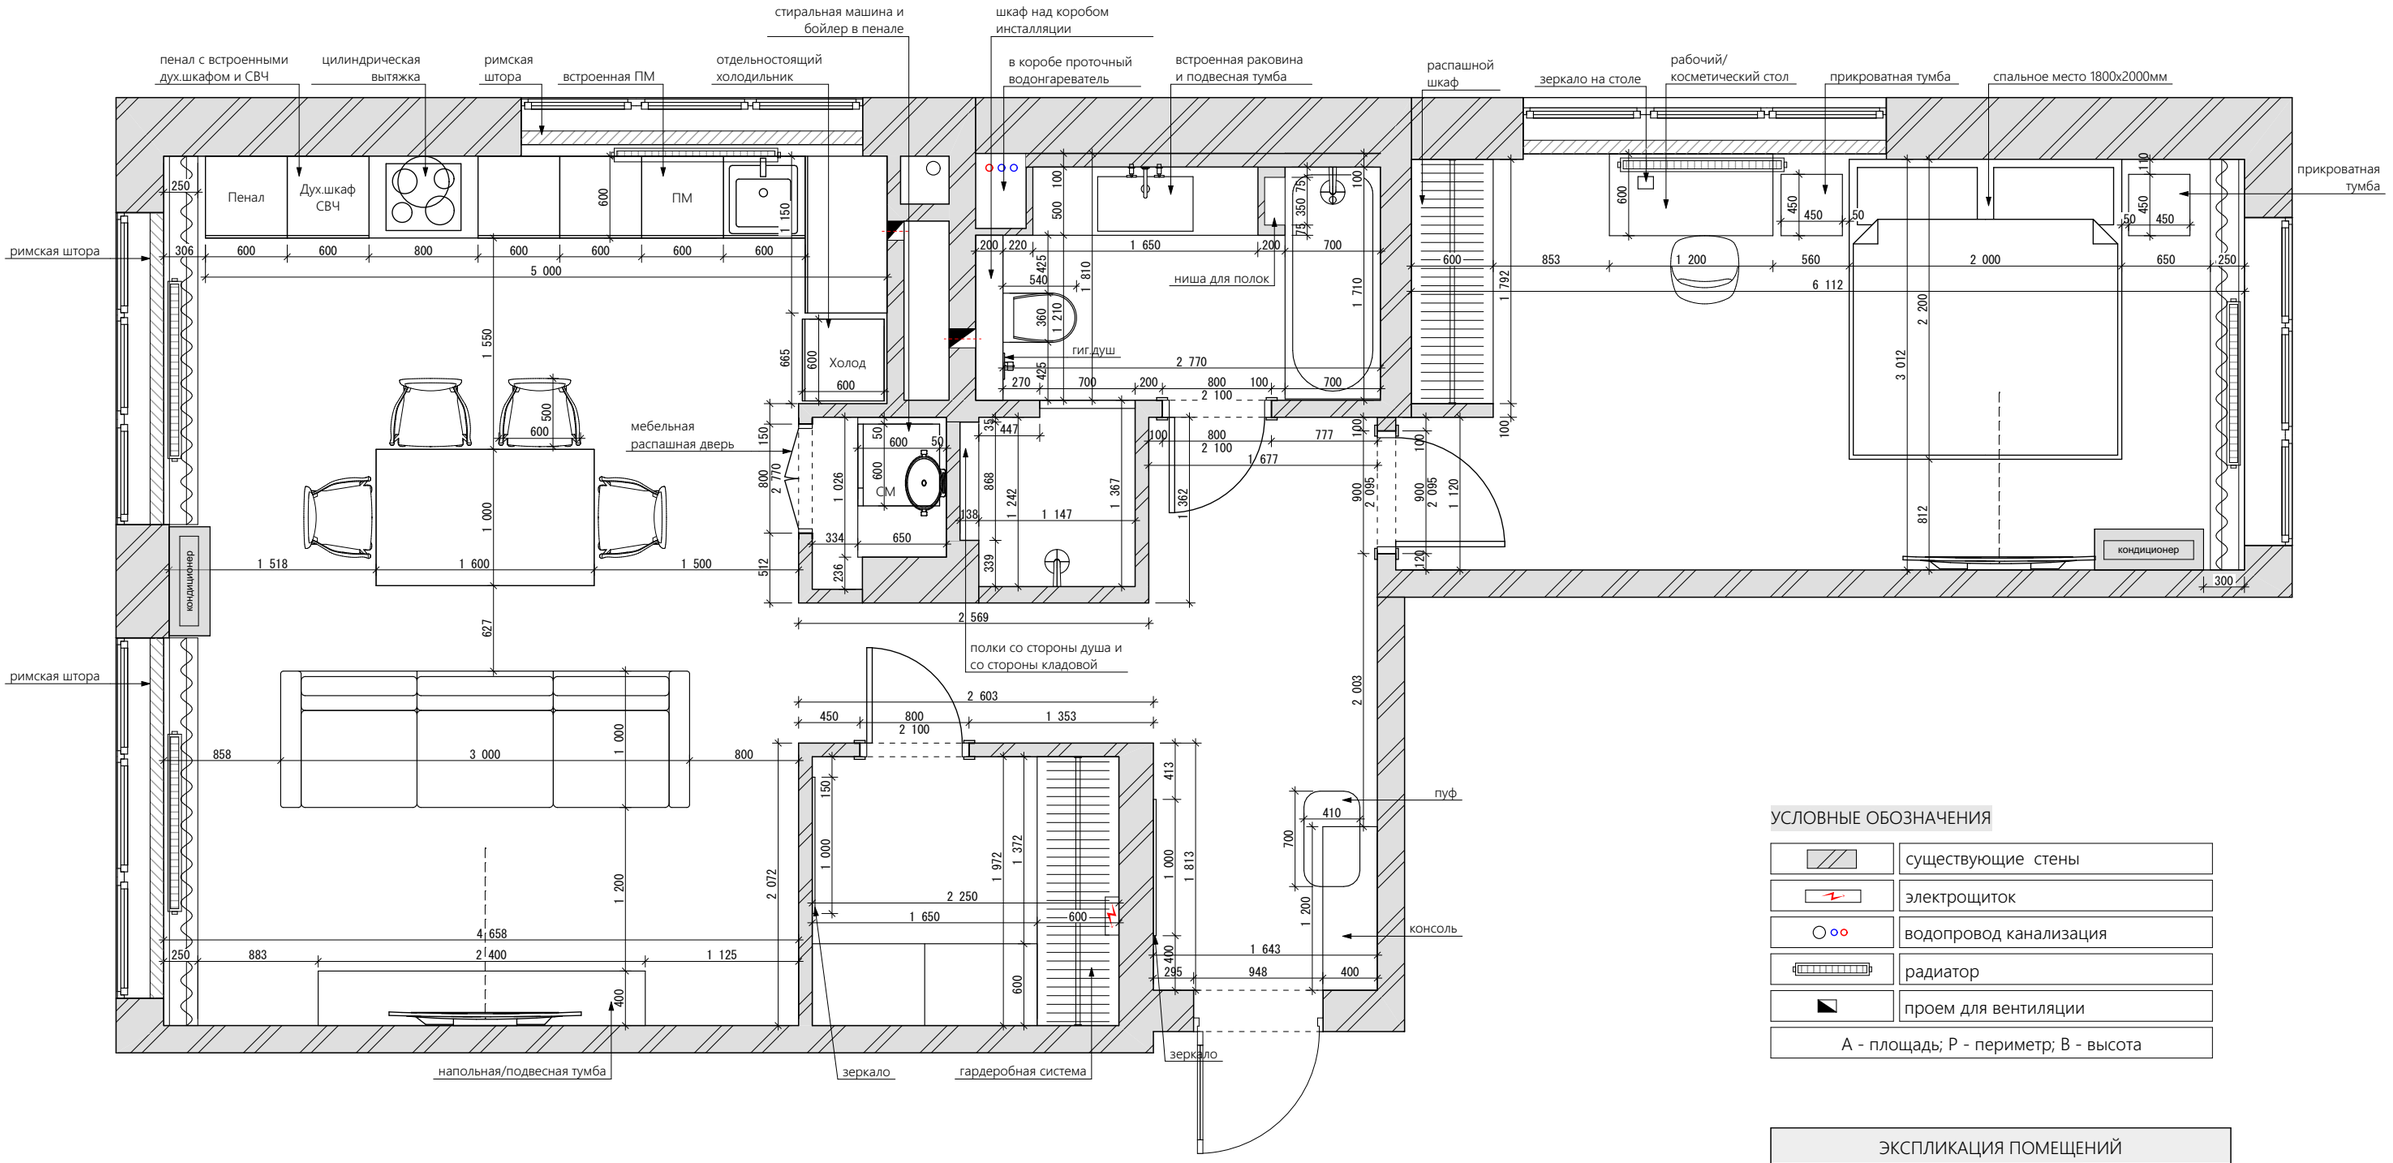

УСЛОВНЫЕ ОБОЗНАЧЕНИЯ


	существующие стены
	электрощиток
	водопровод канализация
	радиатор
	проем для вентиляции
А - площадь; Р - периметр; В - высота	

ЭКСПЛИКАЦИЯ ПОМЕЩЕНИЙ		
№	Наименование помещения	Площадь, м²
1	Прихожая	10,02
2	Гардеробная	4,44
3	Кухня-гостиная	31,06
4	Кладовая	1,10
5	Ванная комната	6,59
6	Спальня	18,58
Общая площадь = 71,79 м²		

ПРИМЕЧАНИЯ

1. Все размеры указаны в миллиметрах.
2. Размеры даны без учета отделочных слоев.
3. Сокращения на чертежах:
СМ - стиральная машина;
ПМ - посудомоечная машина.
4. Мебель индивидуального изготовления заказывать только после фактических обмеров по месту от производителя.
5. Закупка сантехнического оборудования осуществляется только после возведения перегородок, оштукатуривания стен, укладки плитки и последующей проверки размеров.

		Подпись	Дата		Стадия	Лист
Руководитель:					ДП	08
Дизайнер:						
Выполнил:				План расстановки мебели и оборудования		
Заказчик:						

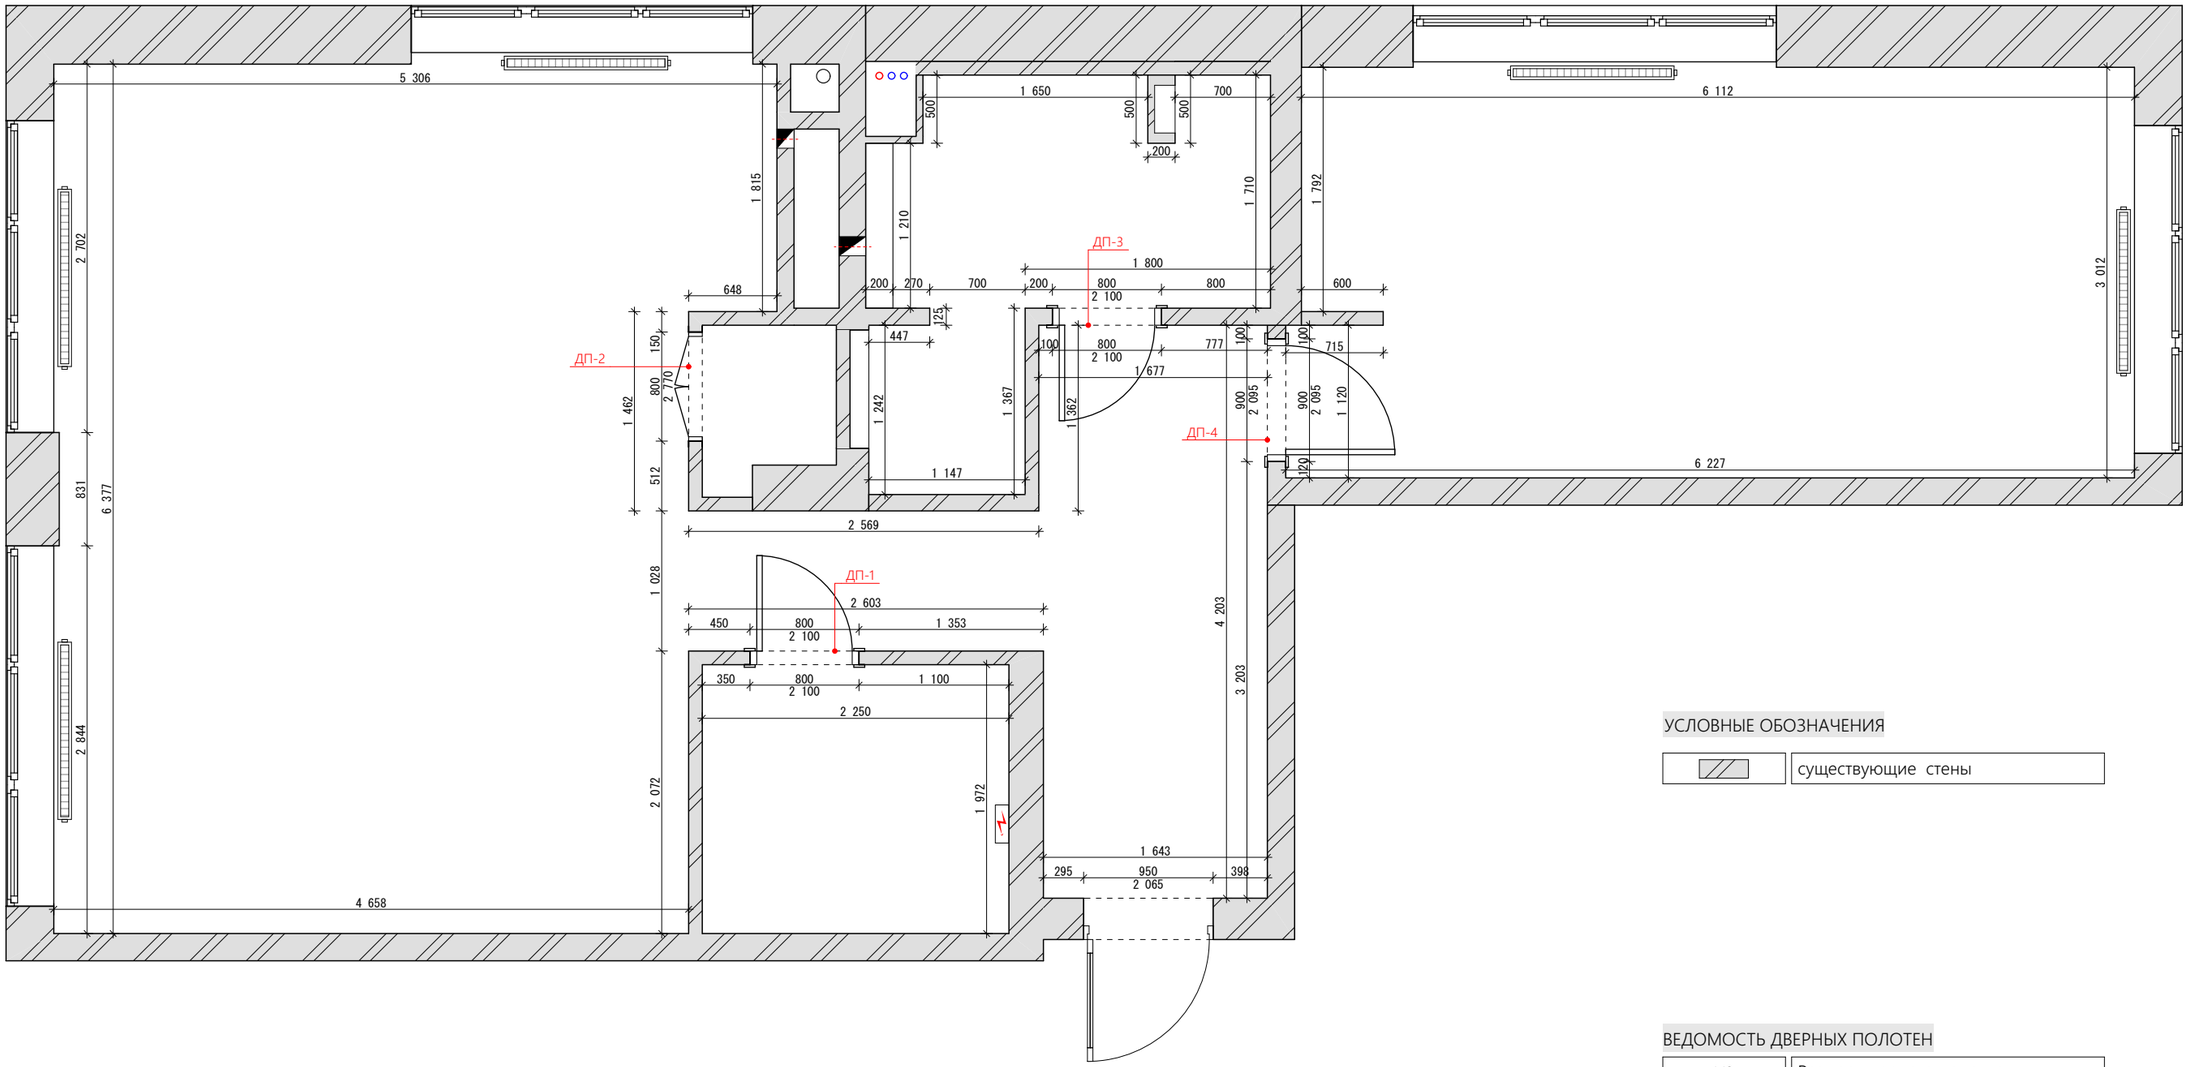

УСЛОВНЫЕ ОБОЗНАЧЕНИЯ

	существующие стены


ВЕДОМОСТЬ ДВЕРНЫХ ПОЛОТЕН

№	Размер дверного полотна
ДП-1	дверное полотно межкомнат. двери 700х2000мм
ДП-2	мебельная распашная дверь, размеры полотна согласовать с производителем
ДП-3	дверное полотно межкомнат.двери 700х2000мм
ДП-4	дверное полотно межкомнат.двери 800х2000мм

ПРИМЕЧАНИЯ

1. Все размеры указаны в миллиметрах.
2. Размеры даны без учета отделочных слоев.
3. Ширину проёмов проверить, и выполнить в соответствии с требованиям по установке дверных коробок.
4. Размеры межкомнатных проемов уточнить после окончательного согласования моделей дверей.

		Подпись	Дата		Стадия	Лист
Руководитель:					ДП	09
Дизайнер:						
Выполнил:				План формирования дверных проемов		
Заказчик:						

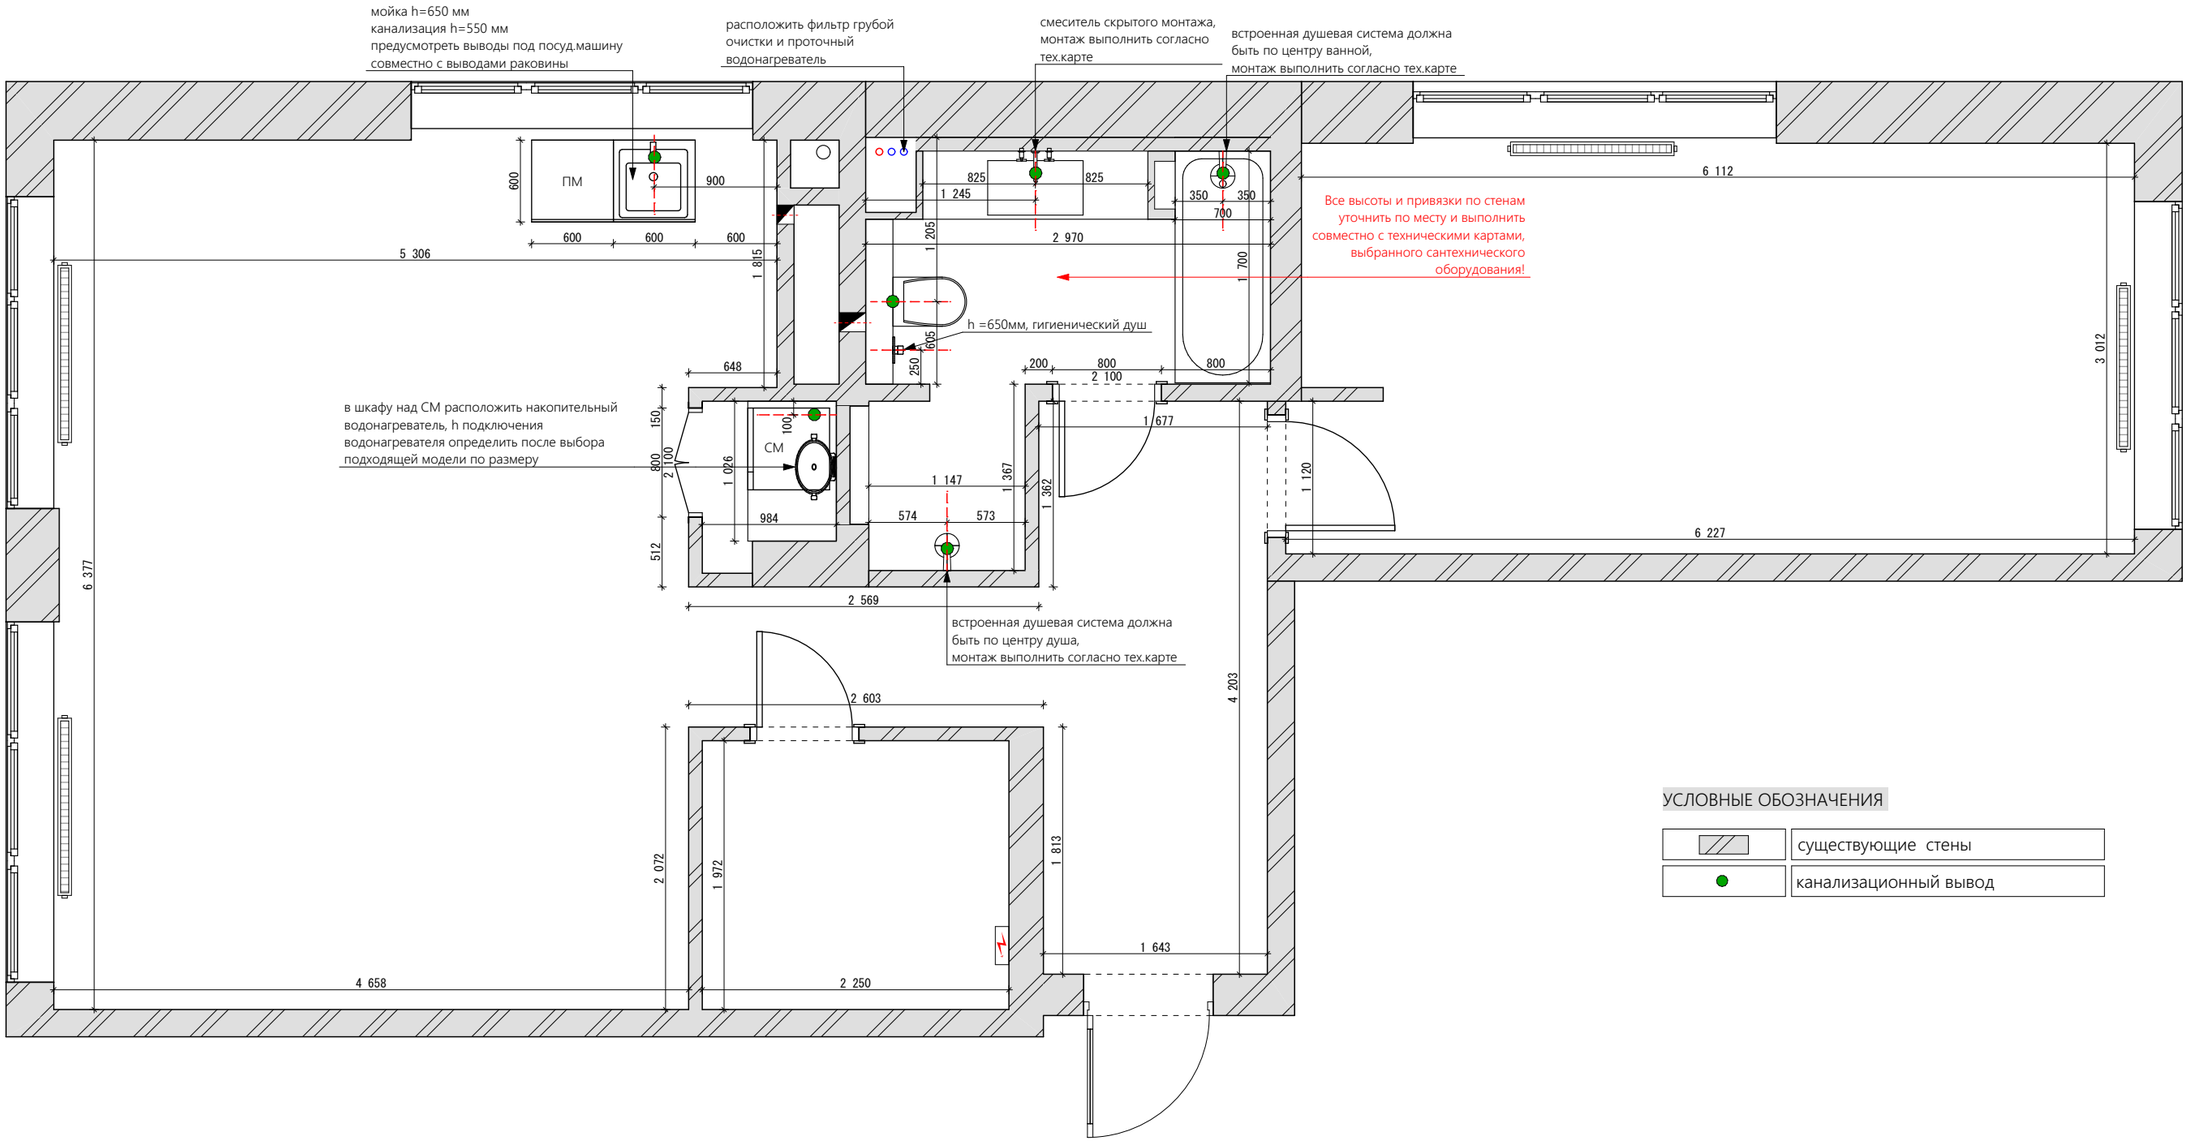


УСЛОВНЫЕ ОБОЗНАЧЕНИЯ

	существующие стены
	канализационный вывод

ПРИМЕЧАНИЯ

1. Все размеры указаны в миллиметрах.
2. Размеры даны без учета отделочных слоев.
3. Коммуникации штробим(уточнить по месту).
4. Привязка по оси сантехнического оборудования.
5. Все высоты и привязки по стенам уточнить по месту и выполнить совместно с техническими картами, выбранного сантехнического оборудования!
6. Установка сантехнического оборудования согласно тех. картам.

		Подпись	Дата		Стадия	Лист
Руководитель:					ДП	10
Дизайнер:						
Выполнил:				План расстановки сантехнического оборудования		
Заказчик:						

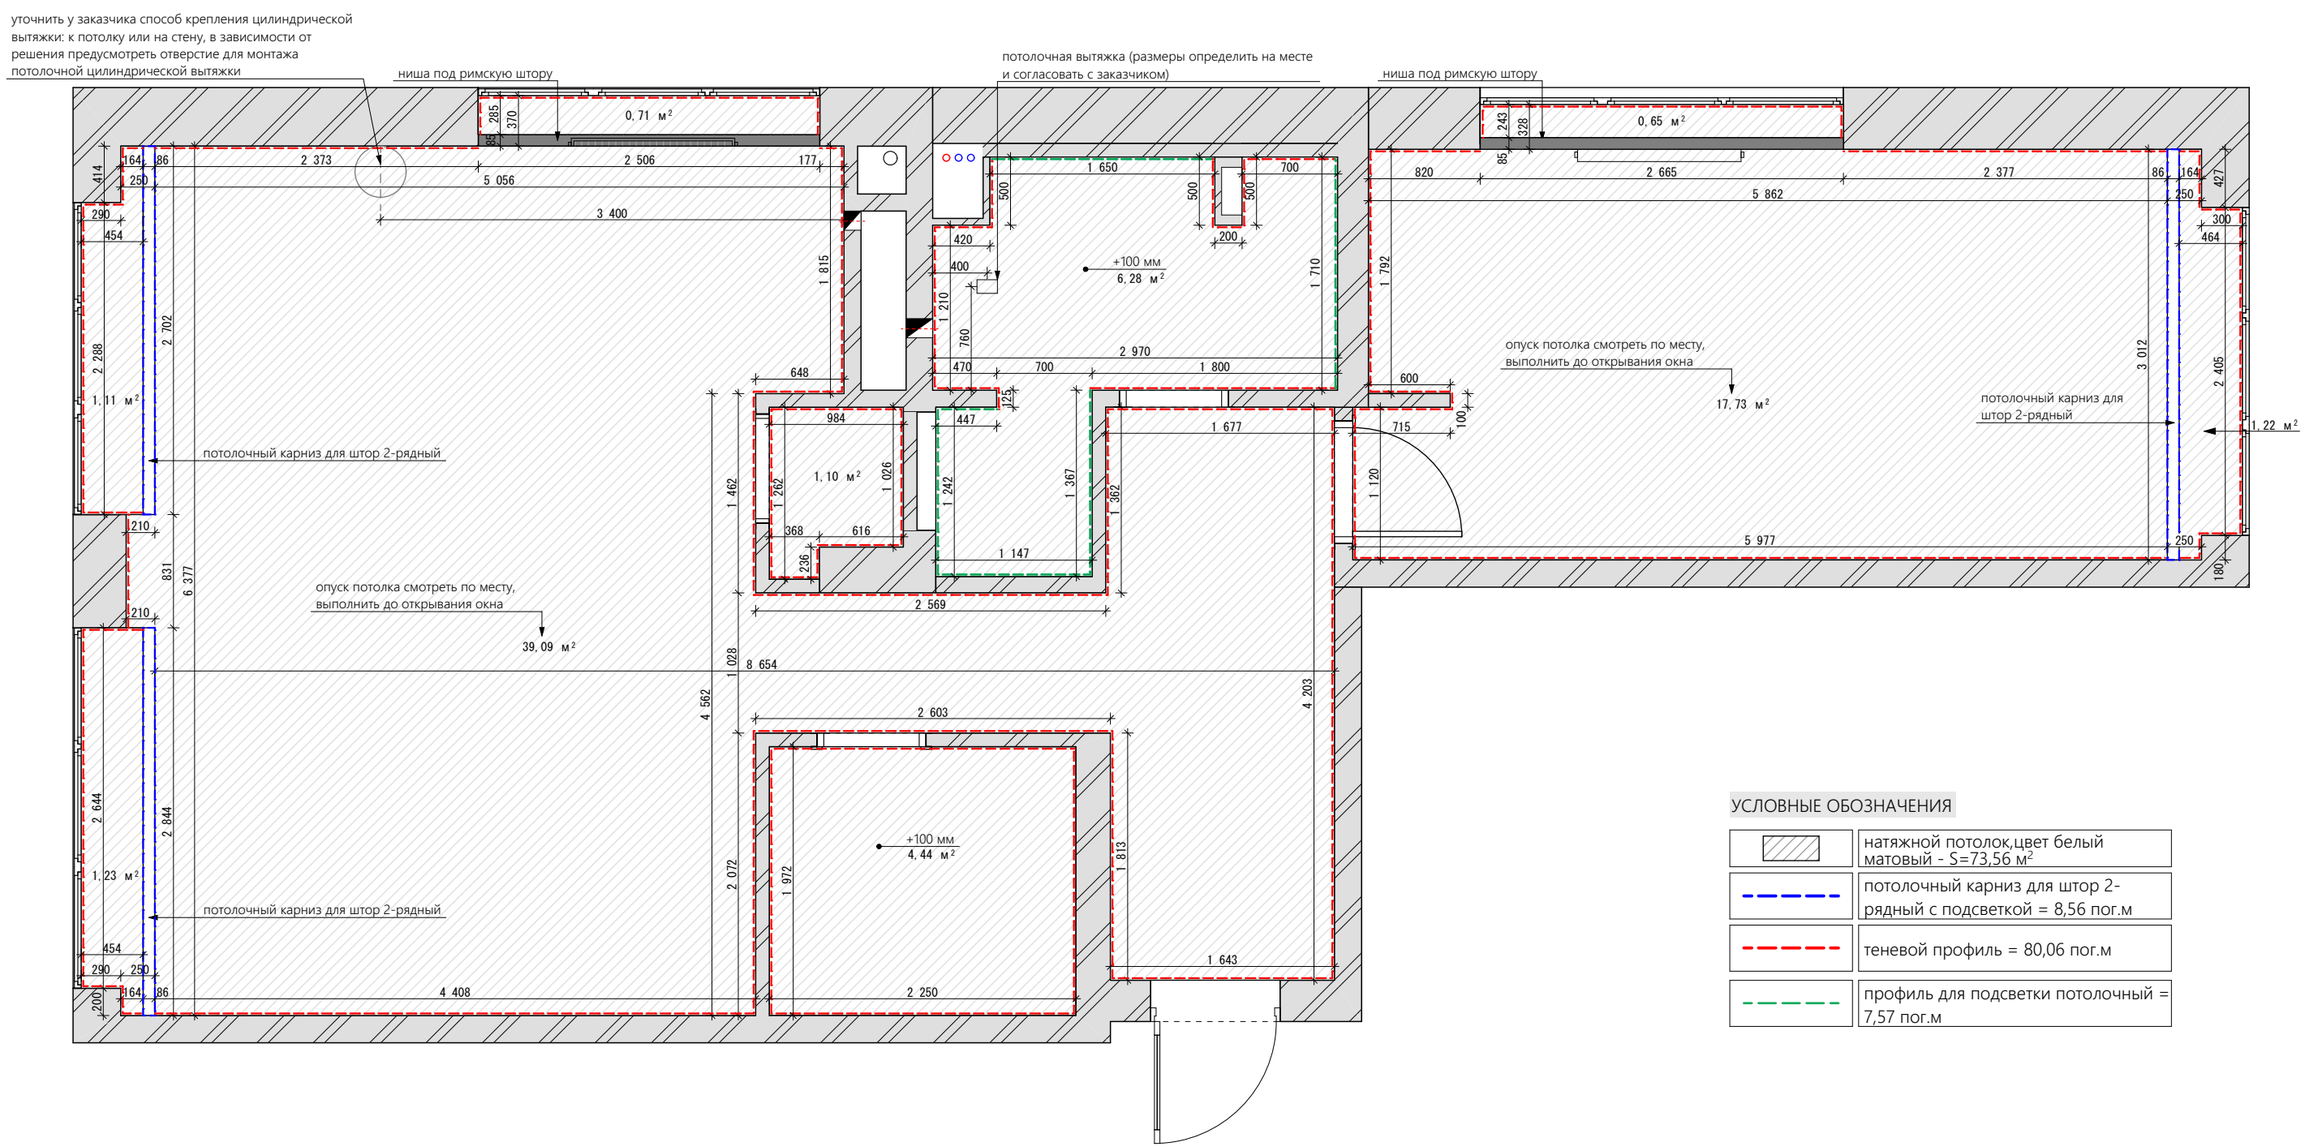


УСЛОВНЫЕ ОБОЗНАЧЕНИЯ

	натяжной потолок,цвет белый матовый - S=73,56 м²
	потолочный карниз для штор 2-рядный с подсветкой = 8,56 пог.м
	теневой профиль = 80,06 пог.м
	профиль для подсветки потолочный = 7,57 пог.м

ПРИМЕЧАНИЕ

1. Все размеры указаны в миллиметрах.
2. Размеры даны без учета отделочных слоев.
3. Коммуникации штробим.
4. Перед монтажом потолков уточнить монтажную глубину выбранных светильников.

		Подпись	Дата		Стадия	Лист
Руководитель:					ДП	11
Дизайнер:						
Выполнил:				План потолков		
Заказчик:						

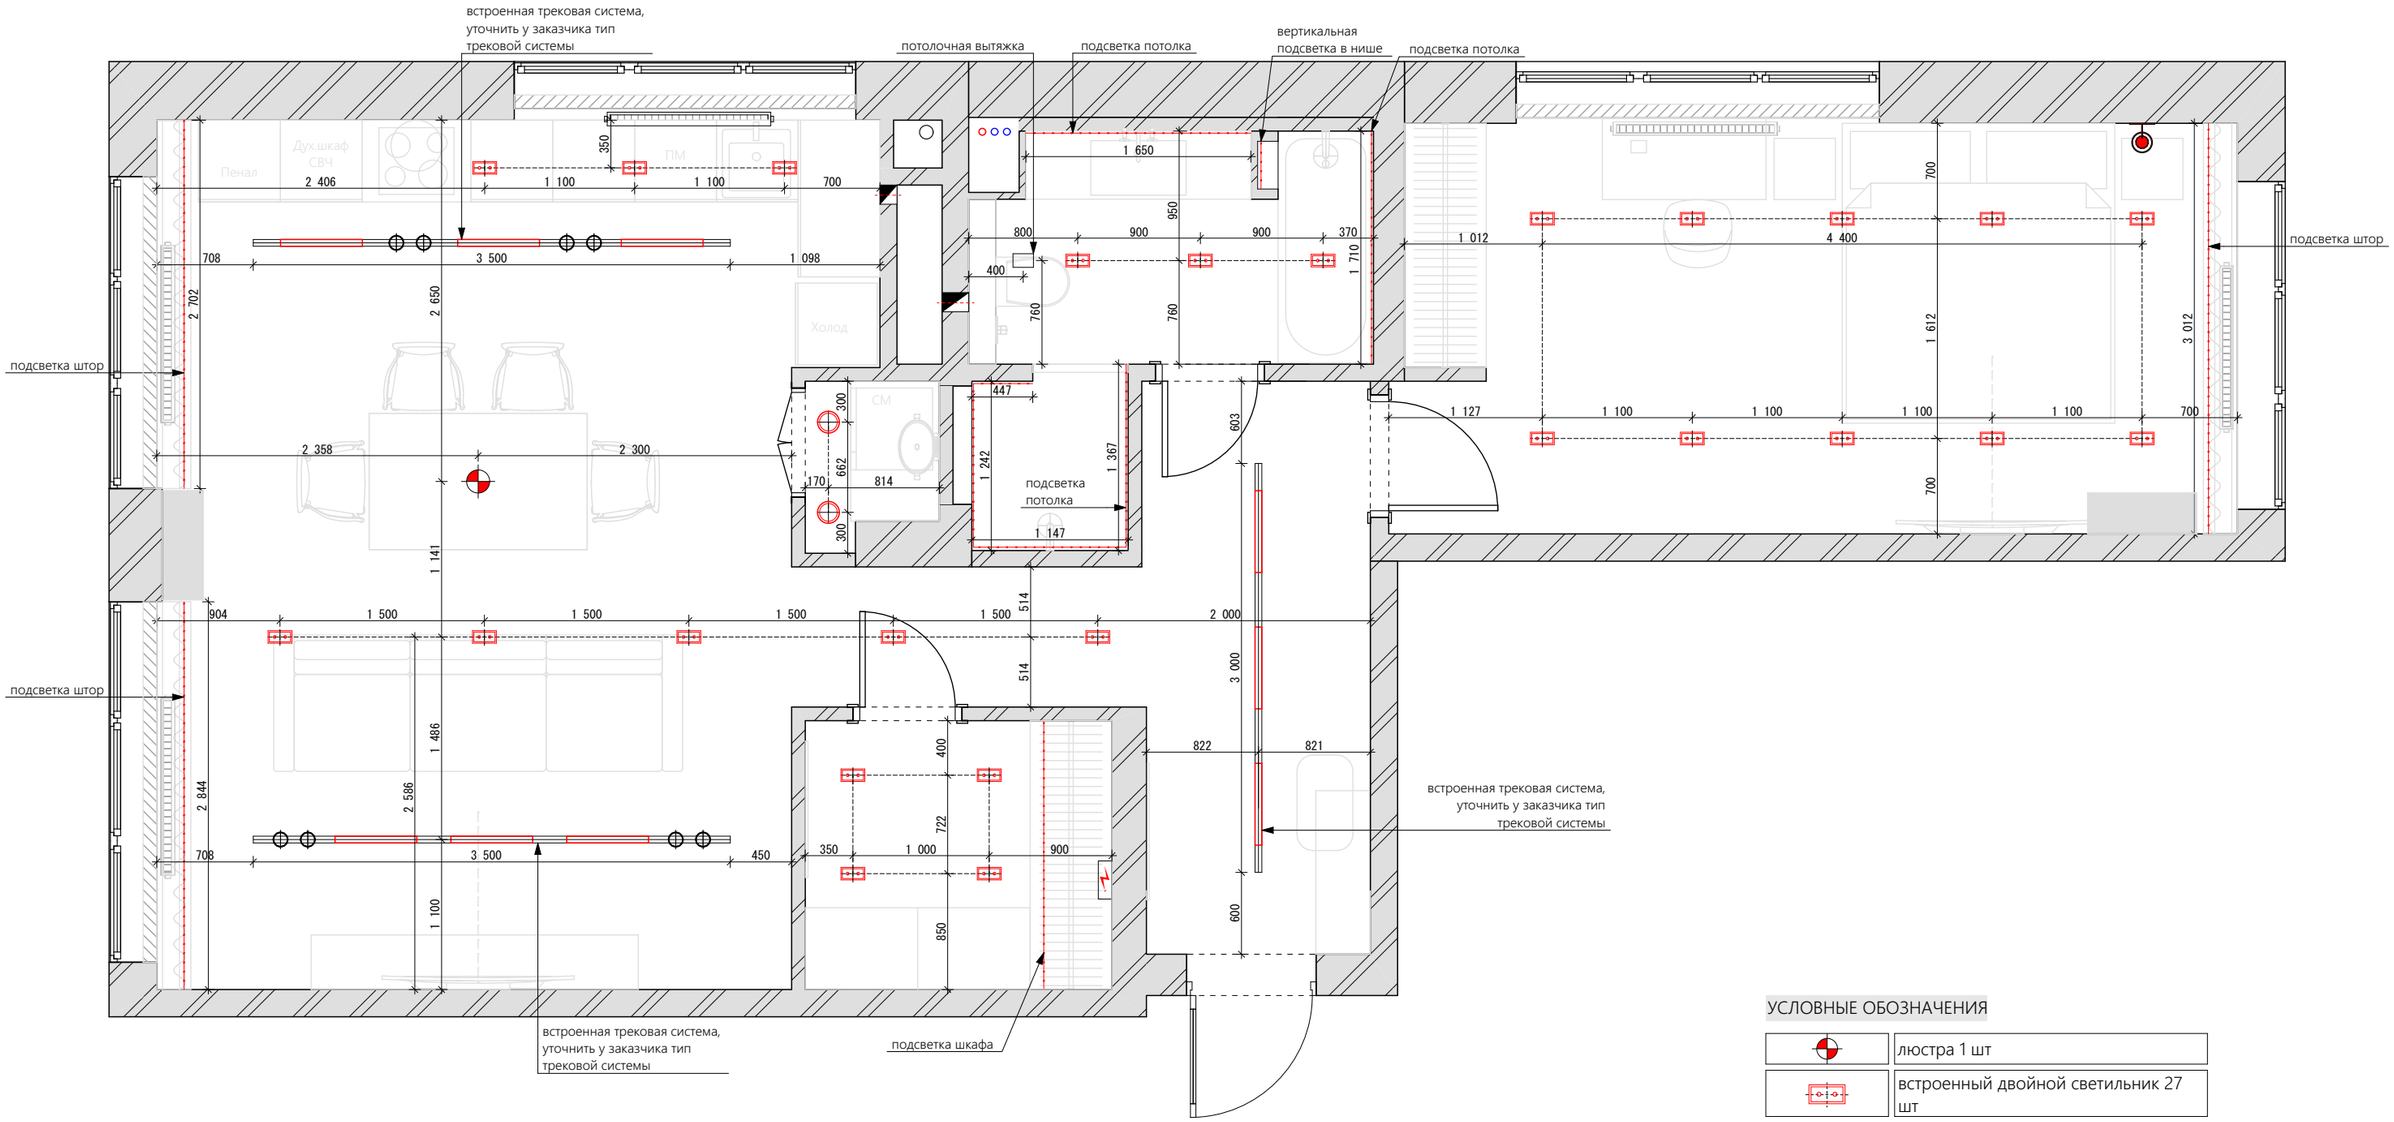


УСЛОВНЫЕ ОБОЗНАЧЕНИЯ

	люстра 1 шт
	встроенный двойной светильник 27 шт
	встроенный светильник 2 шт
	линейный трековый светильник 9 шт
	направленный трековый светильник 8 шт
	встроенная трековая система 13 пог.м
	бра 1 шт
	светодиодная лента 15,5 пог.м без учета подсветки мебели

ПРИМЕЧАНИЯ

1. Все размеры указаны в миллиметрах.
2. Размеры даны без учета отделочных работ.
3. Расположение осветительного оборудования указано относительно центра светильника.
4. Для электровыводов дать запас.

		Подпись	Дата		Стадия	Лист
Руководитель:					ДП	12
Дизайнер:						
Выполнил:				План расстановки осветительного оборудования		
Заказчик:						

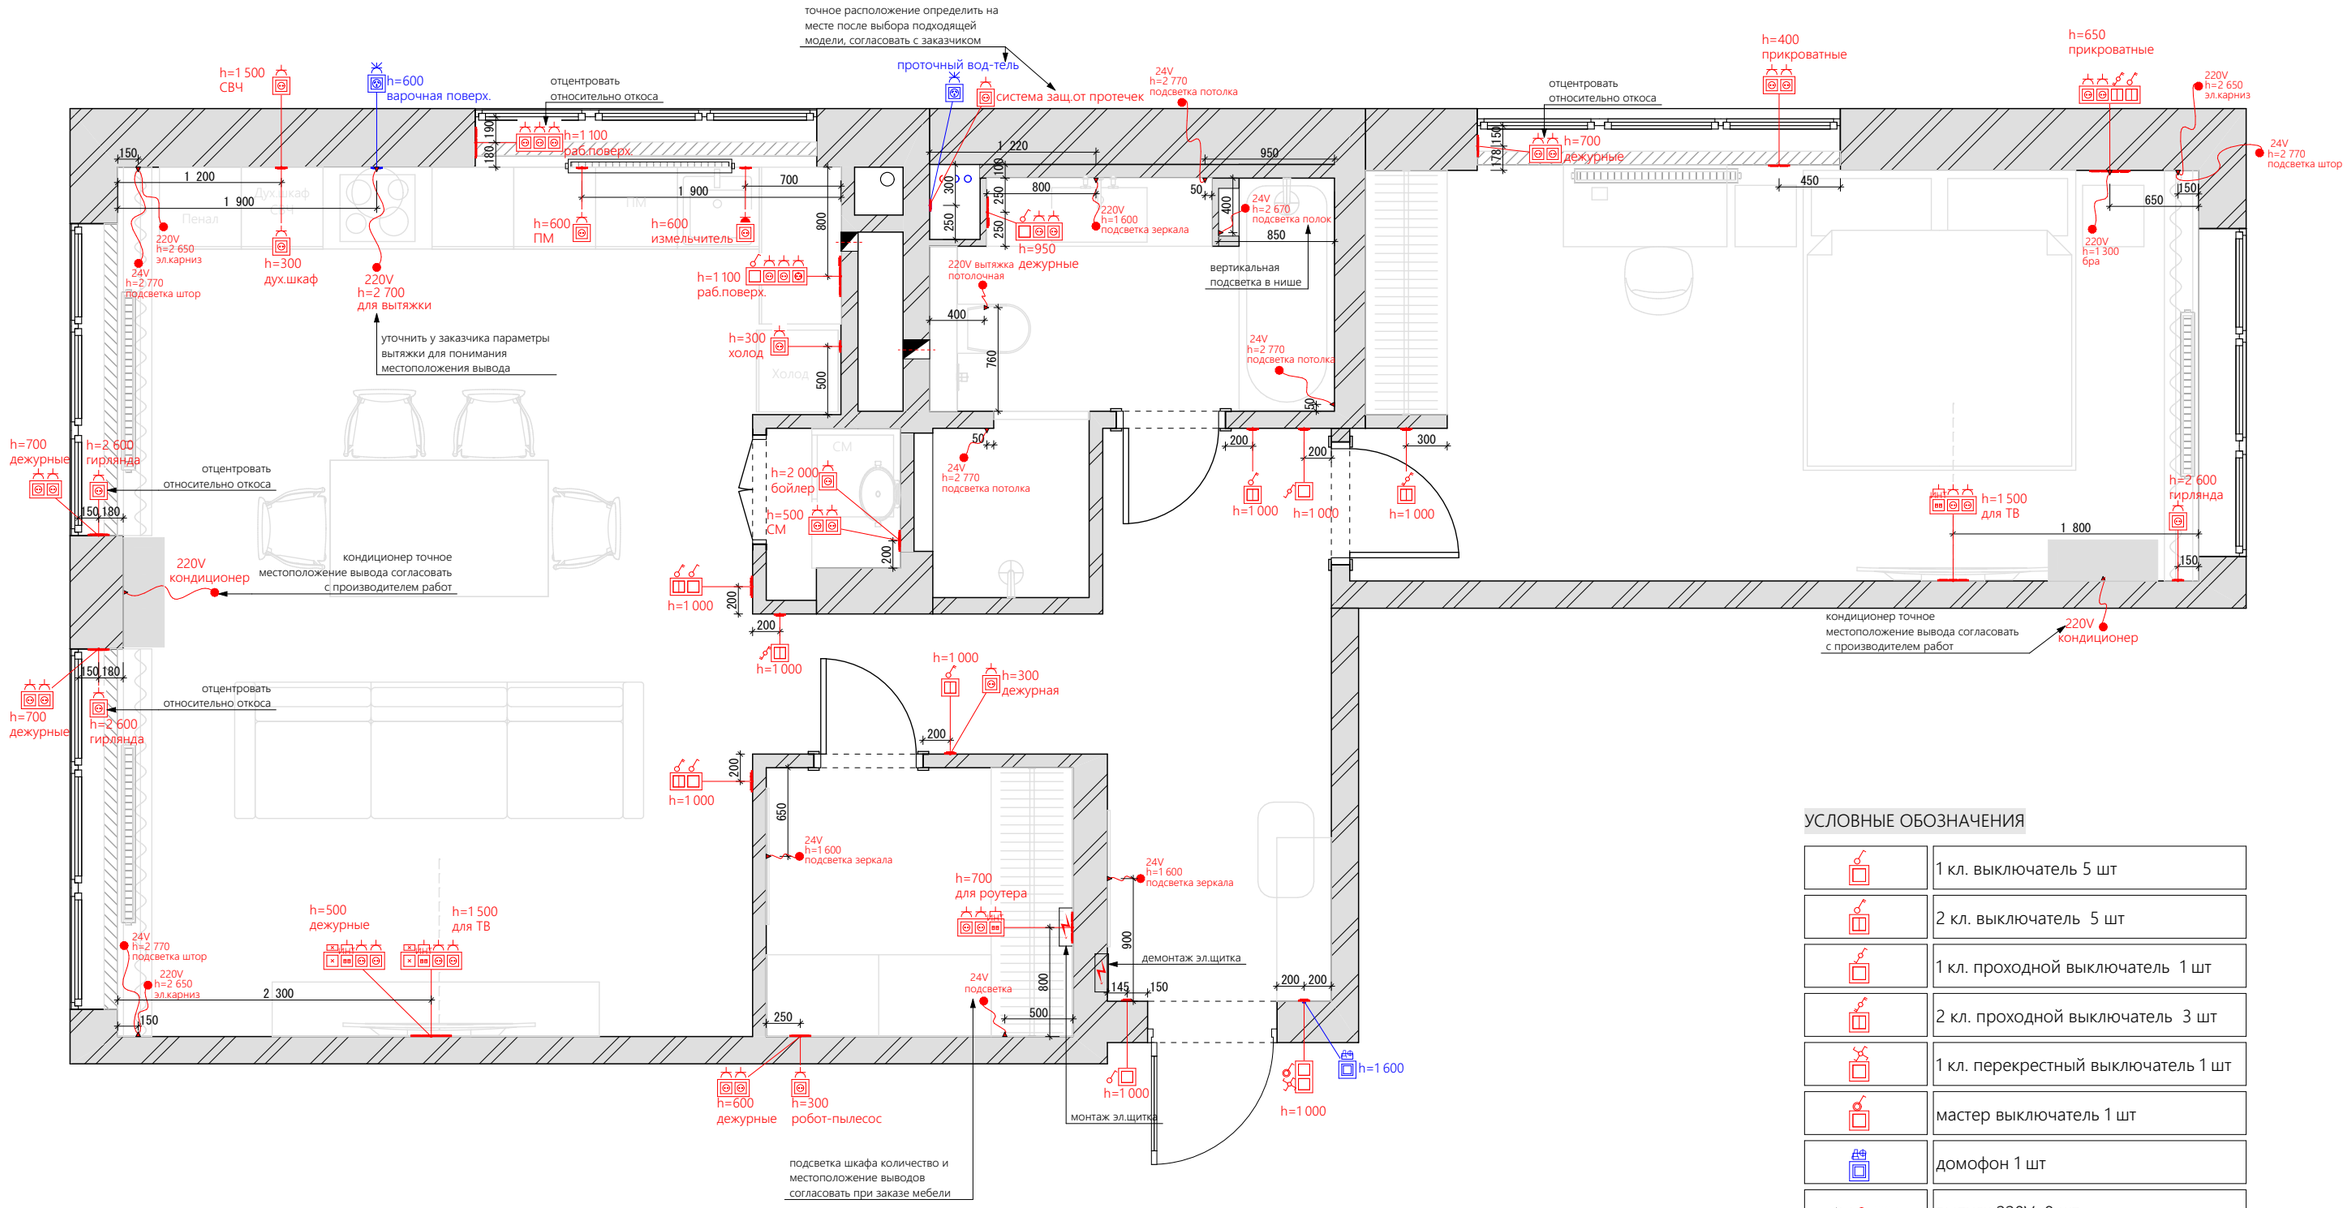


УСЛОВНЫЕ ОБОЗНАЧЕНИЯ

	1 кл. выключатель 5 шт
	2 кл. выключатель 5 шт
	1 кл. проходной выключатель 1 шт
	2 кл. проходной выключатель 3 шт
	1 кл. перекрестный выключатель 1 шт
	мастер выключатель 1 шт
	домофон 1 шт
220V	выпуск 220V 8 шт
24V	выпуск 24V 10 шт
	розетка 41 шт
	кабель-канал 2 шт
	силовой вывод 2 шт
	интернет 4 шт

ПРИМЕЧАНИЯ

1. Все размеры указаны в миллиметрах.
2. Размеры даны без учета отделочных слоев.
3. Расположение розеток и выводов указано относительно центра розетки или группы розеток.
4, Все розетки, необозначенные отметкой высоты, устанавливаются на высоту 300 мм от уровня пола, выключатели 1000 мм.
5. Точное расположение розеток и выводов для кухонной техники уточнить при заказе кухни.
6. Выводы под сплит-систему даны к нижней точке корпуса со стороны стены, согласно купленной модели.
7. Выводы в зонах TV требуют согласования с учетом выбранного оборудования.
8. Дать запас электр.выводам не менее 500мм.

		Подпись	Дата		Стадия	Лист
Руководитель:					ДП	13
Дизайнер:						
Выполнил:				План расположения розеток и выключателей		
Заказчик:						

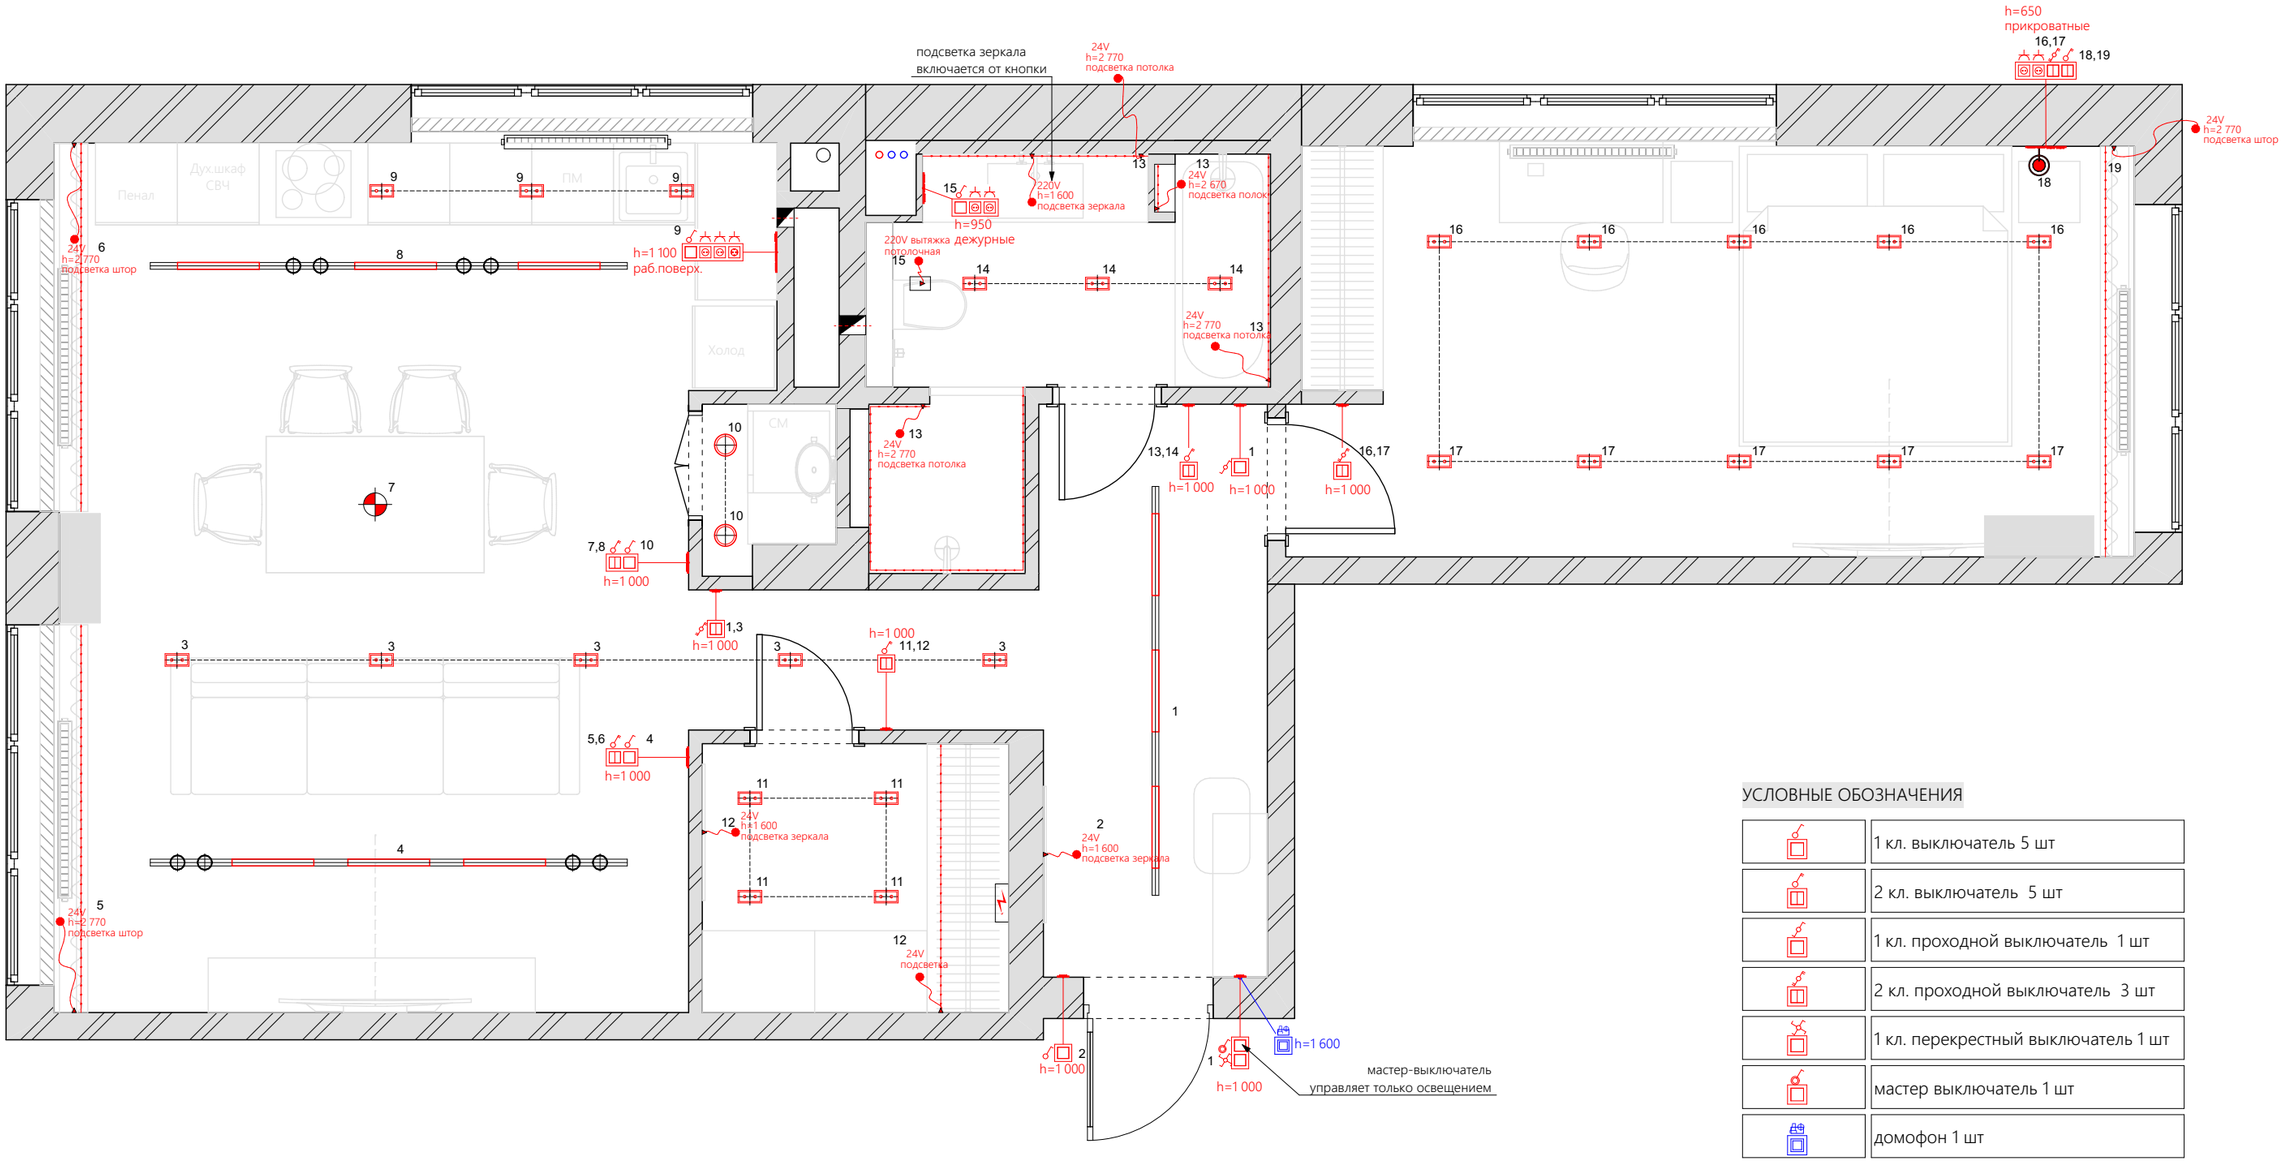


УСЛОВНЫЕ ОБОЗНАЧЕНИЯ

	1 кл. выключатель 5 шт
	2 кл. выключатель 5 шт
	1 кл. проходной выключатель 1 шт
	2 кл. проходной выключатель 3 шт
	1 кл. перекрестный выключатель 1 шт
	мастер выключатель 1 шт
	домофон 1 шт

ПРИМЕЧАНИЕ

1. Все размеры указаны в миллиметрах.
2. Размеры даны без учета отделочных слоев.
3. Расположение розеток и выводов указано относительно центра розетки или группы розеток.
4. Точное расположение розеток и выводов для кухонной техники уточнить при заказе кухни.

		Подпись	Дата		Стадия	Лист
Руководитель:					ДП	14
Дизайнер:						
Выполнил:				План управления осветительного оборудования		
Заказчик:						

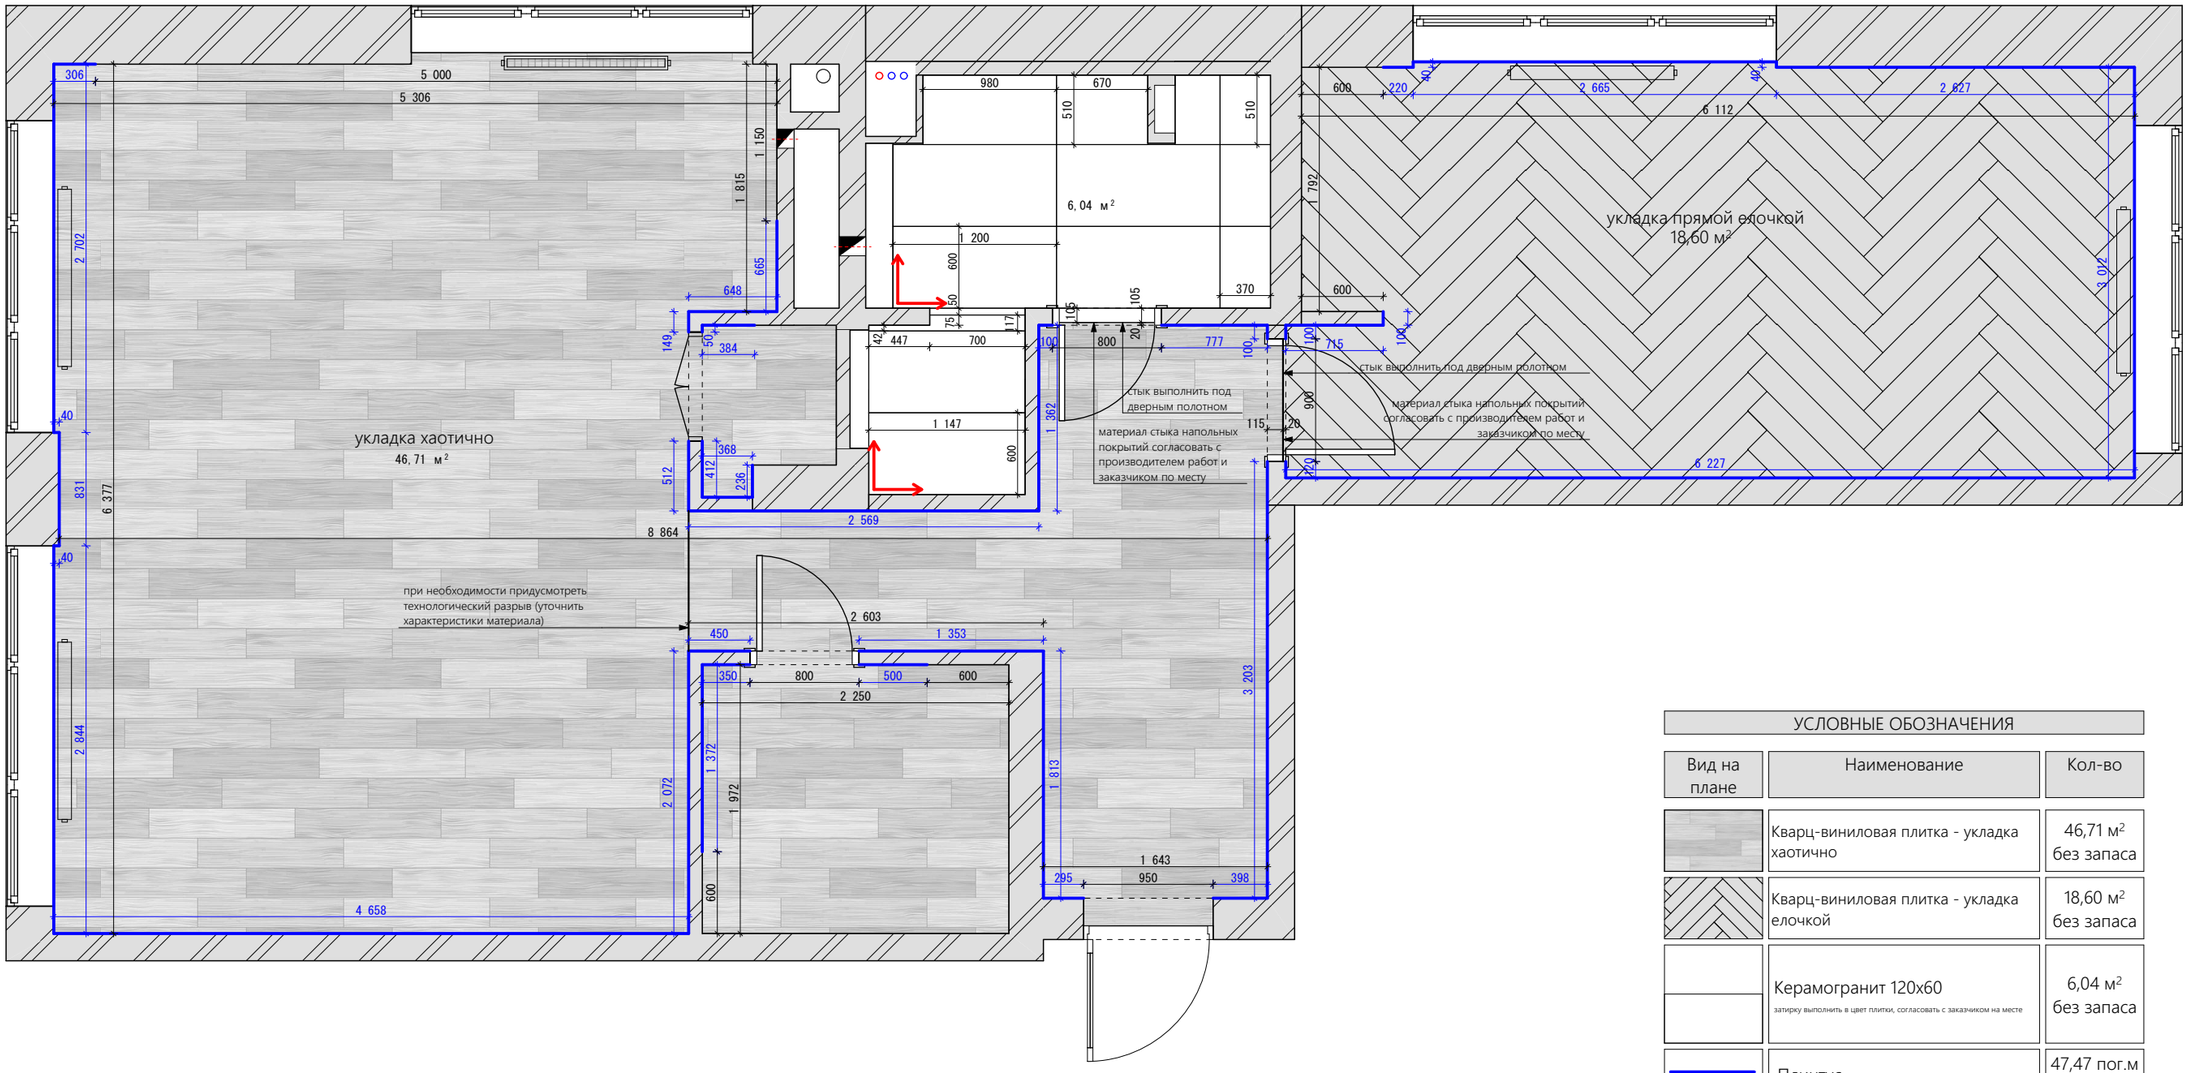

УСЛОВНЫЕ ОБОЗНАЧЕНИЯ


Вид на плане	Наименование	Кол-во
	Кварц-виниловая плитка - укладка хаотично	46,71 м² без запаса
	Кварц-виниловая плитка - укладка елочкой	18,60 м² без запаса
	Керамогранит 120х60 затирку выполнить в цвет плитки, согласовать с заказчиком на месте	6,04 м² без запаса
	Плинтус	47,47 пог.м без запаса
	Начало раскладки	

ПРИМЕЧАНИЯ


1. Все размеры указаны в миллиметрах.
2. Лист смотреть совместно с развертками стен.
3. Размеры даны без учета отделочных слоев.
4. Все площади посчитаны без запаса.
5. Направление укладки пола и все размеры уточняются после окончания общестроительных работ.
6. Границы технологического разрыва уточнить,монтаж производить после согласования с заказчиком и дизайнером.
7. Уровень полов санузла довести до уровня чистового пола во всех помещениях.

		Подпись	Дата		Стадия	Лист
Руководитель:					ДП	15
Дизайнер:						
Выполнил:				План раскладки напольных покрытий		
Заказчик:						

ПЛАН КУХНИ

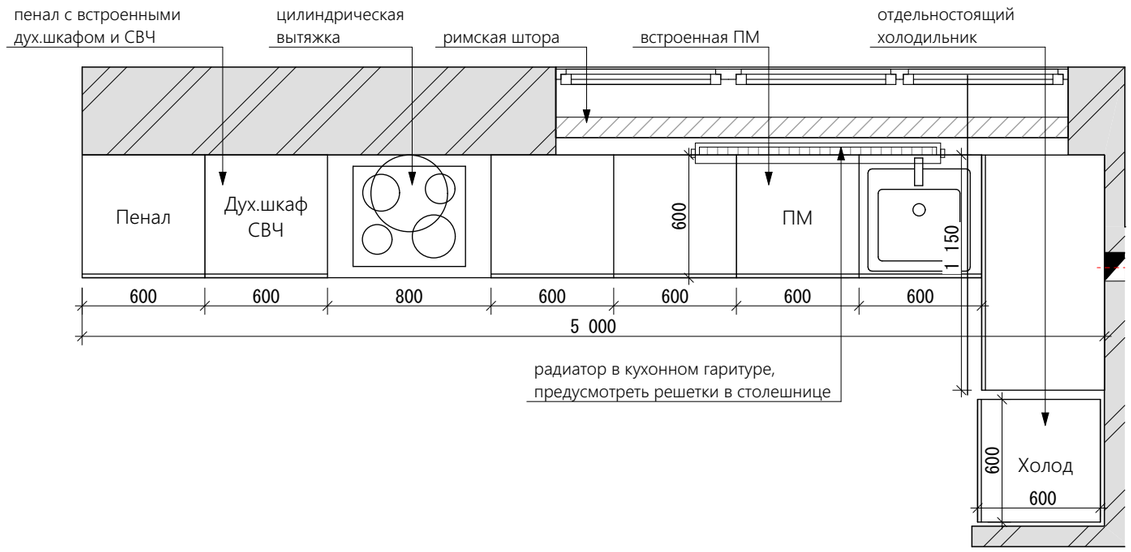

3D-ВИД

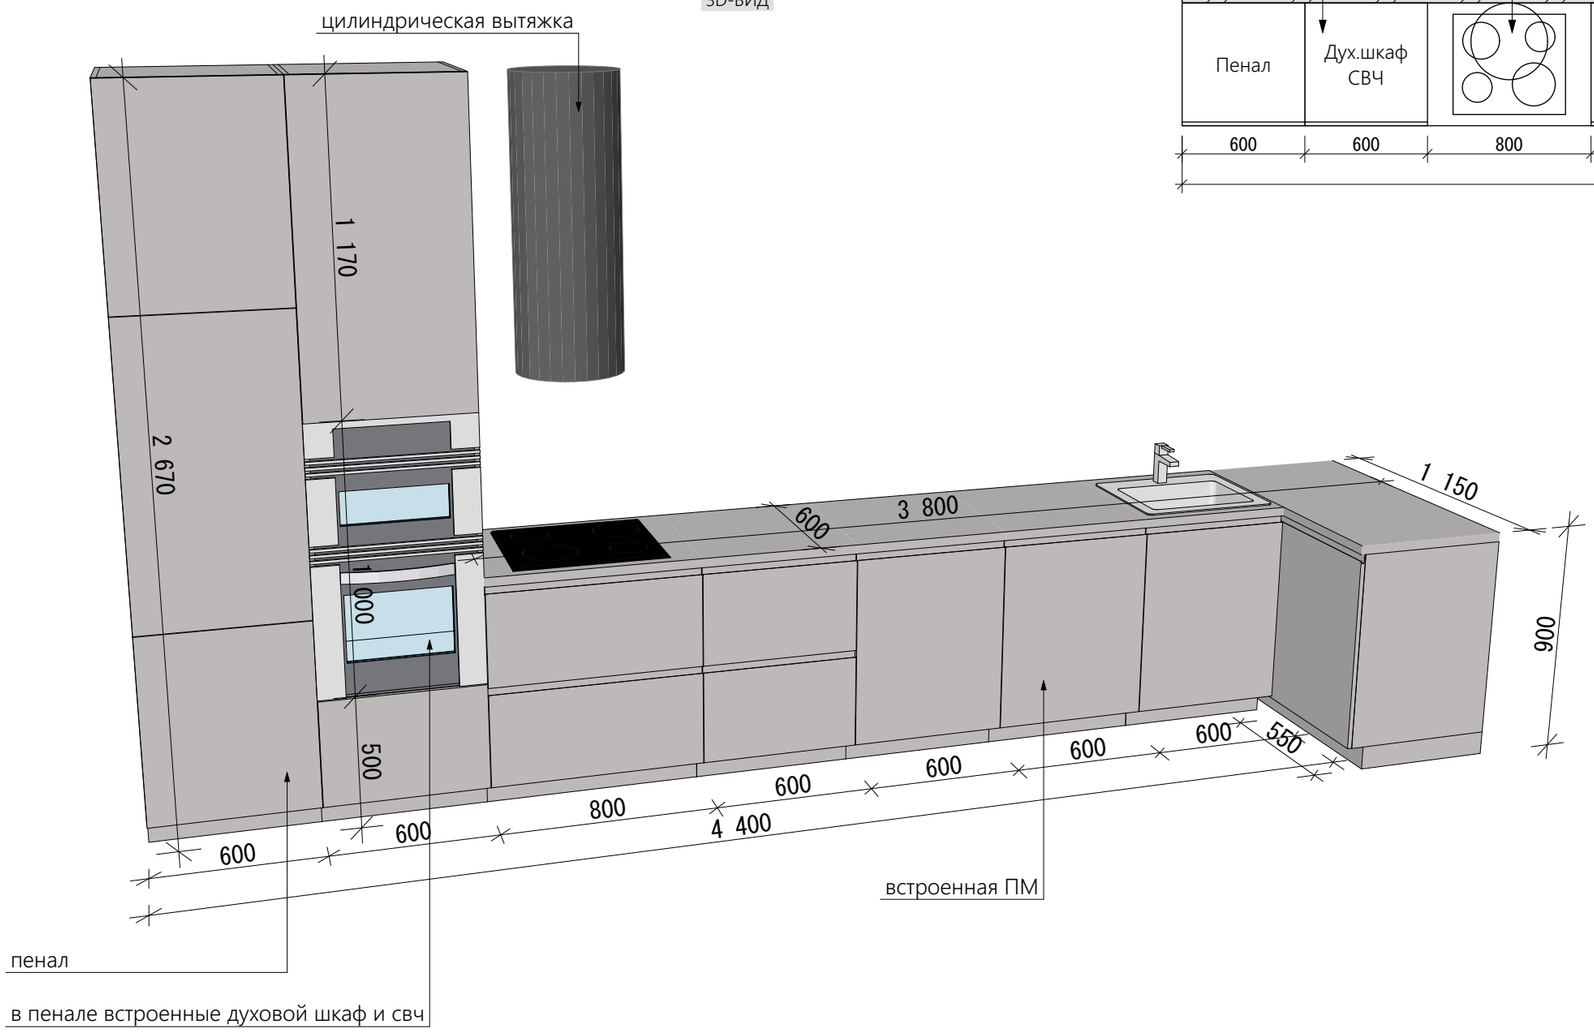

ПРИМЕЧАНИЕ

1. Все размеры указаны в миллиметрах.
2. Размеры даны без учета отделочных слоев.
3. Мебель индивидуального изготовления заказывать только после фактических обмеров по месту от производителя.
Все размеры даны только для предварительного просчета стоимости.

		Подпись	Дата		Стадия	Лист
Руководитель:					ДП	16
Дизайнер:						
Выполнил:				Развертка кухонного гарнитура		
Заказчик:						