ДИЗАЙН-ПРОЕКТ КВАРТИРЫ 83м²


ЖК Родные просторы

Ведомость рабочих чертежей

Имя листа	№ Листа
Титульный лист	1
Ведомость чертежей	2
Обмерочный план	3
Ведомость окон	4
План демонтажа	5
План монтажа	6
План расстановки мебели и оборудования	7
План формирования дверных проемов	8
Общий план расстановки сантехнических приборов	9
План с техническими картами сантехнических приборов	10
Развертка стен ванной комнаты. Привязка сантехники, раскладка плитки	11
Развертка стен санузла	12
План потолков	13
План расстановки осветительного оборудования	14
План расположения розеток и выключателей	15
План управления осветительным оборудованием	16
План привязки теплого пола	17
План раскладки напольных покрытий	18
Развертка стен прихожей	19
Развертка стен кухни-гостиной	20

Имя листа	№ Листа
Развертка стен детской	21
Развертка стен спальни	22
Развертка стен гардероба	23
Развертка стен балкона	24
Развертка по кухонному гарнитуру	25
Визуализация прихожей	26
Визуализации прихожей	27
Визуализация прихожей-кухни-гостиной	28
Визуализация кухни-гостиной	29
Визуализации кухни-гостиной	30
Визуализации кухни-гостиной	31
Визуализация балкона	32
Визуализация балкона	33
Визуализация санузла	34
Визуализация ванной комнаты	35
Визуализация ванной комнаты	36
Визуализация спальни	37
Визуализация спальни	38
Визуализация спальни	39

		Подпись	Дата		Стадия	Лист
					ДП	2
Дизайнер:						
Выполнил:				Ведомость чертежей		
Заказчик:						

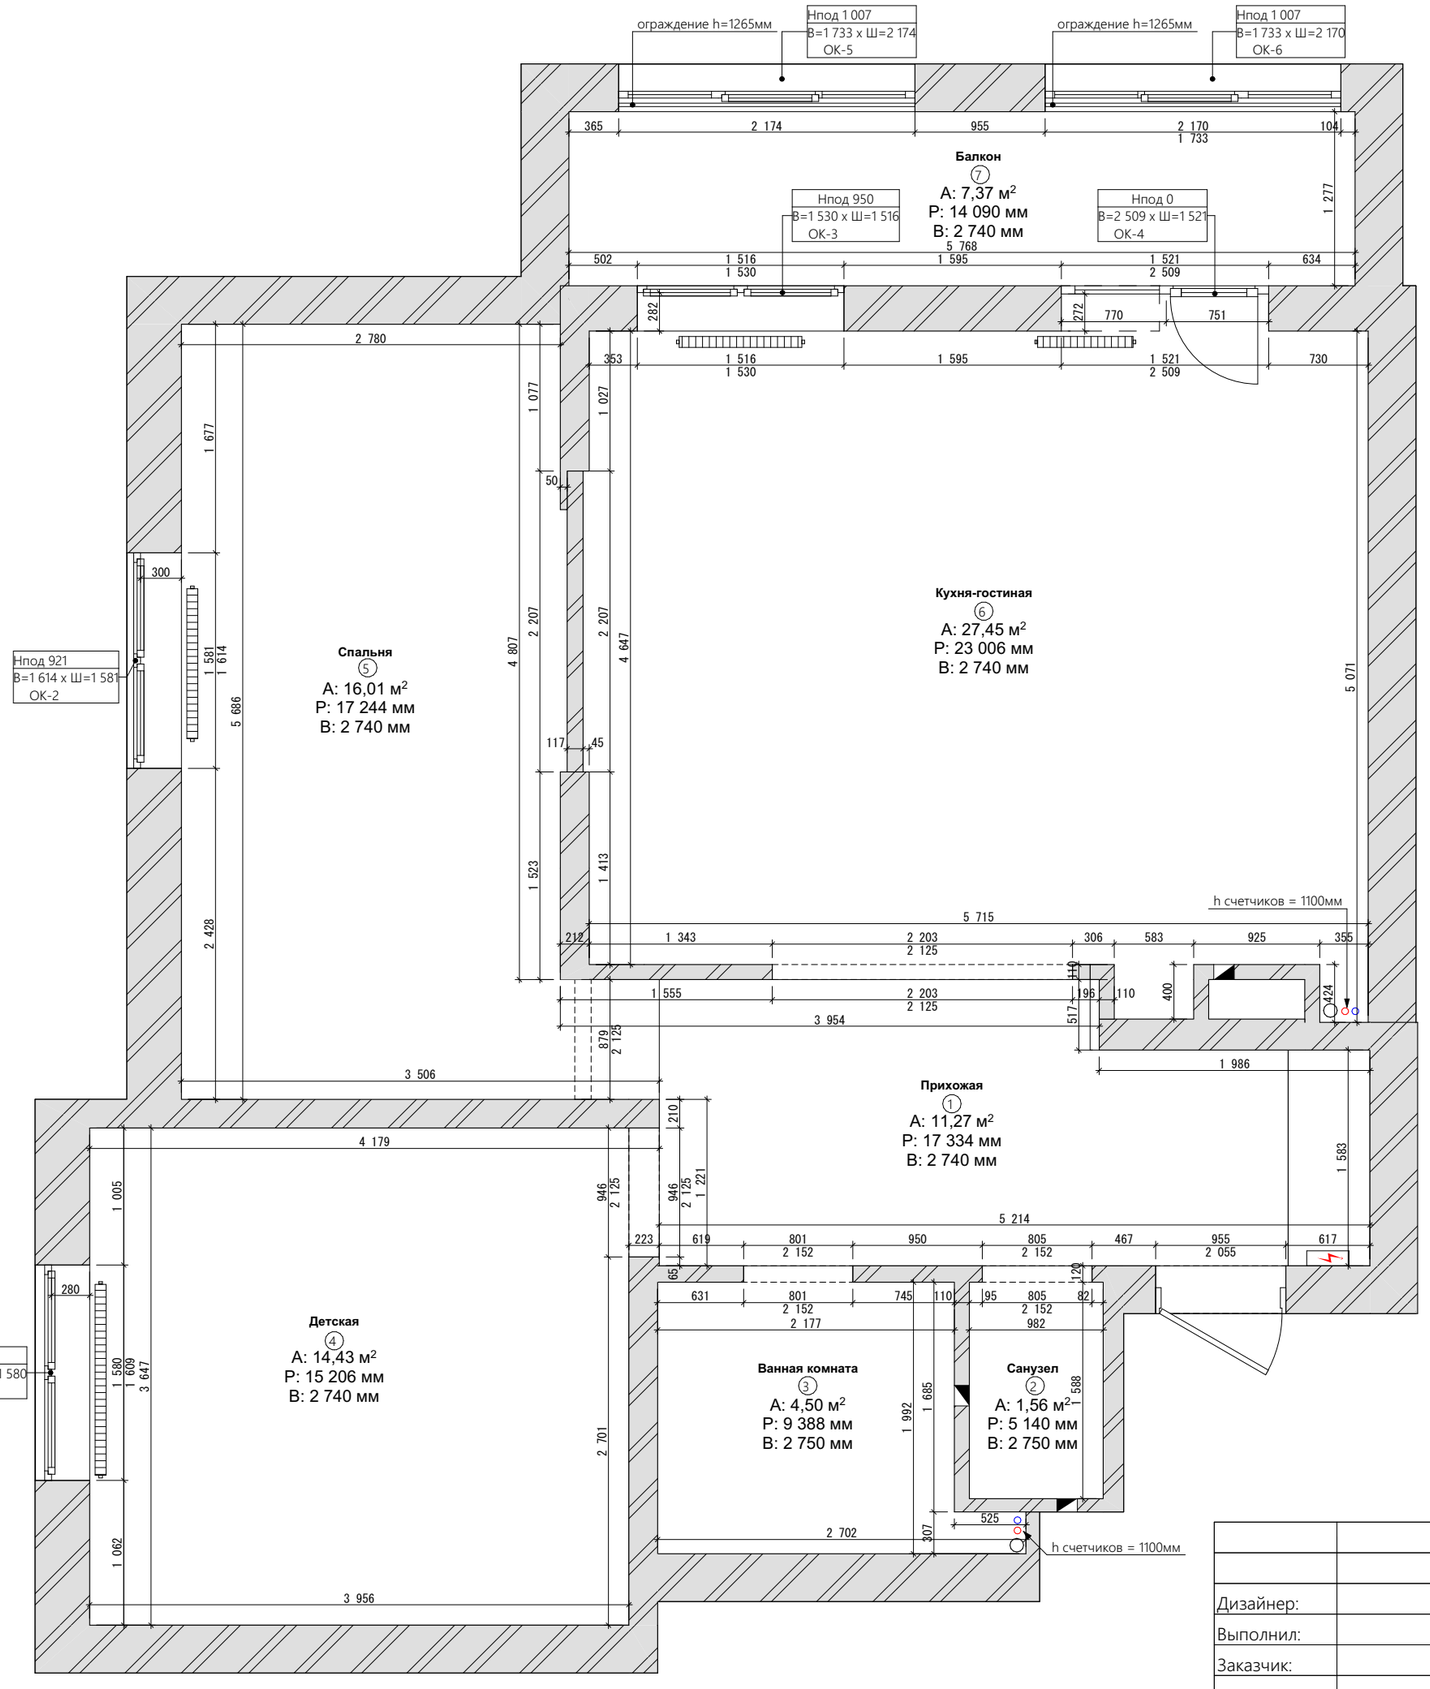

УСЛОВНЫЕ ОБОЗНАЧЕНИЯ

	существующие стены
	электрощиток
	водопровод канализация
	радиатор
	проем для вентиляции

А - площадь; Р - периметр; В - высота


ЭКСПЛИКАЦИЯ ПОМЕЩЕНИЙ


№	Наименование помещения	Площадь, м2
1	Прихожая	11,27
2	Санузел	1,56
3	Ванная комната	4,50
4	Детская	14,43
5	Спальня	16,01
6	Кухня-гостиная	27,45
7	Балкон	7,37
		82,59 м²


ПРИМЕЧАНИЯ


1. Все размеры указаны в миллиметрах.
2. Размеры даны без учета отделочных слоев.
3. Все размеры проверить по месту, возможны погрешности.
4. Отметка высоты указана относительно уровня существующего жб перекрытия.
5. За отметку 0.000 принят уровень существующего пола на момент замера.
6. Все помещения оштукатурены.

		Подпись	Дата		Стадия	Лист
					ДП	3
Дизайнер:						
Выполнил:				Обмерочный план		
Заказчик:						

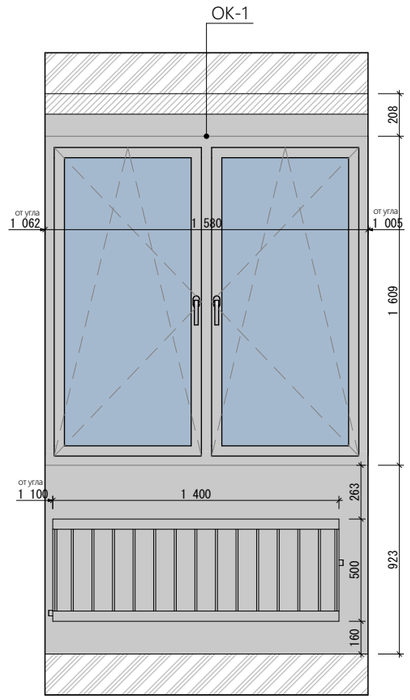


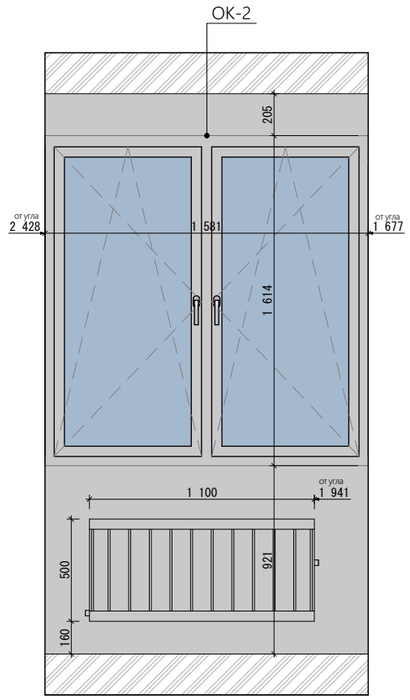

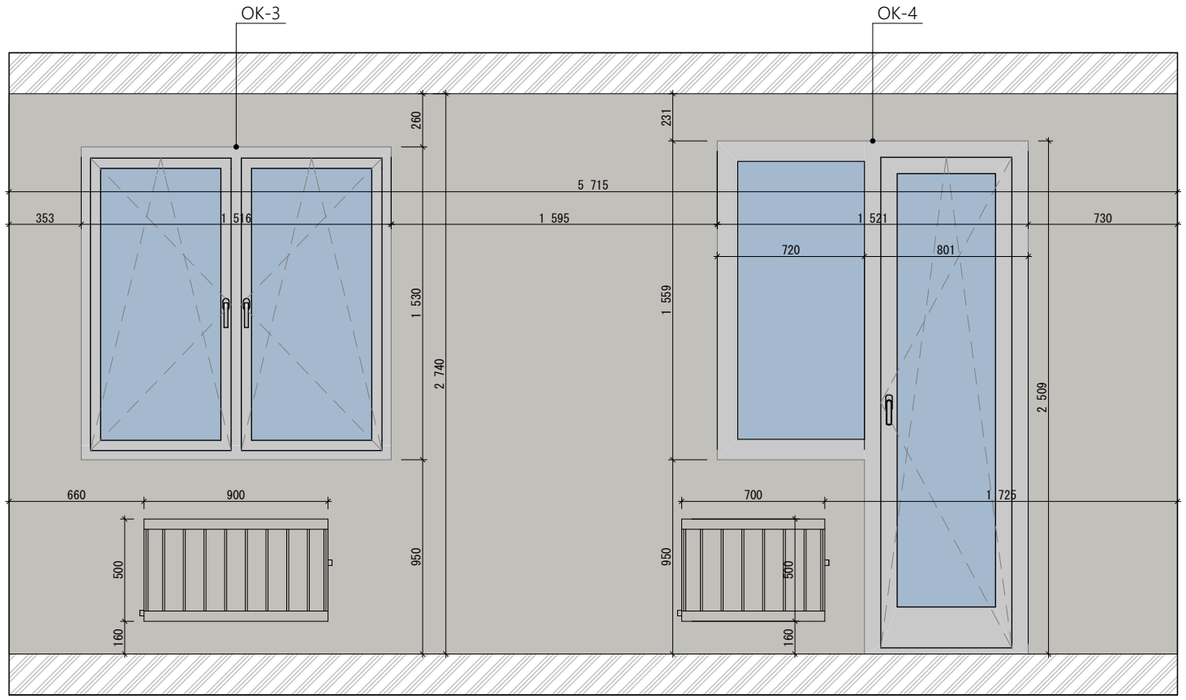

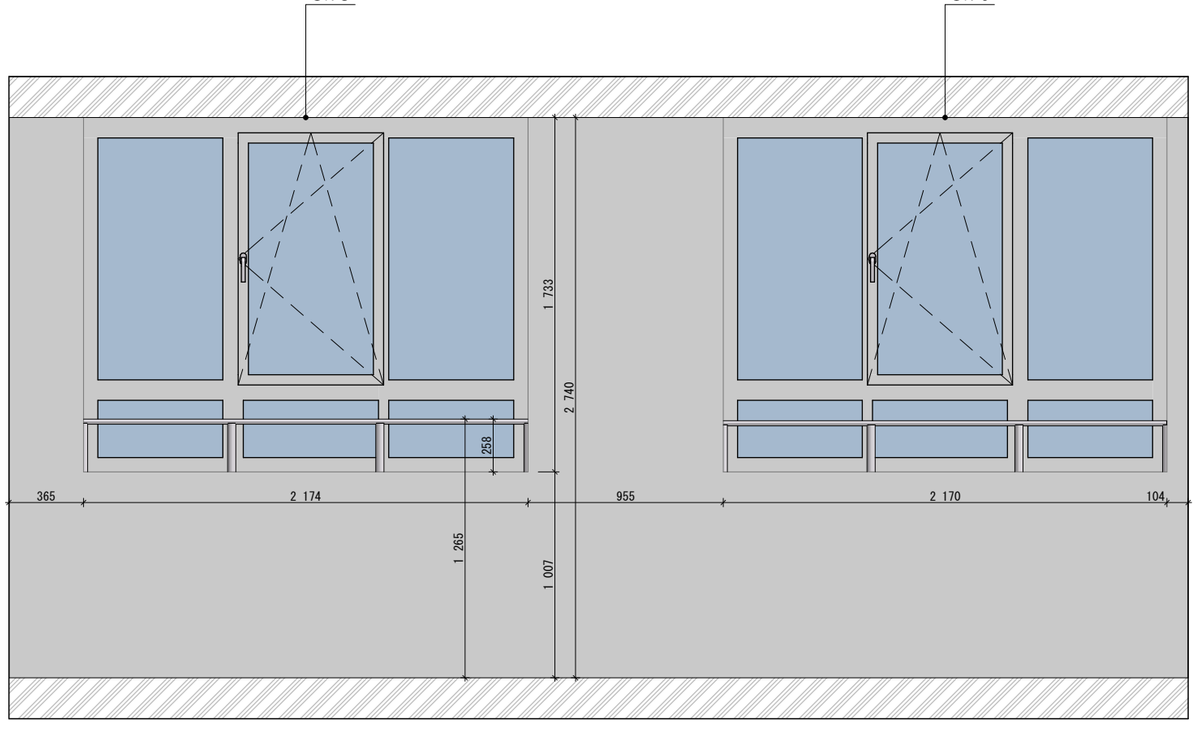

		Подпись	Дата		Стадия	Лист
					ДП	4
Дизайнер:						
Выполнил:				Ведомость окон		
Заказчик:						

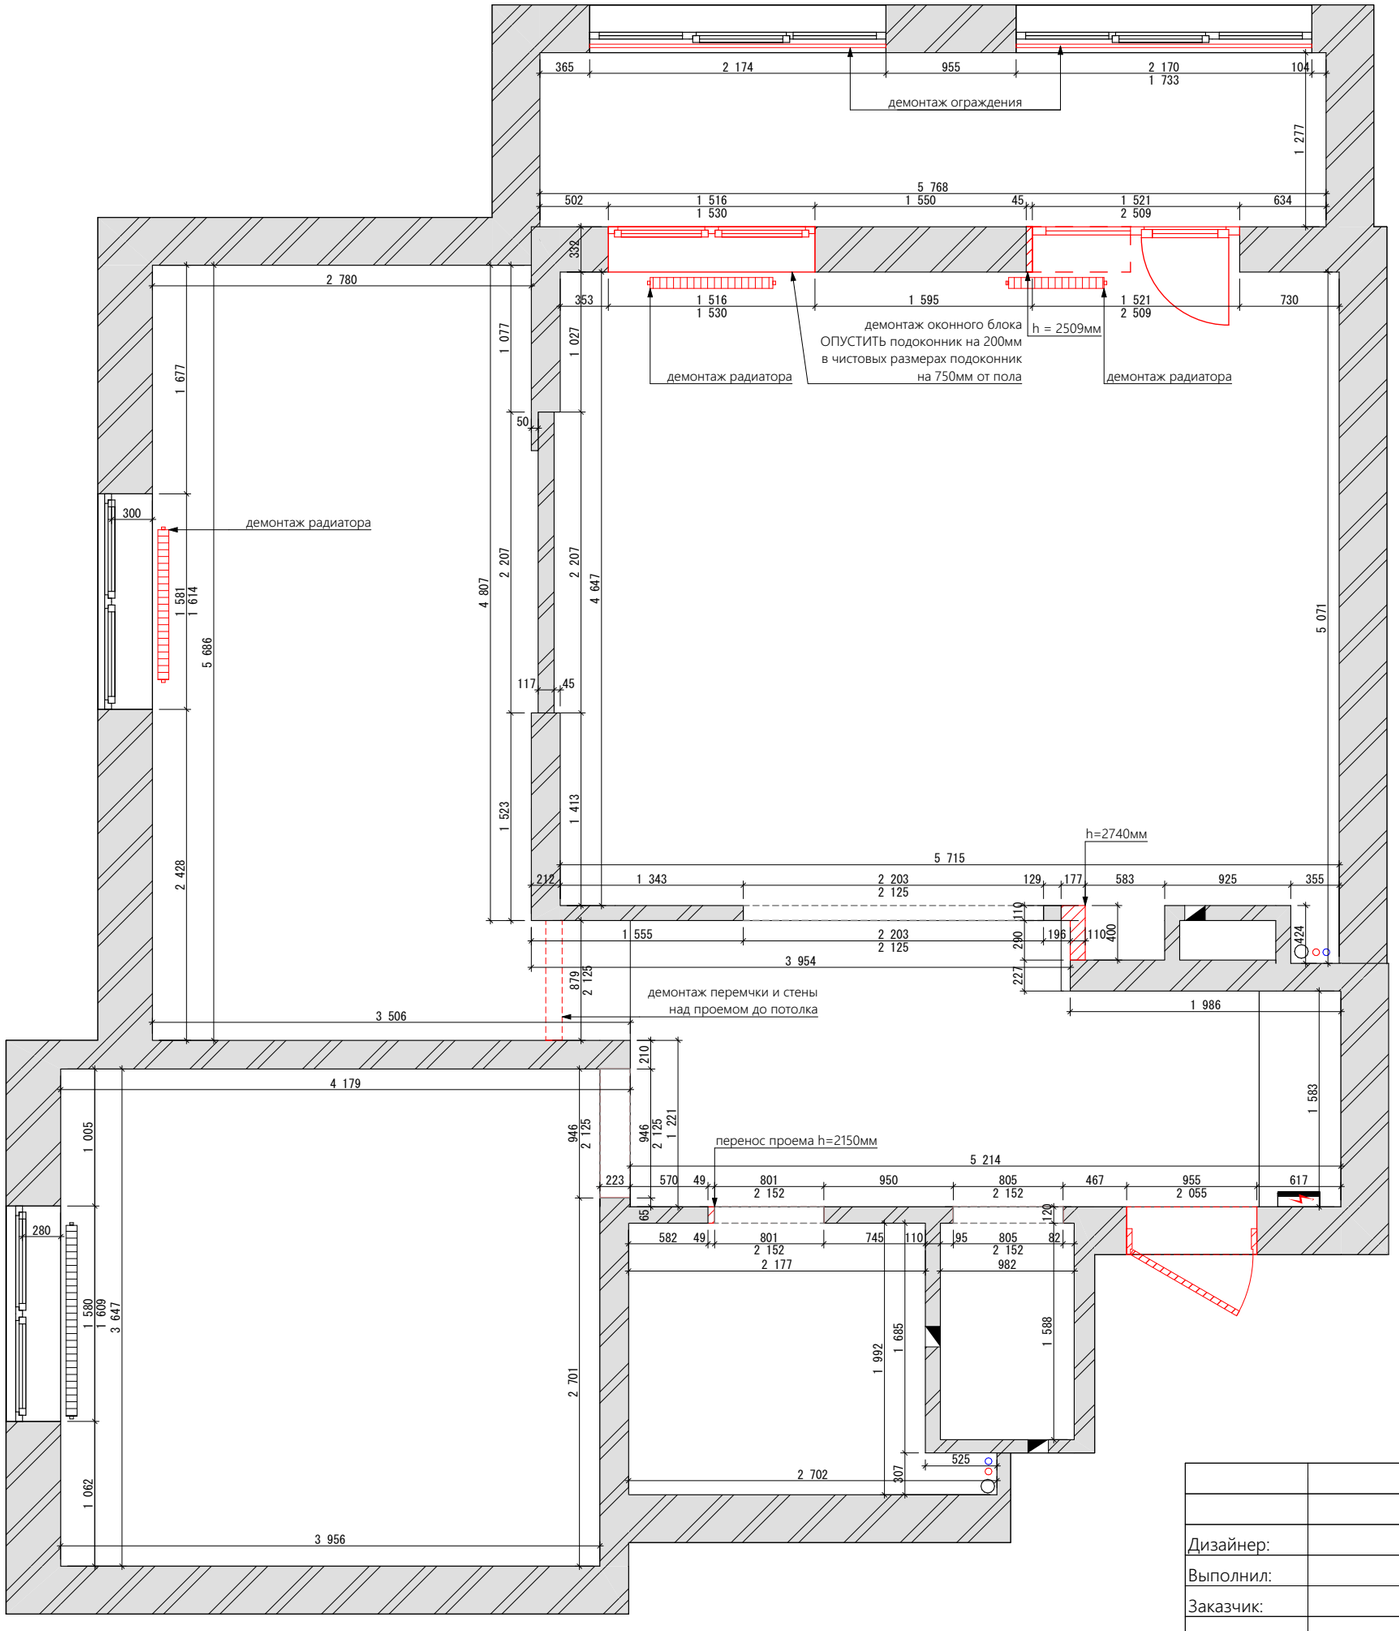


УСЛОВНЫЕ ОБОЗНАЧЕНИЯ

	существующие стены
	демонтируемые стены
	электрощиток
	проем для вентиляции
	водопровод канализация
	радиатор

ПРИМЕЧАНИЯ:

1. Все размеры указаны в миллиметрах.
2. Размеры даны без учета отделочных слоев.
3. Размеры проверить по месту.
4. Вносимые изменения в существующую планировку квартиры (демонтаж, монтаж, перенос радиаторов, канализации и т.п.) требуют согласования в государственных и муниципальных учреждениях либо самостоятельно, либо через специализированные организации и являются ответственностью Заказчика.

		Подпись	Дата		Стадия	Лист
					ДП	5
Дизайнер:						
Выполнил:				План демонтажа		
Заказчик:						

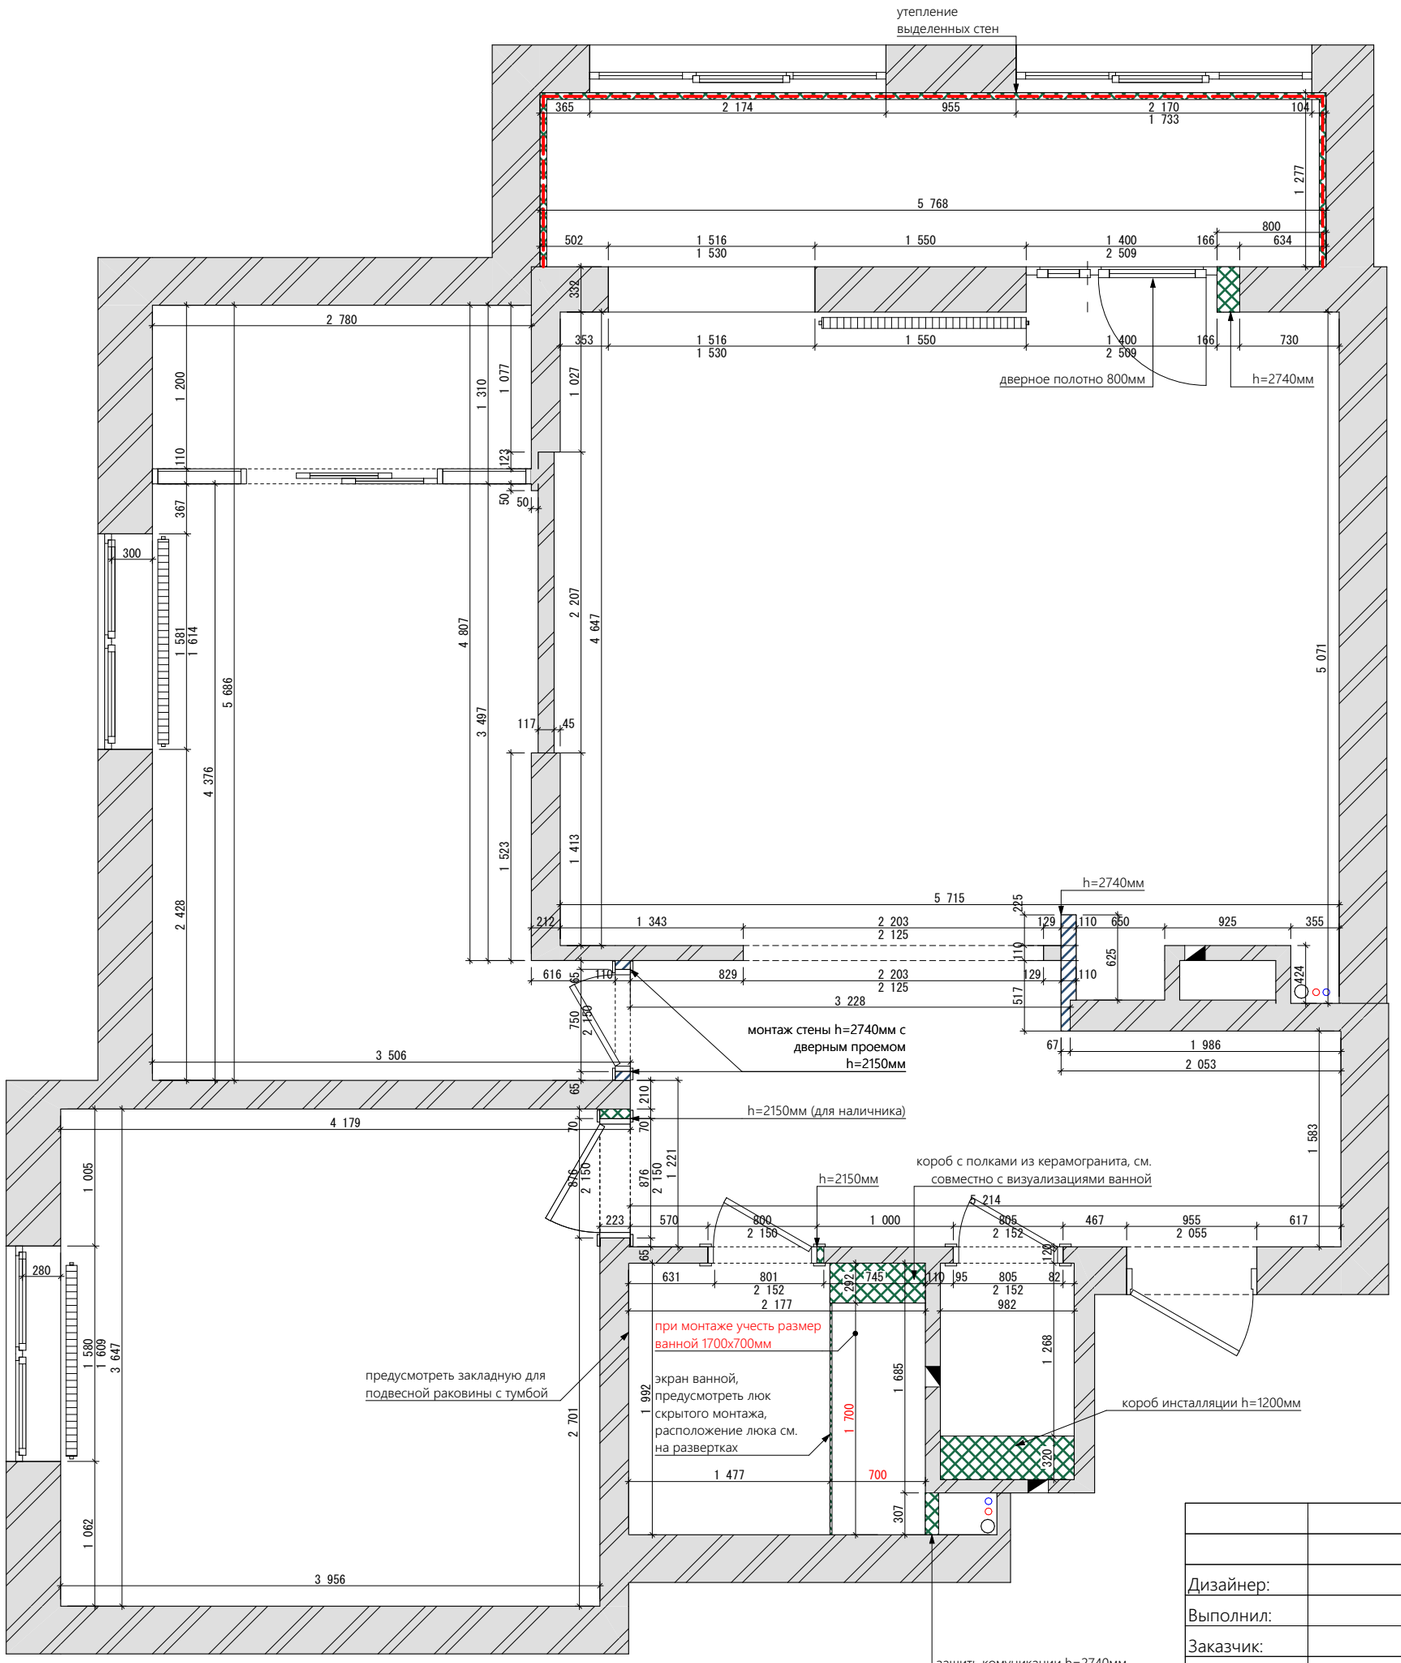

УСЛОВНЫЕ ОБОЗНАЧЕНИЯ

	существующие стены
	стены из ГКЛ
	стены из газоблока
	радиатор
	электрощиток
	проем для вентиляции
	водопровод канализация


ЭКСПЛИКАЦИЯ ПОМЕЩЕНИЙ

№	Наименование помещения	Площадь, м2	Площадь стен, м2
1	Прихожая	11,27	27,32
2	Санузел	1,56	12,31
3	Ванная комната	4,50	23,98
4	Детская	14,43	37,11
5	Спальня	16,01	43,20
6	Кухня-гостиная	27,45	49,81
7	Балкон	7,37	25,63
		82,59 м²	219,36 м²

ПРИМЕЧАНИЯ

1. Все размеры указаны в миллиметрах.
2. В конструкциях, скрывающих коммуникации предусмотреть лючки.
3. Вносимые изменения в существующую планировку квартиры (демонтаж, монтаж, перенос радиаторов, канализации и т.п.) требуют согласования в государственных и муниципальных учреждениях либо самостоятельно, либо через специализированные организации и являются ответственностью Заказчика.
4. Высоту и ширину межкомнатных проемов уточнить после окончательного согласованиямоделей дверей.
5. Площадь возводимых конструкций на чертеже и фактическая площадь могут отличаться по техническим причинам.
6. Краны перекрытия воды предусмотреть по месту с согласованием прораба и заказчика.
7. Вывести углы стен под 90 градусов в санузлах, в местах монтажа плитки на стенах (фартук, декоративные панели) а также на местах монтажа корпусной мебели, панельной отделки, декоративных ГКЛ конструкций.

		Подпись	Дата		Стадия	Лист
					ДП	6
Дизайнер:						
Выполнил:				План монтажа		
Заказчик:						

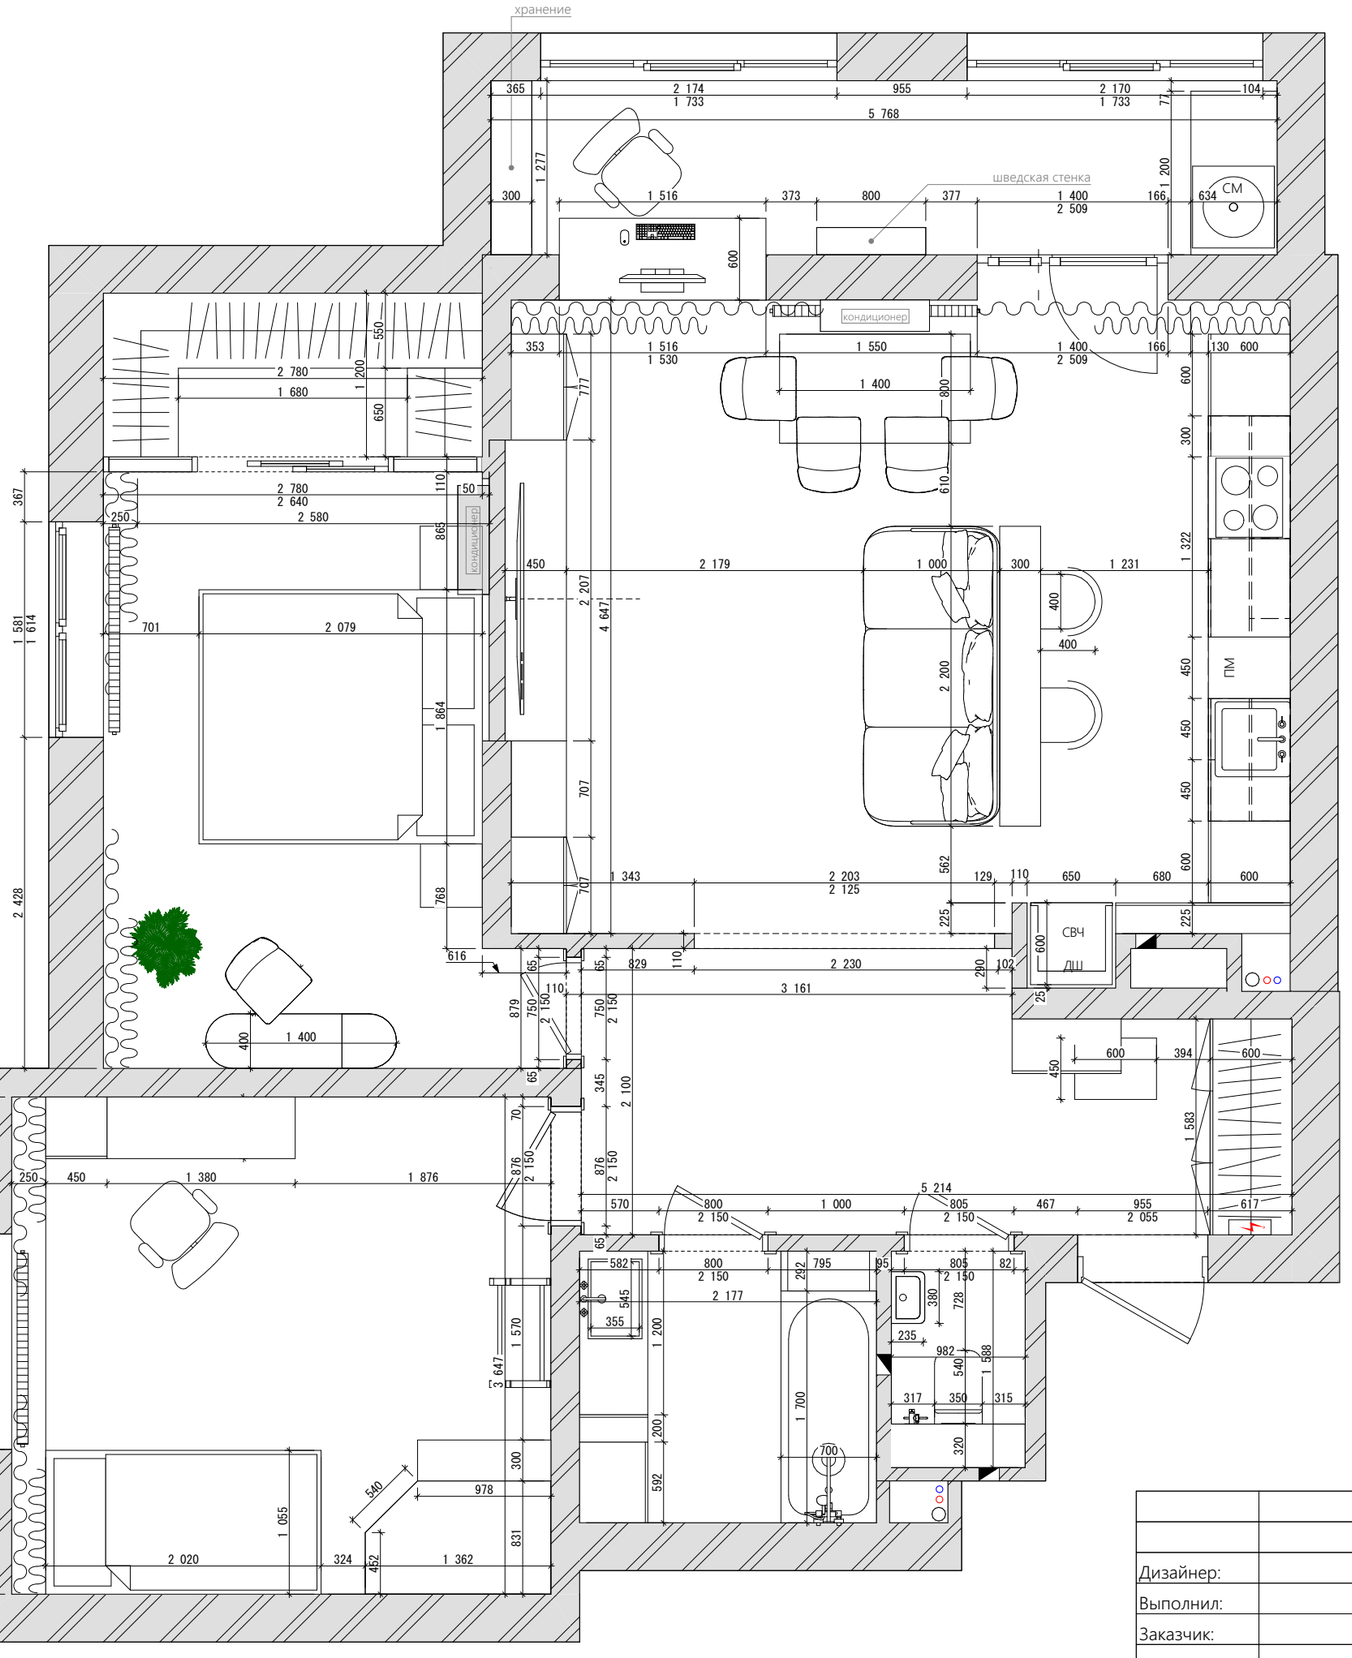

УСЛОВНЫЕ ОБОЗНАЧЕНИЯ

	существующие стены
	электрощиток
	водопровод канализация
	радиатор
	проем для вентиляции


ЭКСПЛИКАЦИЯ ПОМЕЩЕНИЙ

№	Наименование помещения	Площадь, м2
1	Прихожая	11,27
2	Санузел	1,56
3	Ванная комната	4,50
4	Детская	14,43
5	Спальня	16,01
6	Кухня-гостиная	27,45
7	Балкон	7,37
		82,59 м²

ПРИМЕЧАНИЯ:

1. Все размеры указаны в миллиметрах.
2. Лист смотреть совместно с 3D-визуализациями.
3. Размеры даны без учета отделочных слоев.
4. Мебель индивидуального изготовления заказывать только после фактических обмеров по месту от производителя.
5. Размеры мебели указаны только для предварительного расчета стоимости.
6. Сокращения, применяемые на чертехаж: - СМ - стиральная машина; - ПМ - посудомоечная машина; - ДШ - духовой шкаф; - СВЧ - микроволновая печь; - Х - холодильник;
7. В ванной комнате учтен слой для облицовки помещения 30мм(штукатурка 15мм+плитка 15мм) везде, кроме периметра ванной. По периметру ванной предусмотрен слой 15мм, с учетом монтажа ванной после оштукатуривания и гидроизоляции, но перед началом плиточных работ.

		Подпись	Дата		Стадия	Лист
					ДП	7
Дизайнер:						
Выполнил:				План расстановки мебели и оборудования		
Заказчик:						

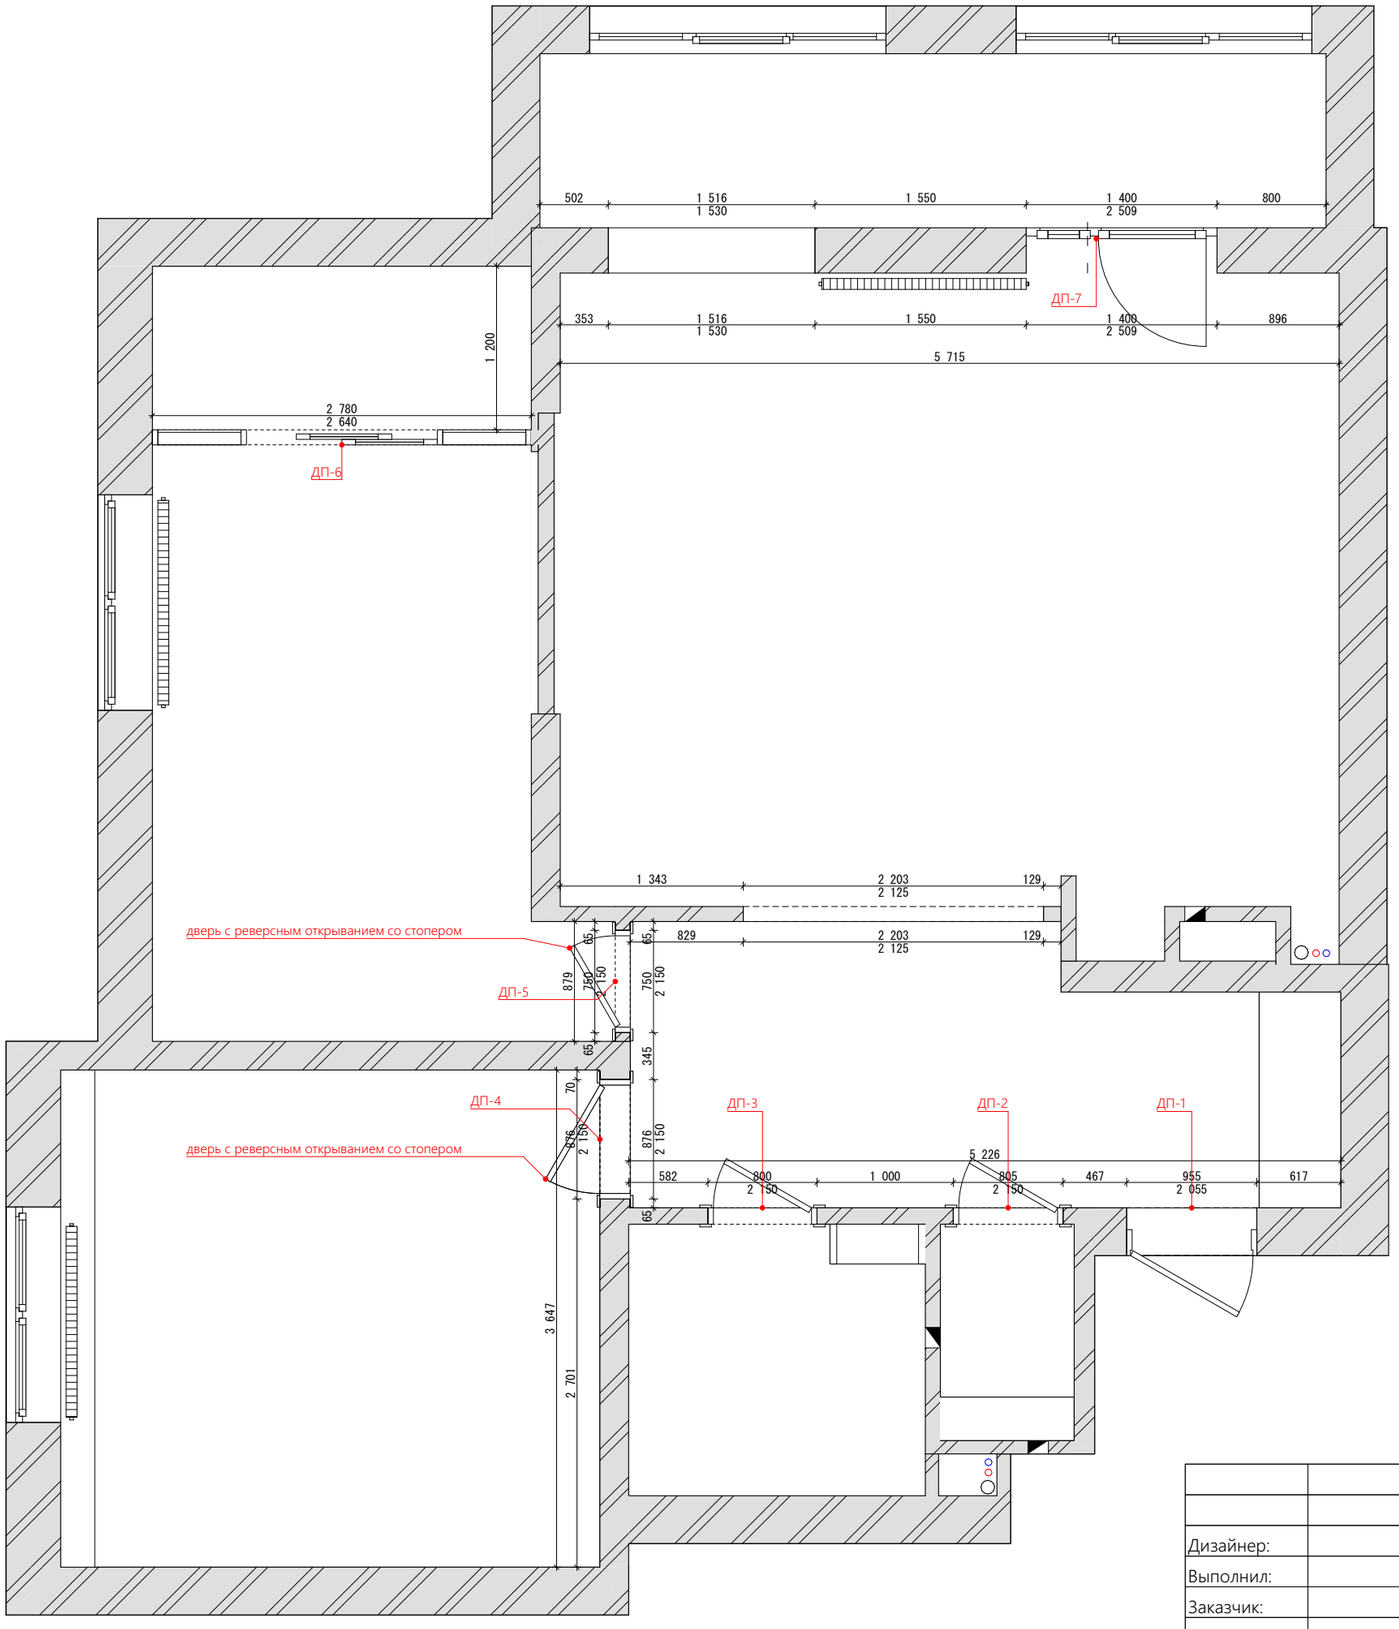


ВЕДОМОСТЬ ДВЕРНЫХ ПОЛОТЕН

ДП-01	дверное плотно входной двери 900х2000мм
ДП-02	дверное плотно межкомнатной двери 700х2000мм
ДП-03	дверное плотно межкомнатной двери 700х2000мм
ДП-04	дверное плотно межкомнатной двери 800х2000мм
ДП-05	дверное плотно межкомнатной двери 650х2000мм
ДП-06	стекляная перегородка из 4 полотен. два статичных - каждое по 690мм в ширину, два раздвижных - каждое по 700мм в ширину
ДП-07	балконный блок, размер дверного полотна ширину 800мм, остальные размеры согласовать с заказчиком

ПРИМЕЧАНИЯ:

1. Все размеры указаны в миллиметрах.
2. Размеры даны без учета отделочных слоев.
3. Ширину проёмов проверить по месту, монтаж выполнить в соответствии с требованиями по установке скрытых дверных коробок.
4. Высоту и ширину межкомнатных проемов уточнить после окончательного согласования моделей дверей.
5. На плане обозначены размеры дверного проема! В условных обозначениях - ориентировочный размер полотна!
6. Перед заказом дверей произвести замер по месту.

		Подпись	Дата		Стадия	Лист
					ДП	8
Дизайнер:						
Выполнил:				План формирования дверных проемов		
Заказчик:						

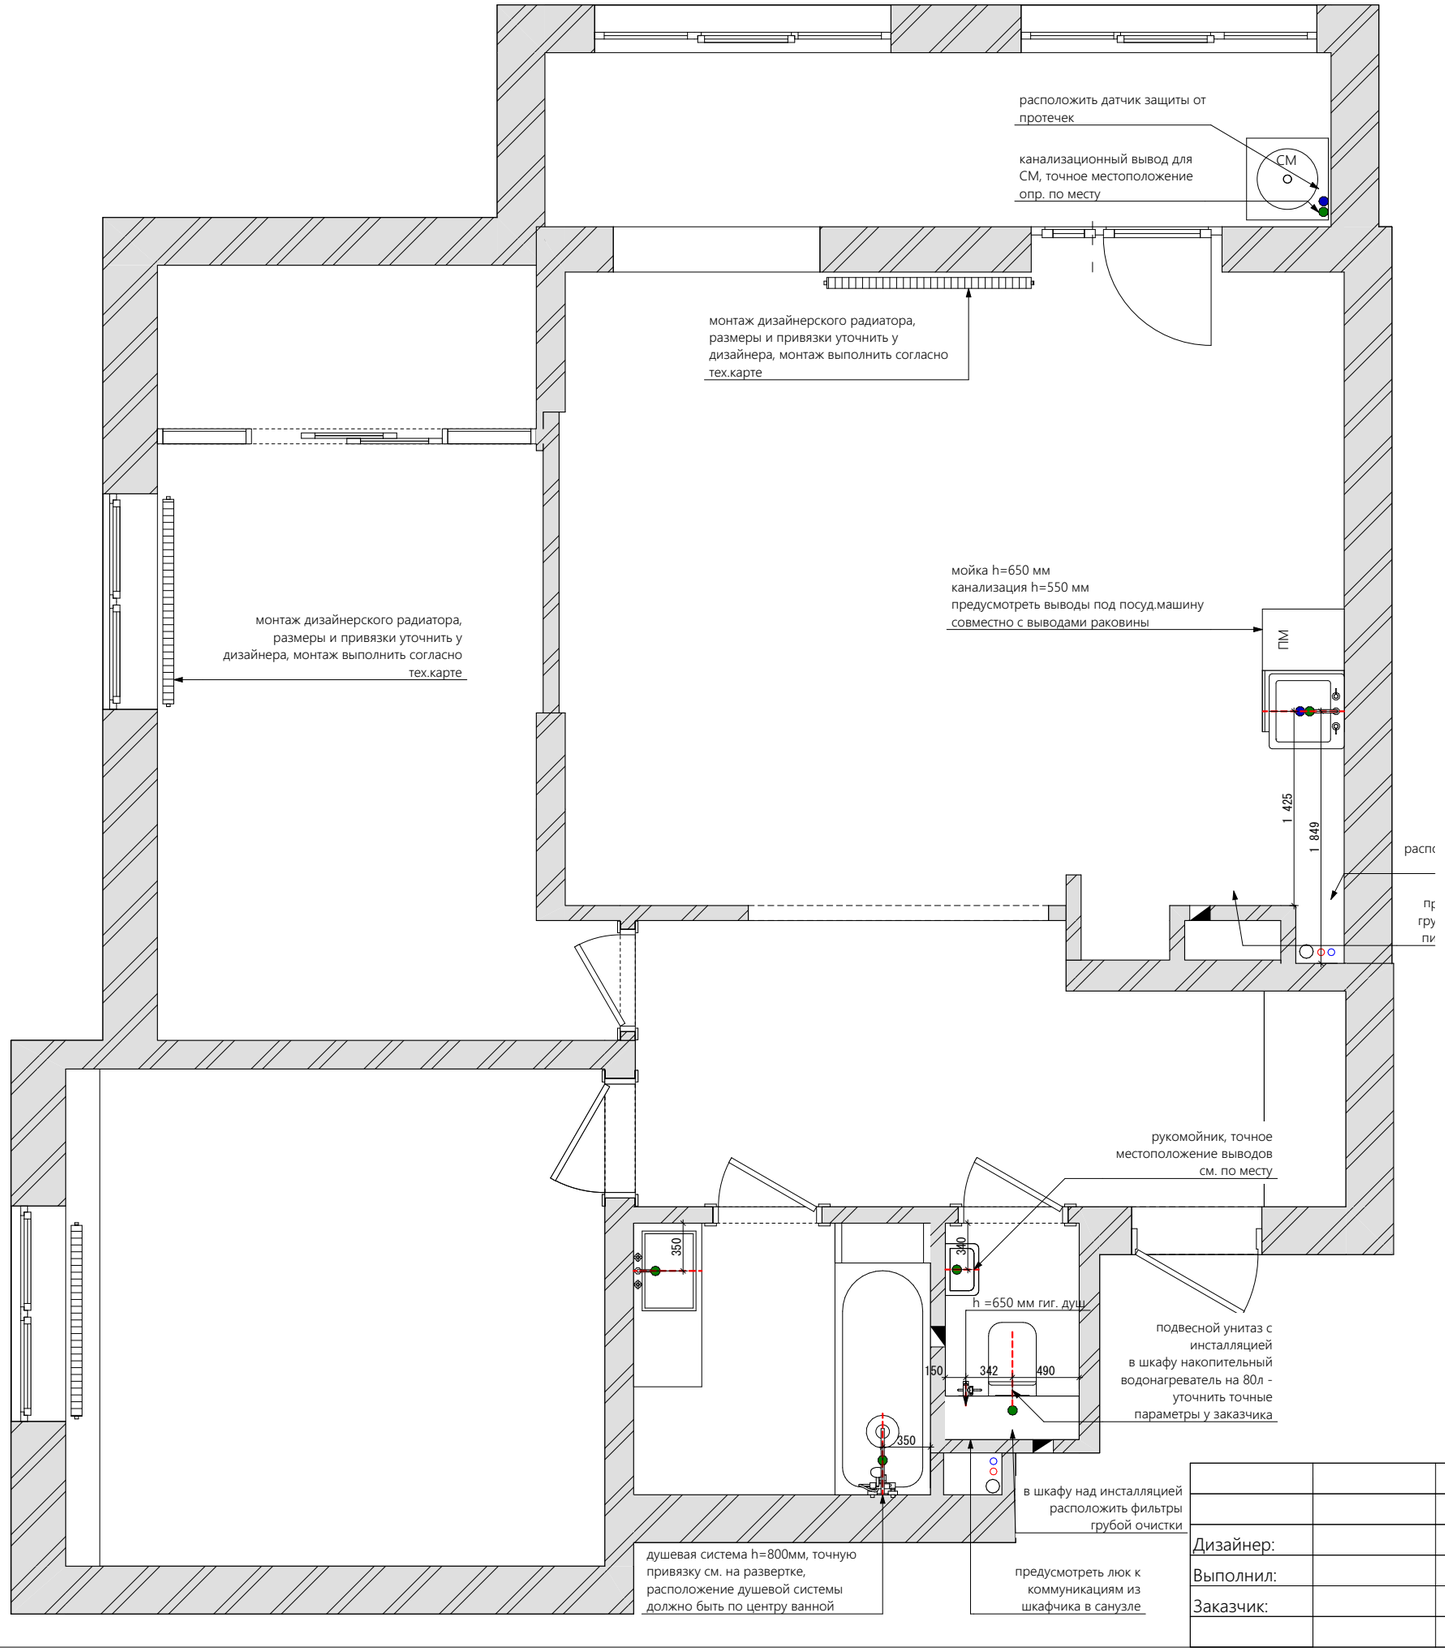

УСЛОВНЫЕ ОБОЗНАЧЕНИЯ

	существующие стены
	канализационный вывод
	датчик защиты от протечек
	электрощиток
	водопровод канализация
	радиатор
	проем для вентиляции

ПРИМЕЧАНИЯ

1. Все размеры указаны в миллиметрах.
2. Лист смотреть совместно развертками стен.
3. Размеры даны без учета отделочных слоев.
4. Коммуникации штробим(уточнить по месту).
5. Привязка по оси сантехнического оборудования.
6. Установка сантехнического оборудования согласно тех. картам.
7. Выводы сантехники в кухне уточнить после окончательного согласования проекта кухни.
8. Все высоты и привязки по стенам уточнить по месту и выполнить совместно с техническими картами, выбранного сантехнического оборудования.


		Подпись	Дата
Дизайнер:			
Выполнил:			
Заказчик:			

Общий план расстановки сантехнических приборов


Стадия	Лист
ДП	9

ДИЗАЙН & Co.


Радиатор трубчатый 7 секций (спальня) Piatto 30x60 Z

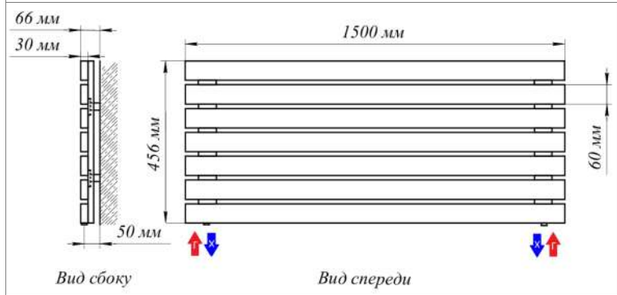


Радиатор трубчатый 10 секций (гостиная) Piatto 30x60 Z

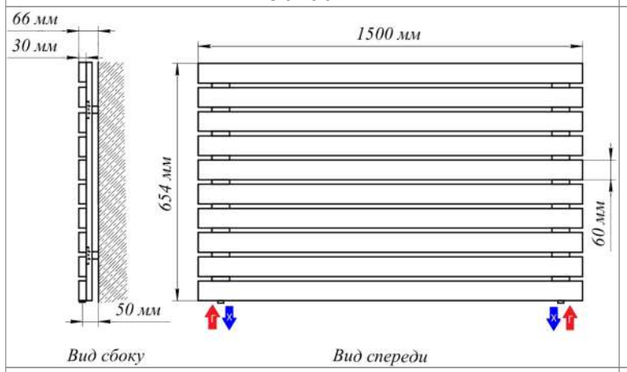


Смеситель для раковины оружейная сталь SEEME AVS

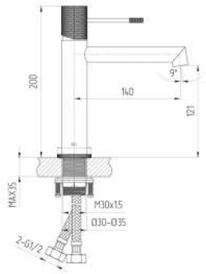


Встраиваемый смеситель с гигиеническим душем оружейная сталь SEEME AVS

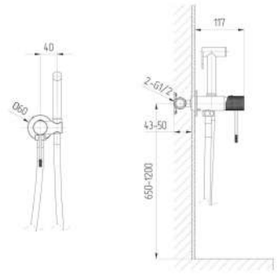


Душевая система ТЕРМОСТАТ для ванны оружейная сталь SEEME AVS

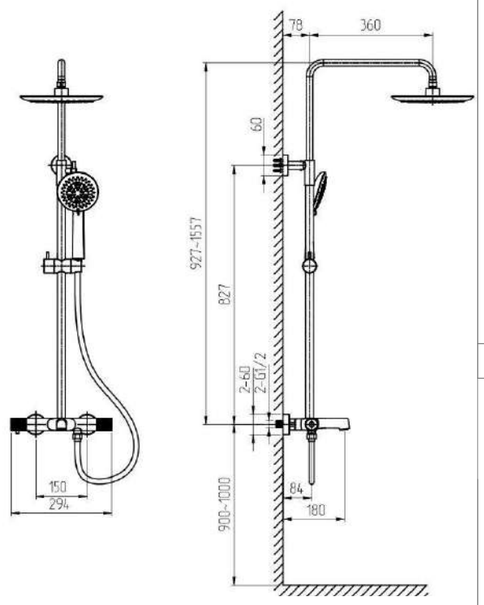


Система инсталляции с отверстием для дезинфицирующих таблеток AVS

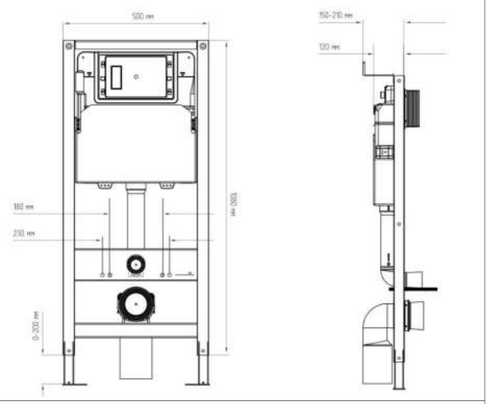


Раковина 400*220 Como CERSANIT - 1 шт

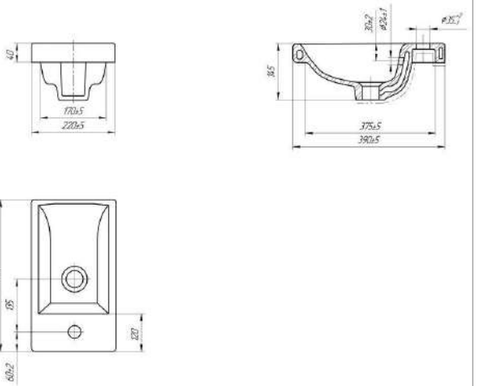


KASANDRA Ванна акриловая 170*70*45 без КС, без ф/п, без с/п бел, подходит КС VPK17070 Vagnerplast

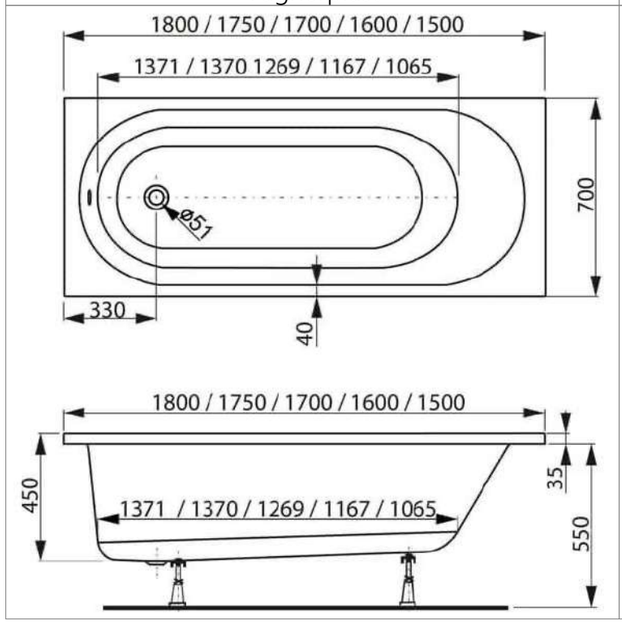


Раковина 1200*480*175 правая Прима AVS

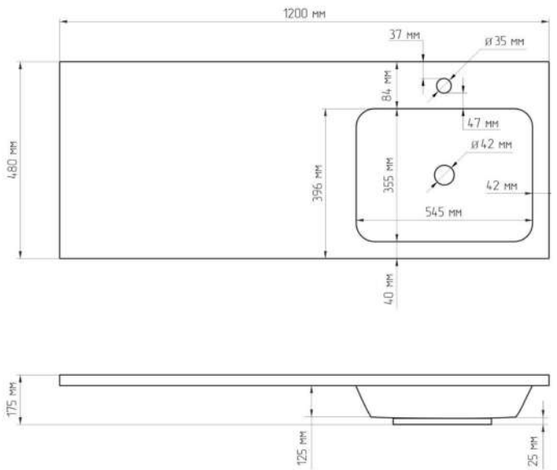

Клавиша смыва, овальн.кнопки, оружейная сталь AVS

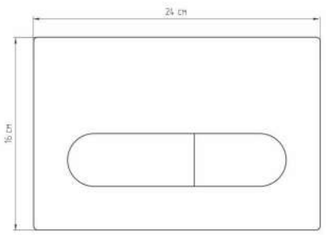



Унитаз подвес БЕЗОБОД со смывом Торнадо2 + сид-е, 54см глянцевый белый ЛЕММА AVS

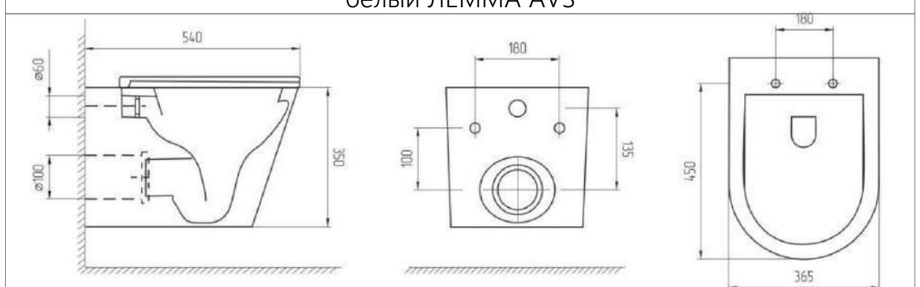


		Подпись	Дата		Стадия	Лист
					ДП	10
Дизайнер:						
Выполнил:				План с техническими картами сантехнических приборов		
Заказчик:						


Развертка стен ванной комнаты. Привязка сантехники, раскладка плитки

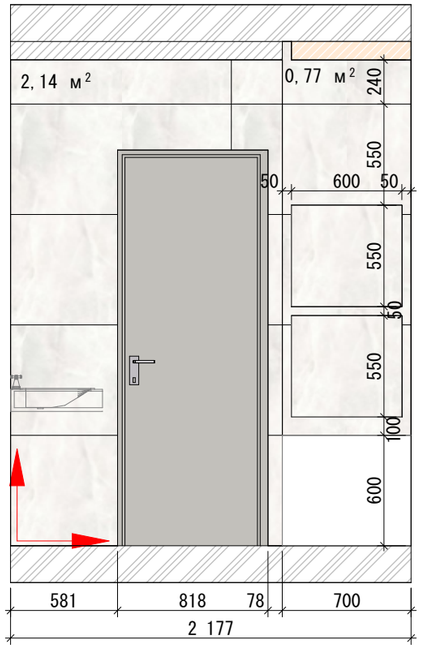

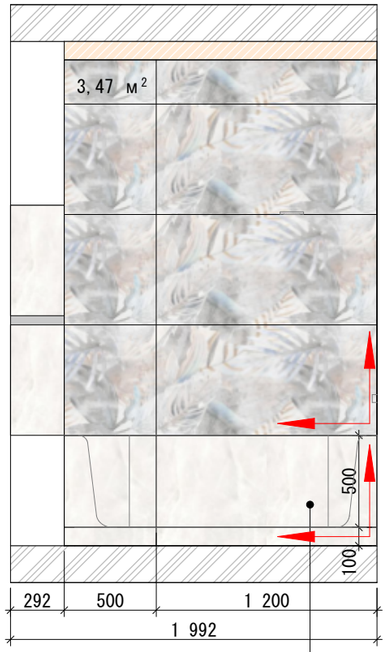


экран ванной под облицовку плиткой
с подсвечиваемым цоколем
предусмотреть люк скрытого монтажа
в экране ванной - см.по месту

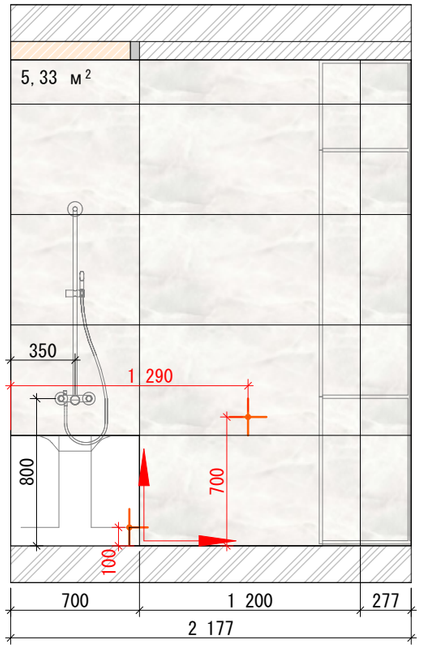

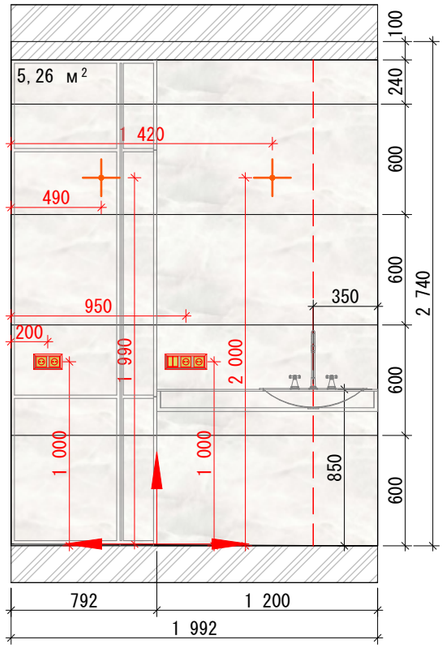

УСЛОВНЫЕ ОБОЗНАЧЕНИЯ:

	Керамогранит bahamas floristry light d120241g матовый гранить S=3,5м² СТЕНЫ без запаса
	Керамогранит salt white d120244l лаппатированный карвинг S=15,7 м² без запаса

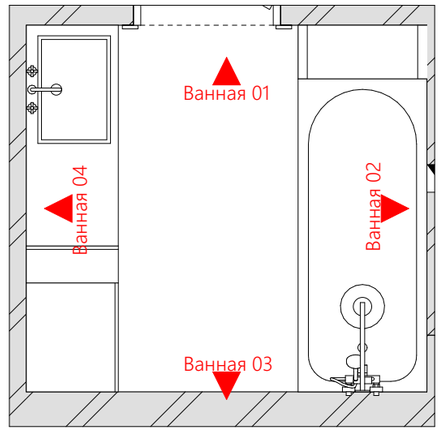



ПРИМЕЧАНИЯ:

1. Все размеры указаны в миллиметрах.
2. Размеры даны без учета отделочных слоев.
3. Углы плитки запиливать под 45 градусов.
4. Шов минимальный (реттифицированный керамогранит).
5. Каждый вид керамогранита затирается своим цветом затирки - уточнить у дизайнера.
6. Привязка сантехнического оборудования указана на развертках.
7. Установка сантехнического оборудования согласно тех. картам, см. лист 10.
8. Закупка сантехнического оборудования осуществляется только после возведения перегородок, оштукатуривания стен, укладки плитки и последующей проверки размеров.
9. Привязка электрики возле двери дана от дверного проема, а не от полотна!
10. Лист смотреть совместно с 3D-визуализациями.

		Подпись	Дата		Стадия	Лист
					ДП	11
Дизайнер:						
Выполнил:				Развертка стен ванной комнаты. Привязка сантехники, раскладка плитки		
Заказчик:						

Развертка стен санузла. Привязка сантехники, раскладка плитки

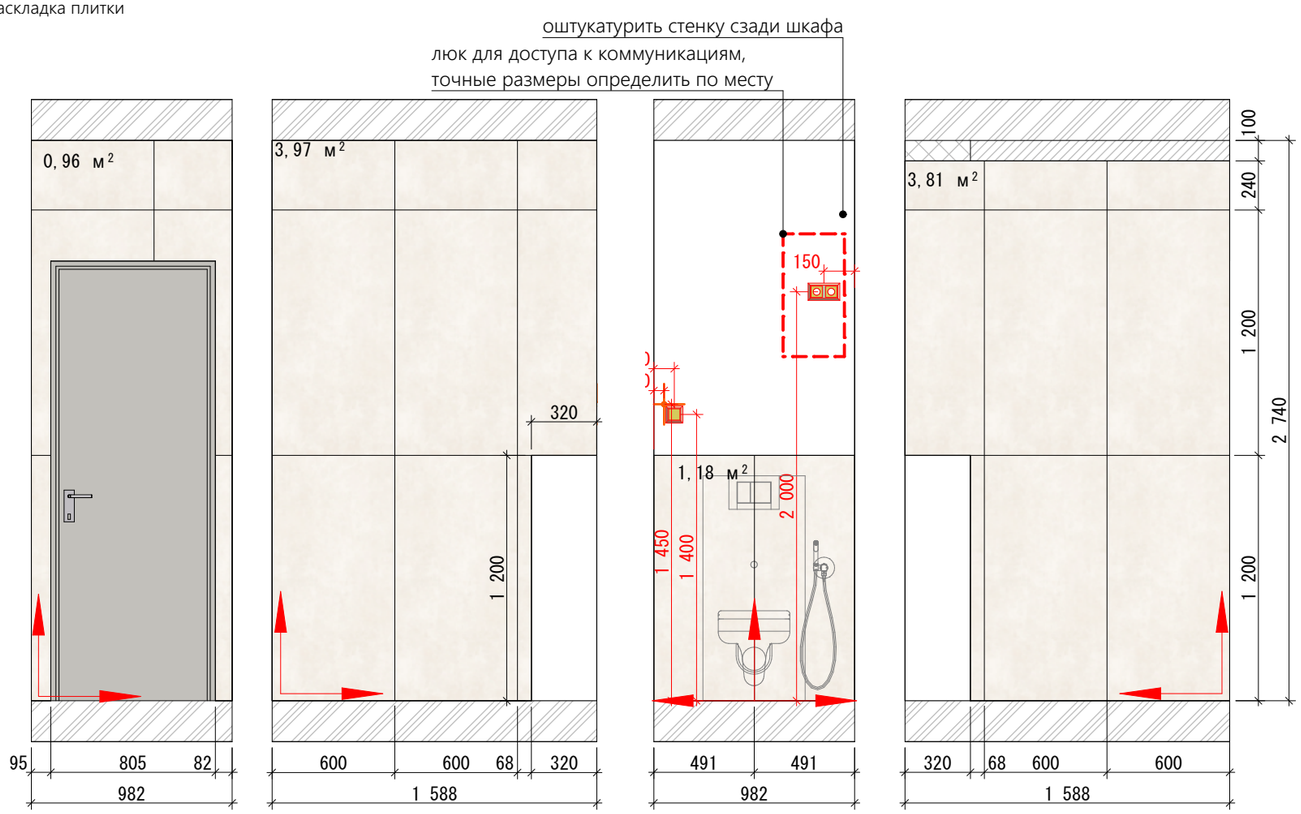

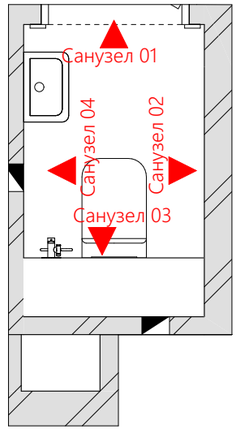

Санузел 01 1:30 Санузел 02 1:30 Санузел 03 1:30 Санузел 04 1:30


УСЛОВНЫЕ ОБОЗНАЧЕНИЯ:

	Керамогранит GFU60120BTP04R Beton Pro матовый 600x1200x8.5 S=10,1 м^2 без запаса

ПРИМЕЧАНИЯ:

1. Все размеры указаны в миллиметрах.
2. Размеры даны без учета отделочных слоев.
3. Углы плитки запиливать под 45 градусов.
4. Шов минимальный (реттифицированный керамогранит).
5. Каждый вид керамогранита затирается своим цветом затирки - уточнить у дизайнера.
6. Привязка сантехнического оборудования указана на развертках.
7. Установка сантехнического оборудования согласно тех. картам, см. лист 10.
8. Закупка сантехнического оборудования осуществляется только после возведения перегородок, оштукатуривания стен, укладки плитки и последующей проверки размеров.
9. Привязка электрики возле двери дана от дверного проема, а не от полотна!
10. Лист смотреть совместно с 3D-визуализациями.

		Подпись	Дата		Стадия	Лист
					ДП	12
Дизайнер:						
Выполнил:				Развертка стен санузла. Привязка сантехники, раскладка плитки		
Заказчик:						

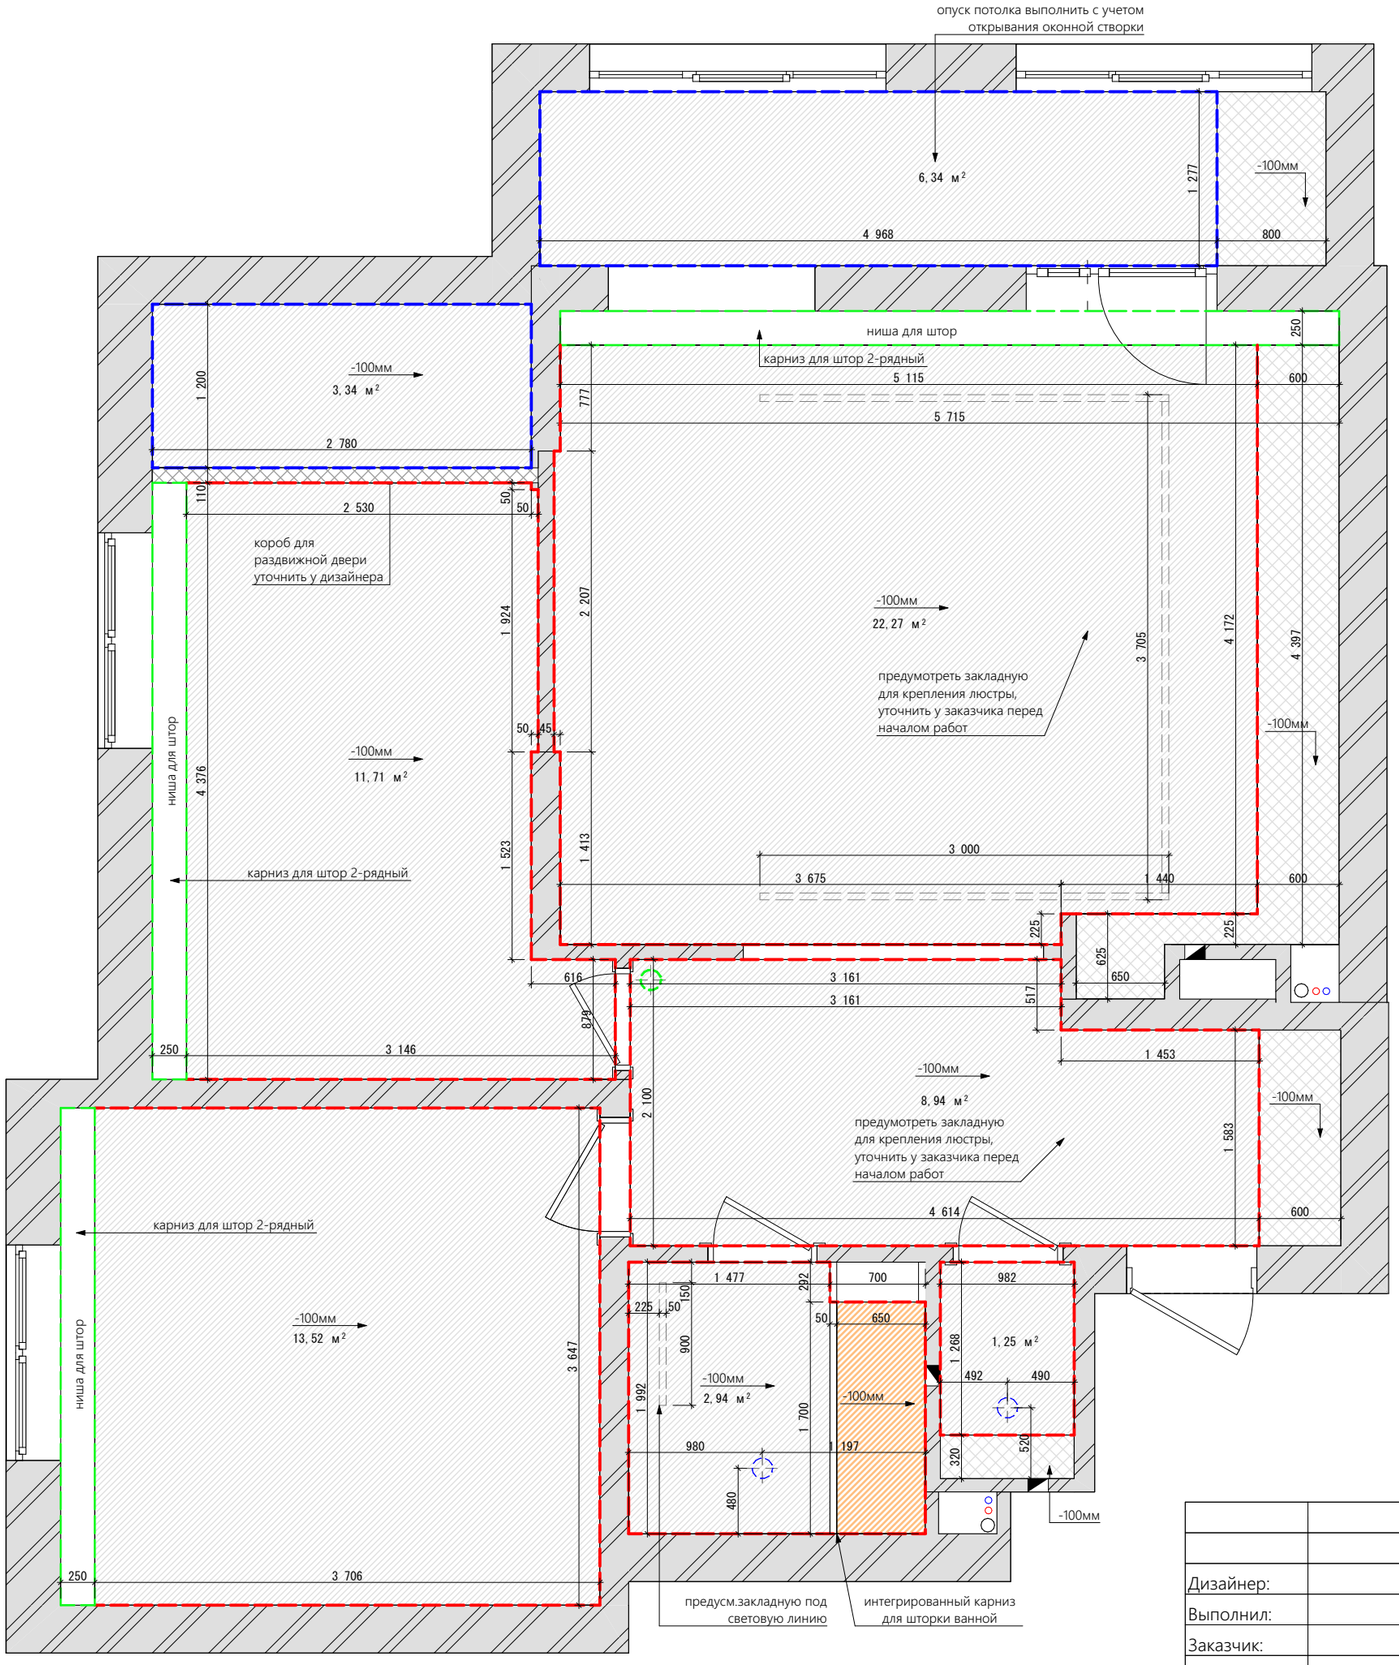


УСЛОВНЫЕ ОБОЗНАЧЕНИЯ

	натяжной потолок, цвет белый матовый = 30,53 м²
	ГКЛ потолок выкрасить в белый матовый
	световой натяжной потолок = 1,21 м²
	световая линия
	теневой профиль д/натяж. потолка=30,43 пог.м
	резинка для натяжного потолка = 21 пог.м.
	потолочный карниз для штор 2-рядный = 14,1 пог.м.
	принудительная вытяжка потолочная = 2шт
	закладная под камеру

ПРИМЕЧАНИЯ

1. Все размеры указаны в миллиметрах.
2. Лист смотреть совместно с развертками стен.
3. Лист смотреть совместно с 3D-визуализациями.
4. Размеры даны без учета отделочных слоев.
5. Перед монтажом потолков уточнить монтажную глубину выбранных светильников.
6. Монтаж теневого профиля - к ГКЛ коробам. Опуск ГКЛ коробов равен опуску натяжных полотен!!!
7. При необходимости дополнительного разделения натяжного потолка стыковочным профилем - уточнить у дизайнера его местоположение!
8. Местоположение интегрированной вентиляции в ванной и его размеры уточнить у производителя работ, согласовать с дизайнером и заказчиком. Монтаж выполнить согласно техкарте. Опуск потолка должен соответствовать техническим рекомендациям по установке щелевого диффузора.

		Подпись	Дата		Стадия	Лист
					ДП	13
Дизайнер:						
Выполнил:				План потолков		
Заказчик:						

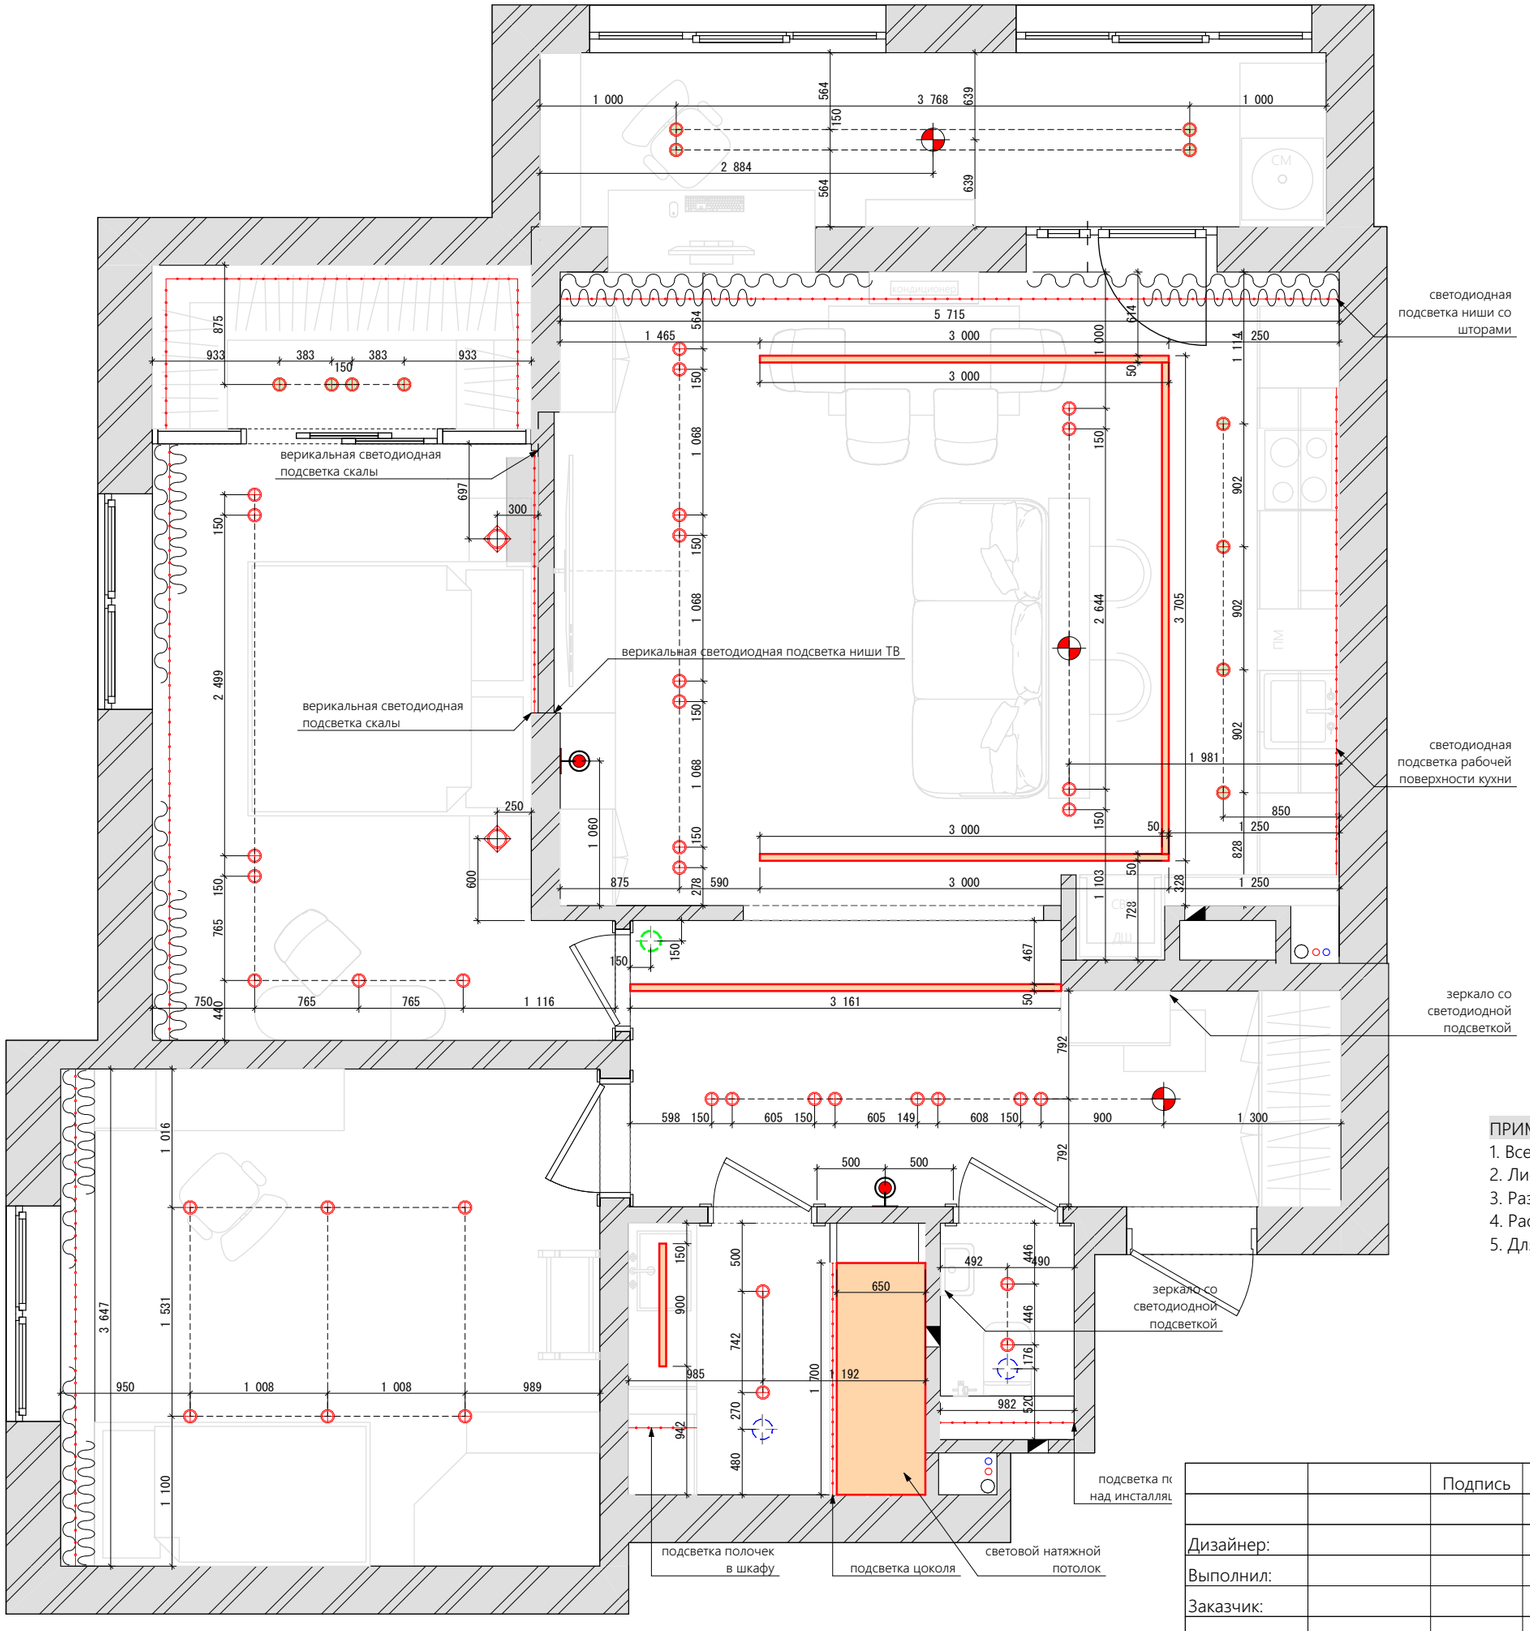


УСЛОВНЫЕ ОБОЗНАЧЕНИЯ		
Вид на плане	Наименование	Кол-во
	Бра	2
	Накладной Точечный Светильник	41 шт
	Люстра	3 шт
	Световая линия	13,5 пог.м.
	Светодиодная подсветка	

ПРИМЕЧАНИЯ:

1. Все размеры указаны в миллиметрах.
2. Лист смотреть совместно с развертками стен.
3. Размеры даны без учета отделочных работ.
4. Расположение осветительного оборудования указано относительно центра светильника.
5. Для электровыводов дать запас.

		Подпись	Дата		Стадия	Лист
					ДП	14
Дизайнер:				План расстановки осветительного оборудования		
Выполнил:						
Заказчик:						

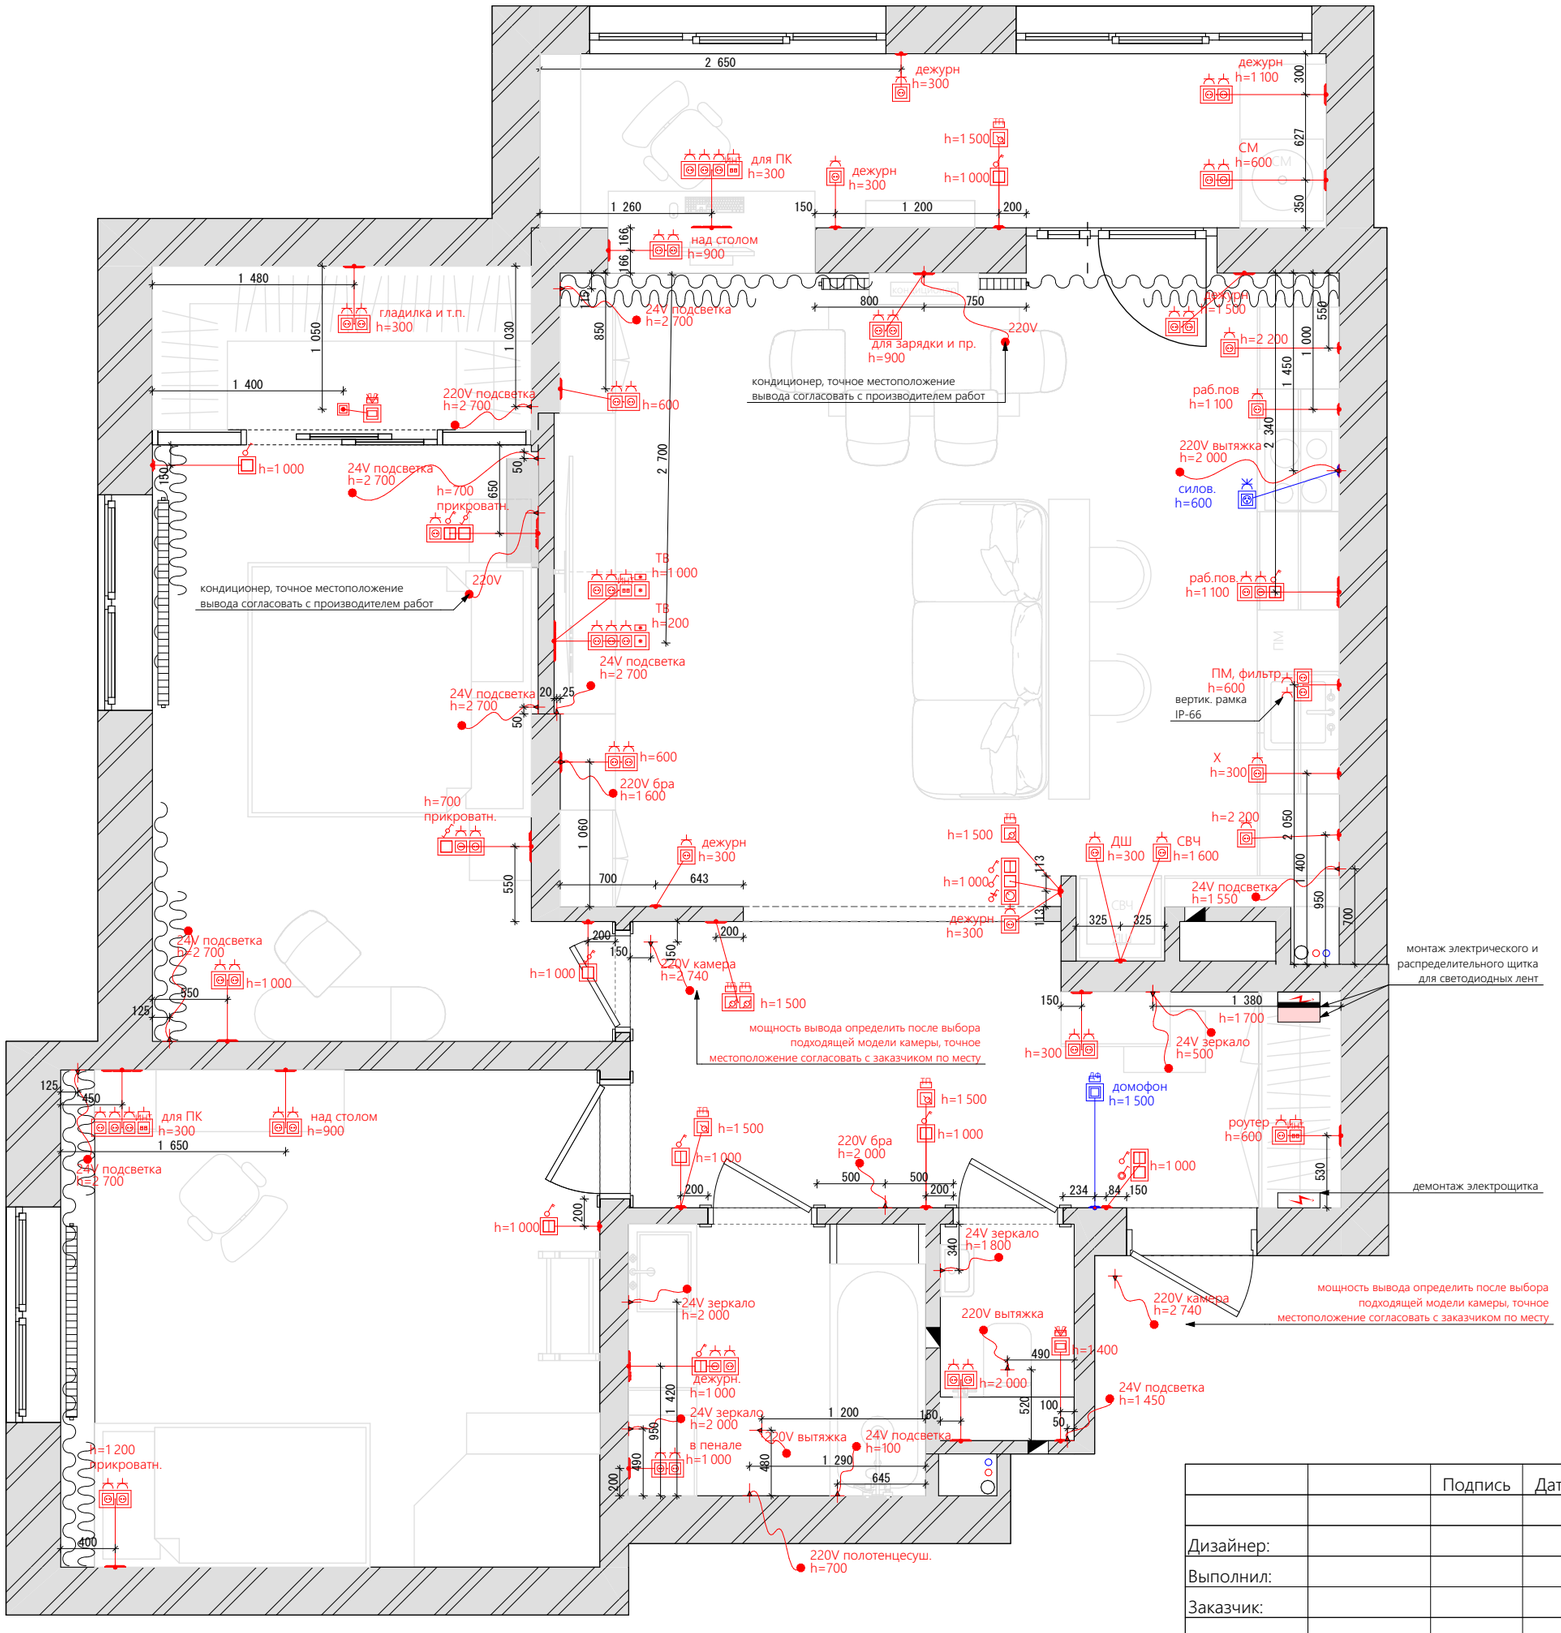


УСЛОВНЫЕ ОБОЗНАЧЕНИЯ		
Вид на плане	Наименование	Кол-во
	Кабельканал	2
	Выключатель 1 клавишный	2
	Выключатель 1 клавишный	2
	Выключатель 1 клавишный -"МАСТЕР"	1
	Выключатель 2 клавишный	9
	Выключатель 2 клавишный	1
	Датчик движения	2
	Домофон	1
	Розетка 220V	59
	Силовой вывод	1
	Розетка сетевая	4
	Светорегулятор (диммер) 220V 10А-50А	1
	Терморегулятор теплого пола	6

ВЫВОДЫ		
Вид на плане	Наименование	Кол-во
	Вывод ЭЛ 220V	11
	Вывод ЭЛ 24V	14

ПРИМЕЧАНИЯ:

1. Все размеры указаны в миллиметрах.
2. Лист смотреть совместно с развертками стен.
3. Размеры даны без учета отделочных слоев.
4. Расположение розеток и выводов указано относительно центра розетки или группы розеток.
5. Все розетки, необозначенные отметкой высоты, устанавливаются на высоту 300 мм от уровня пола, выключатели 1000 мм.
6. Точное расположение розеток и выводов для кухонной техники уточнить при заказе кухни.
7. Выводы под сплит-систему даны к нижней точке корпуса со стороны стены, согласно купленной модели.
8. Выводы в зонах TV требуют согласования с учетом выбранного оборудования.
9. Дать запас электр.выводам не менее 500мм.


		Подпись	Дата		Стадия	Лист
					ДП	15
Дизайнер:						
Выполнил:				План расположения розеток и выключателей		
Заказчик:						

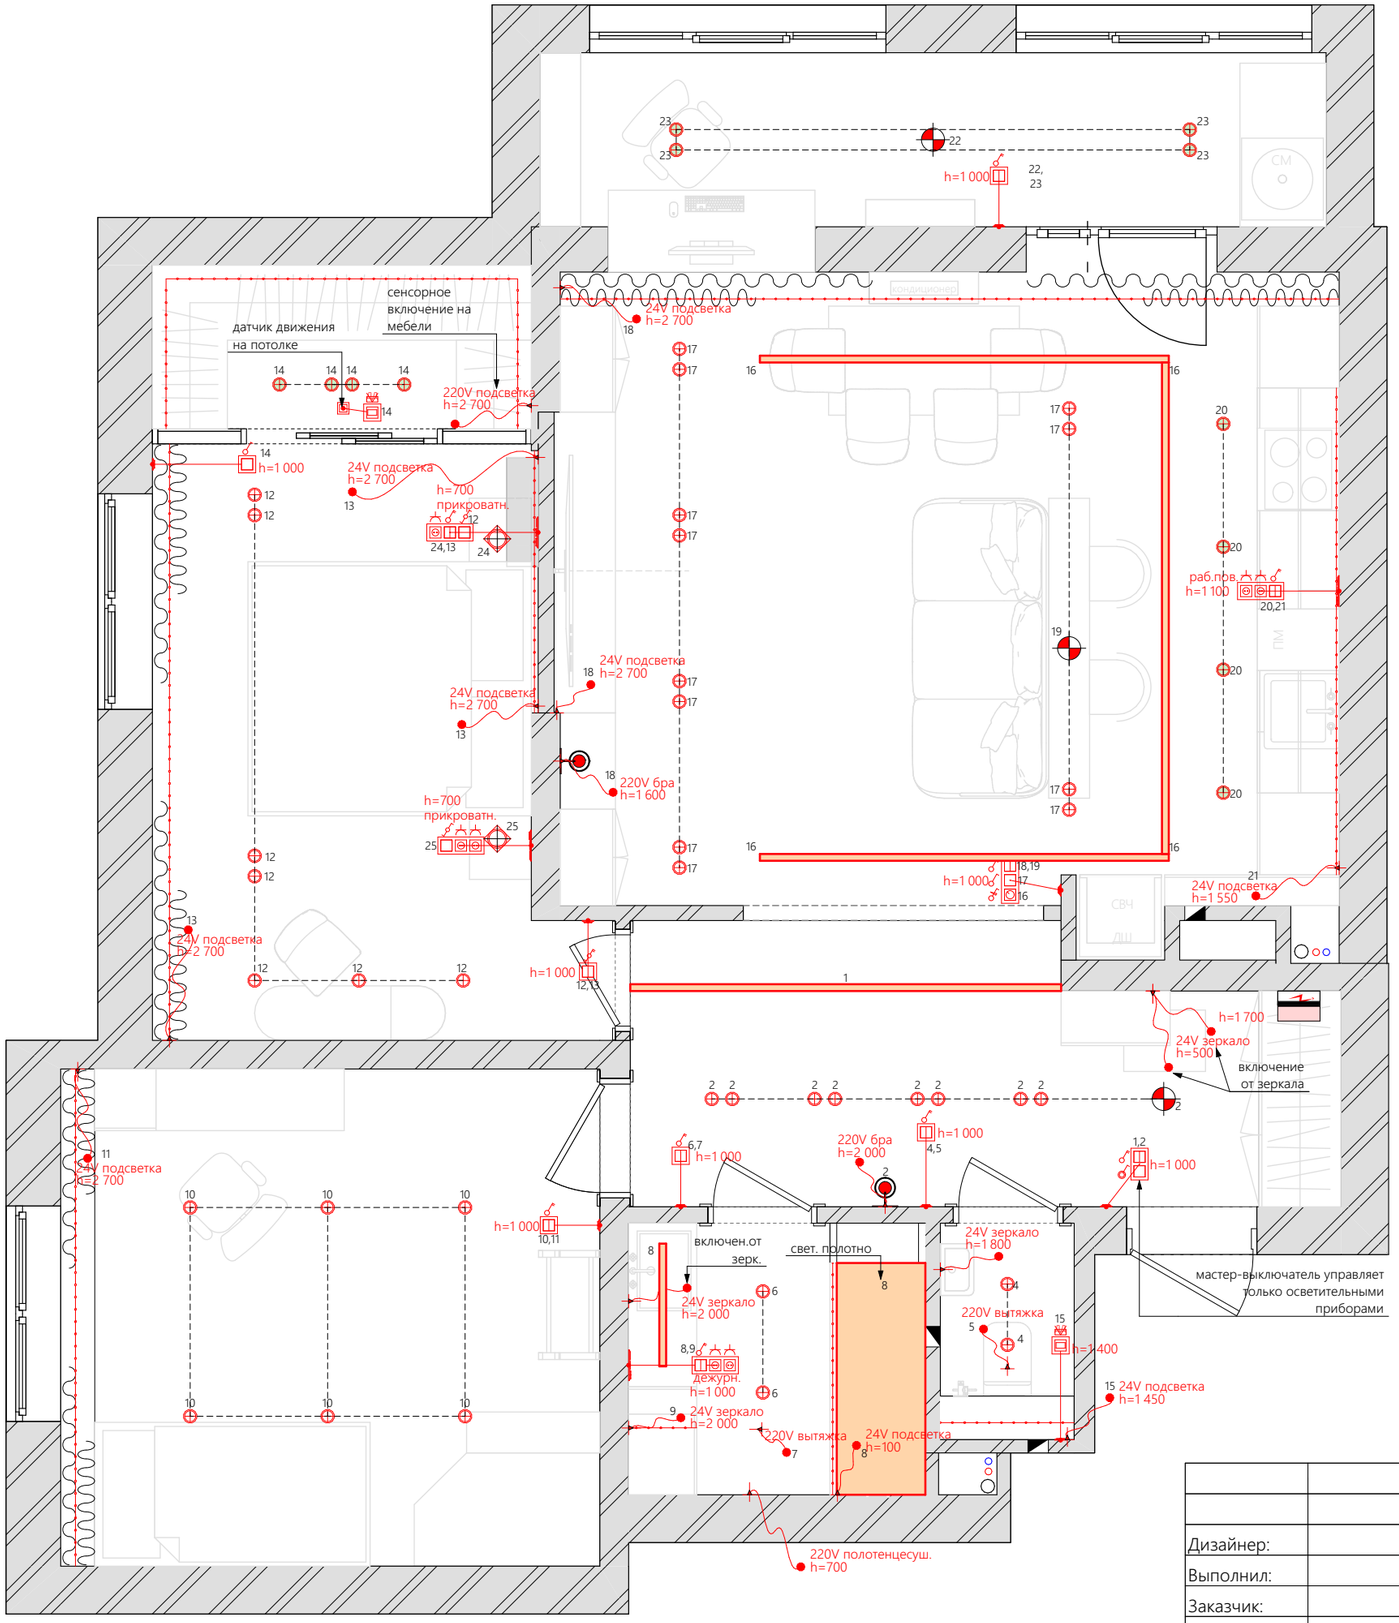

ПРИМЕЧАНИЯ:

1. Все размеры указаны в миллиметрах.
2. Лист смотреть совместно с развертками стен.
3. Размеры даны без учета отделочных работ.
4. Расположение осветительного оборудования указано относительно центра светильника.
5. Для электровыводов дать запас.
6. Точное расположение выводов электрики и сантехники уточнить после окончательного
согласования проекта кухни.
7. Лист смотреть совместно с планом расположения розеток и выключателей.

		Подпись	Дата		Стадия	Лист
					ДП	16
Дизайнер:				План управления осветительным оборудованием		
Выполнил:						
Заказчик:						

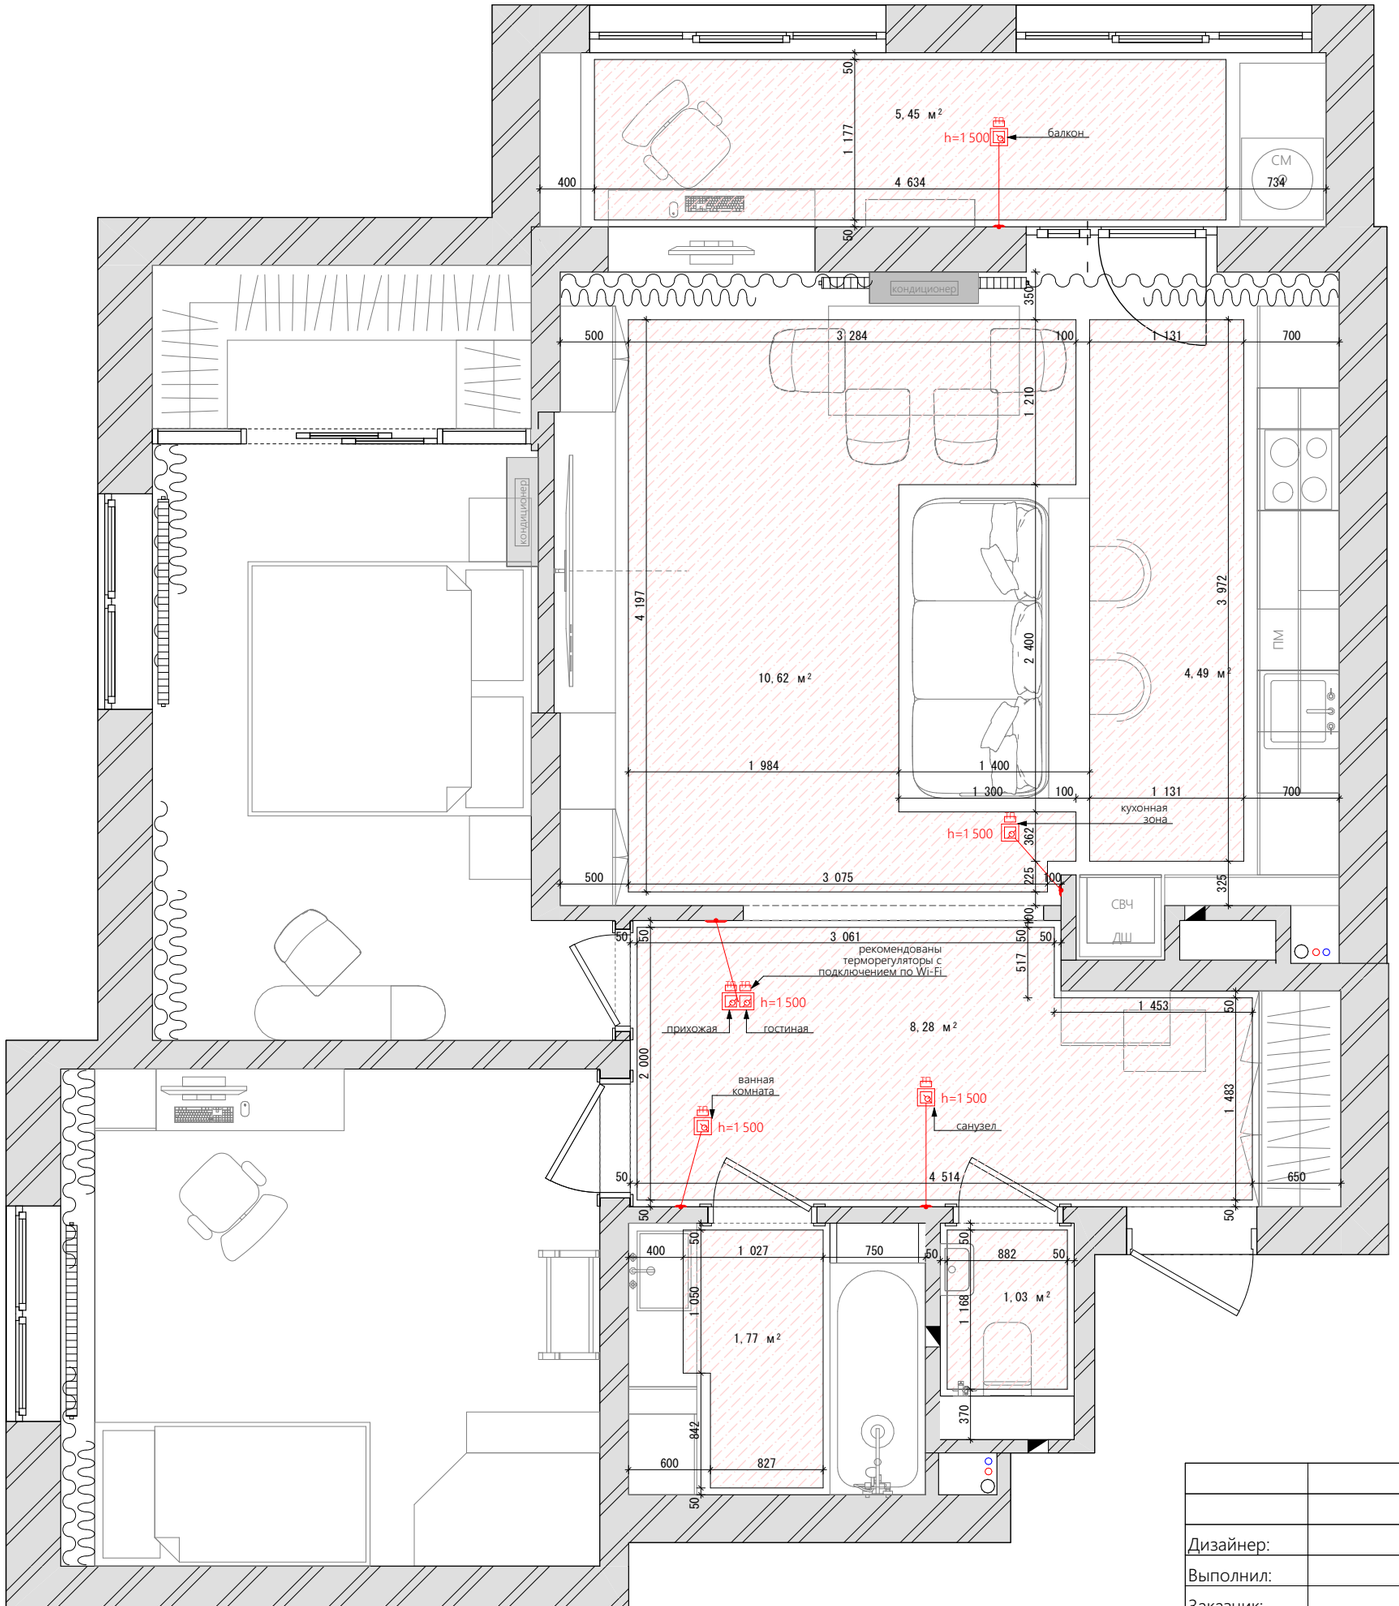


УСЛОВНЫЕ ОБОЗНАЧЕНИЯ

теплый электрический пол = 31,72 м²

ПРИМЕЧАНИЯ:

1. Все размеры указаны в миллиметрах.
2. При приобретении напольных покрытий и систем теплого пола уточнить у поставщиков их совместимость.
3. Теплый пол монтируется с отступом от мебели 100 мм.

		Подпись	Дата		Стадия	Лист
					ДП	17
Дизайнер:						
Выполнил:				План привязки теплого пола		
Заказчик:						

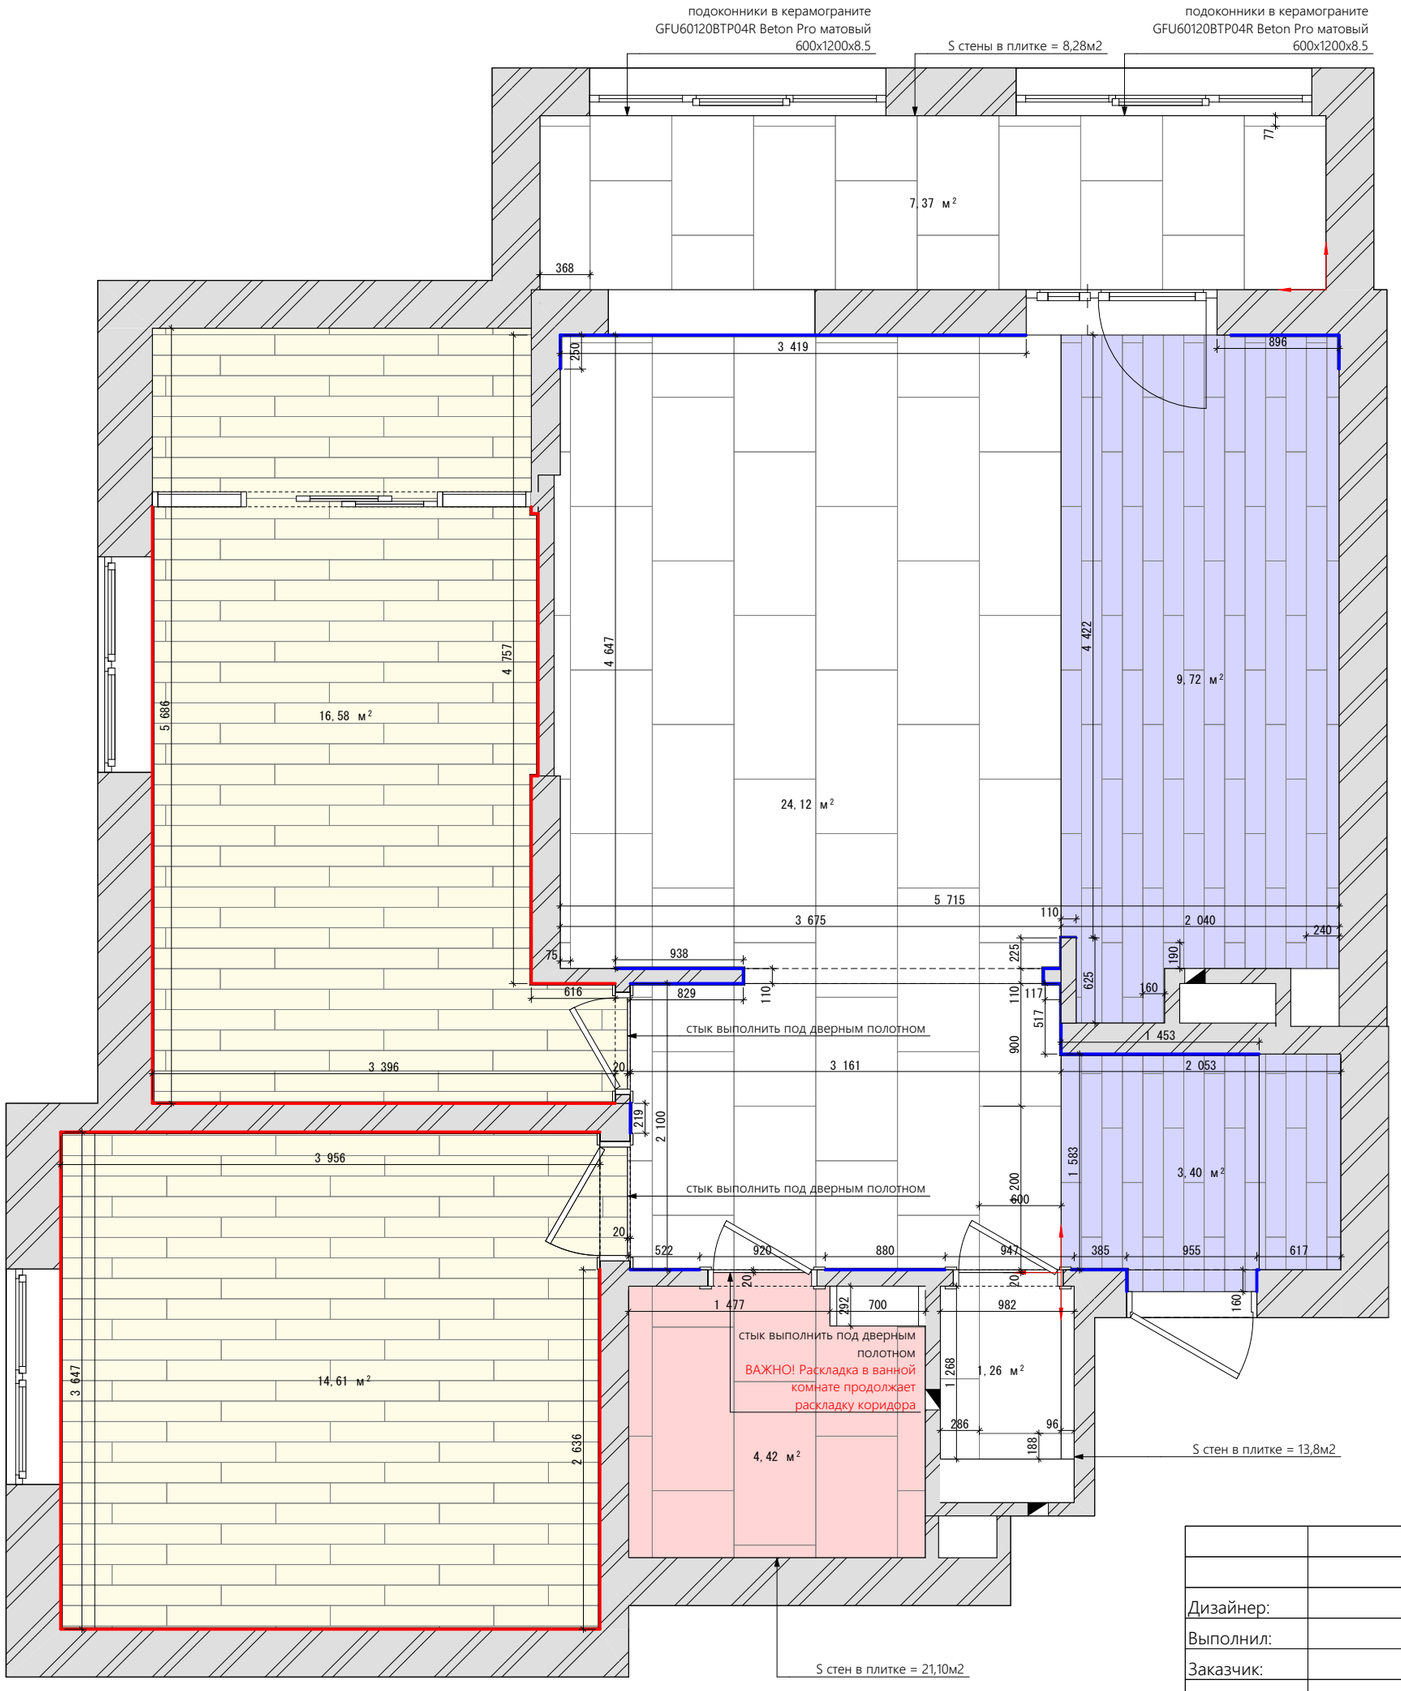

УСЛОВНЫЕ ОБОЗНАЧЕНИЯ:


Вид на плане	Текстура материала	Наименование	Кол-во
		Кермогранит 60120PEF01M Perfect Marble мат.карвинг 600x1200мм	S=32,2м² без запаса
		Кермогранит Salt White D120244L лапатированный карвинг 600x1200мм	S=4,42м² без запаса
		Керамогранит Naturalwood Nut GP20120NAT11 матовый 200x1200	S=13,12м² без запаса
		Ламинат дуб светлый - толщина 10мм	S=31,2м² без запаса
	МДФ плинтус в цвет дверей		29 пог.м. без запаса
	Плинтус 90мм дюрополимер под покраску		12м² без запаса
	Начало раскладки плитки		

ПРИМЕЧАНИЯ:


1. Все размеры указаны в миллиметрах.
2. Лист смотреть совместно с развертками стен.
3. Размеры даны без учета отделочных слоев.
4. Все площади посчитаны без запаса.
5. Направление укладки пола и все размеры уточняются после окончания общестроительных работ.
6. Границы технологического разрыва уточнить,монтаж производить после согласования с заказчиком и дизайнером.
7. Уровень полов санузла довести до уровня чистового пола во всех помещениях.
8. Точное местоположение плинтуса возле конвекторов уточнить у дизайнера только после подбора подходящих моделей конвекторов и согласования заказчика.

		Подпись	Дата		Стадия	Лист
					ДП	18
Дизайнер:						
Выполнил:				План раскладки напольных покрытий		
Заказчик:						


Развертка стен прихожей

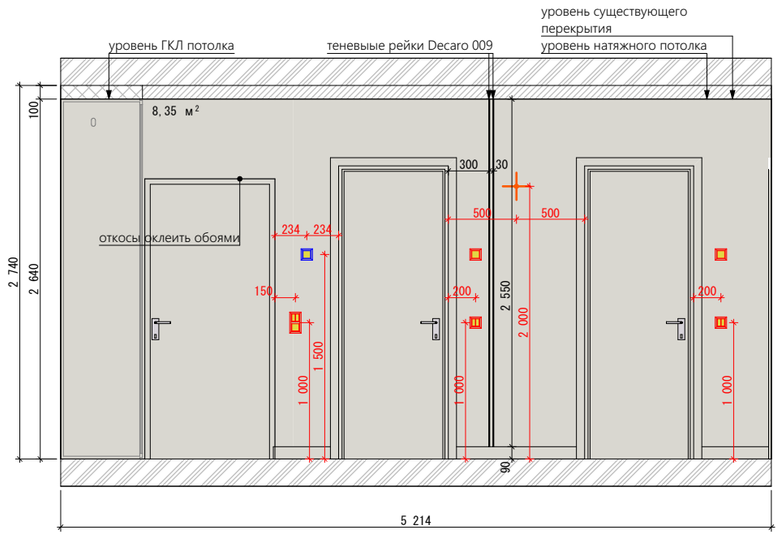

Прихожая 01 1:45

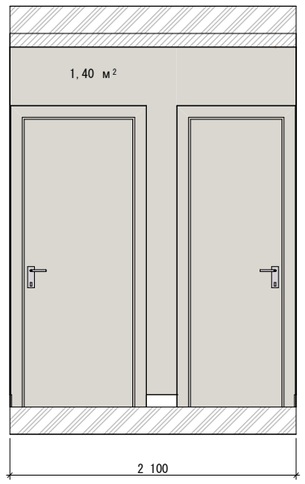

Прихожая 02 1:45

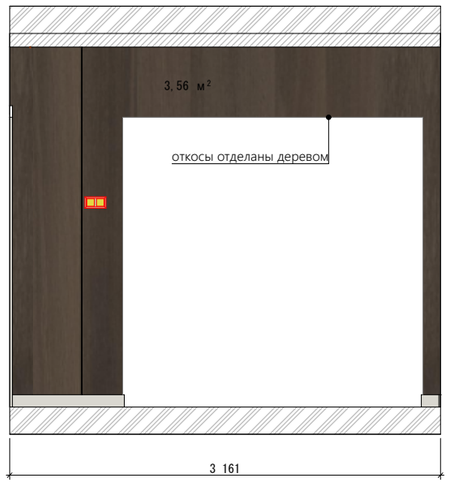


Прихожая 03 1:45




04 Прихожая 1:45

монтажж электрического и распред.щитков - точное местоположение и размеры опр.по месту, согласовать с заказчицей

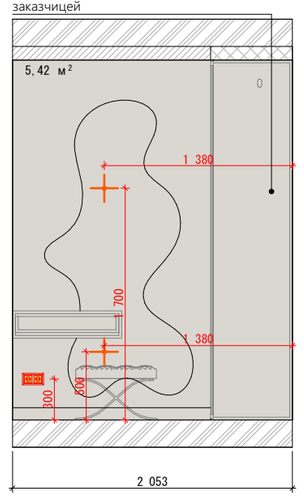

Прихожая 05 1:45

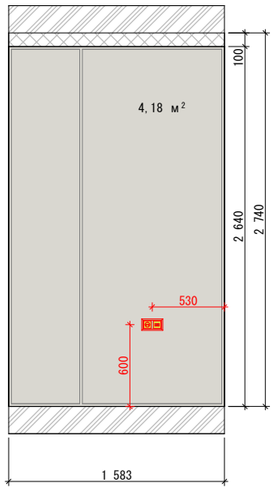

Прихожая 06 1:45

УСЛОВНЫЕ ОБОЗНАЧЕНИЯ:


	Обои Marburg 36211 S=19.35м² без запаса
	МДФ панели S=4,8м² без запаса

ПРИМЕЧАНИЯ:


1. Все размеры указаны в миллиметрах.
2. Размеры даны без учета отделочных слоев.
3. Все площади даны без запаса.
4. Привязки плинтуса см. на плане раскладки напольных покрытий, лист №17.
5. Привязка электрики возле двери дана от дверного проема, а не от полотна!
6. Лист смотреть совместно с 3D-визуализациями.

		Подпись	Дата		Стадия	Лист
					ДП	19
Дизайнер:						
Выполнил:				Развертка стен прихожей		
Заказчик:						


Развертка стен кухни-гостиной

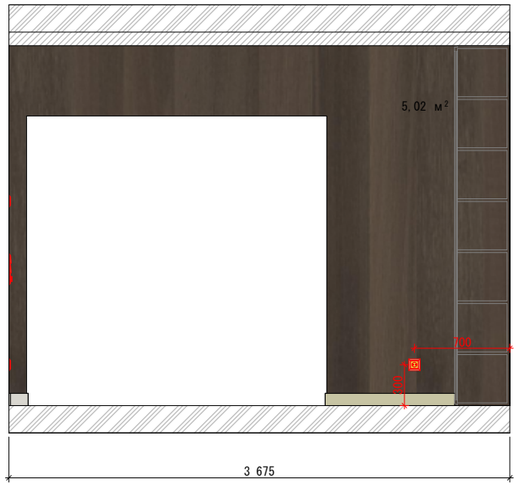

Кух-гост 01 1:45

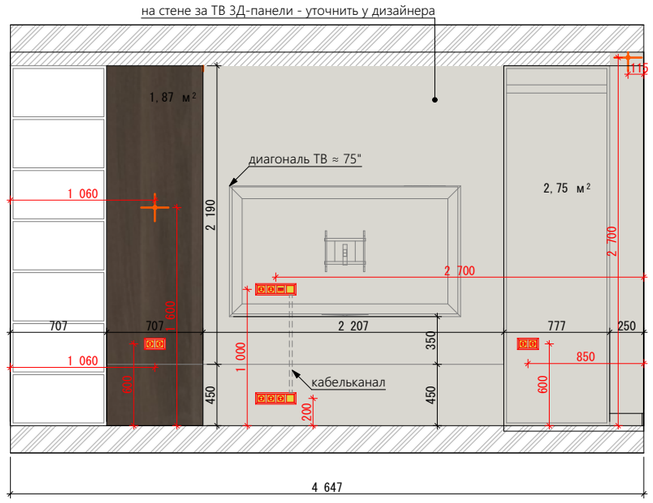

Кух-гост 02 1:45

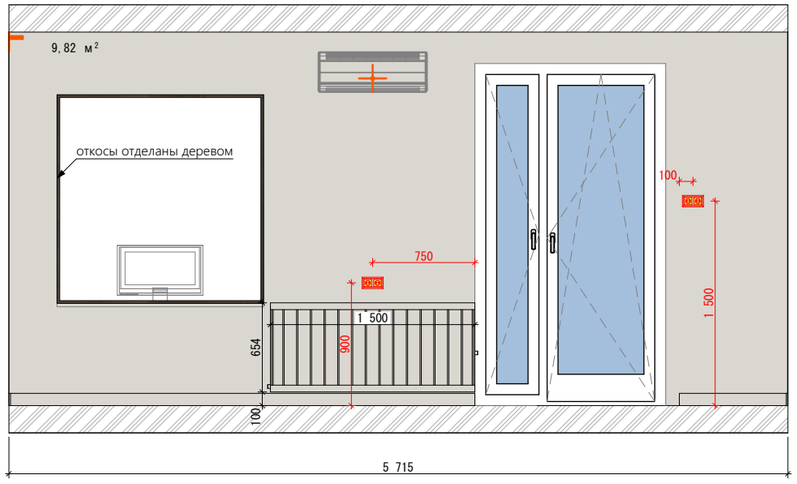

Кух-гост 03 1:45

Кух-гост 04 1:45

Кух-гост 05 1:45
Кух-гост 06 1:45
Кух-гост 07 1:45
Кух-гост 08 1:45
Кух-гост 09 1:45
Кух-гост 10 1:45
Кух-гост 11 1:45
Кух-гост 12 1:45

ПРИМЕЧАНИЯ:


1. Все размеры указаны в миллиметрах.
2. Размеры даны без учета отделочных слоев.
3. Углы плитки запиливать под 45 градусов.
4. Шов минимальный (ректифицированный керамогранит).
5. Каждый вид керамогранита затирается своим цветом затирки - уточнить у дизайнера.
6. Привязка сантехнического оборудования указана на развертках.
7. Установка сантехнического оборудования согласно тех. картам, см. лист 10.
8. Привязка электрики возле двери дана от дверного проема, а не от полотна!
9. Привязки плинтуса см. на плане раскладки напольных покрытий, лист №17.
10. Лист смотреть совместно с 3D-визуализациями.

УСЛОВНЫЕ ОБОЗНАЧЕНИЯ:


	Обои Marburg 36211 S=32,5м² без запаса
	МДФ панели S=6,7м² без запаса

		Подпись	Дата		Стадия	Лист
					ДП	20
Дизайнер:						
Выполнил:				Развертка стен кухни-гостиной		
Заказчик:						


Развертка стен детской

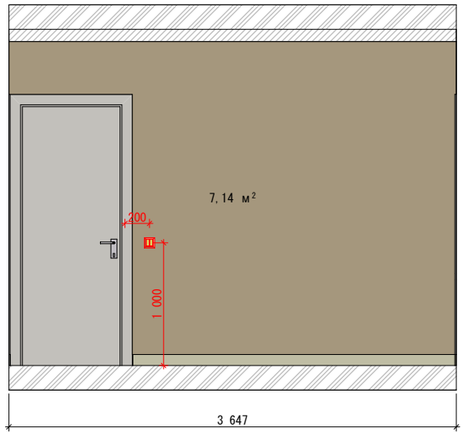


Детская 01 1:50

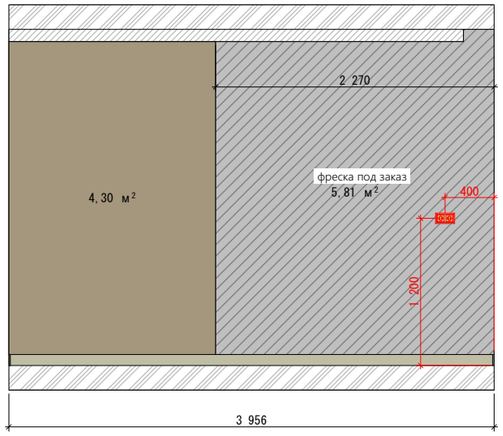


Детская 02 1:50

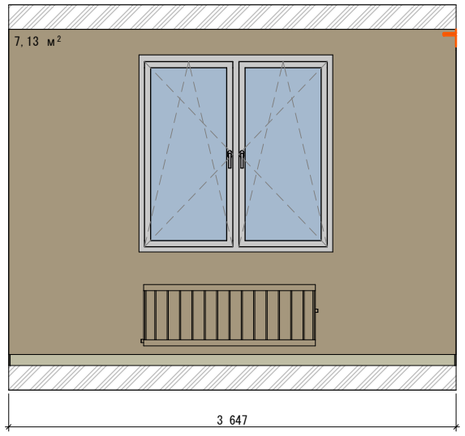

Детская 03 1:50

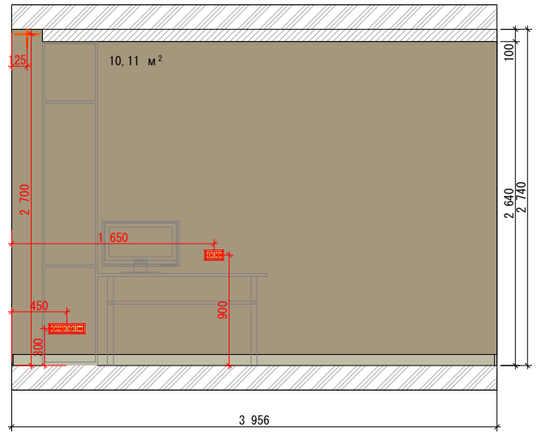

Детская 04 1:50

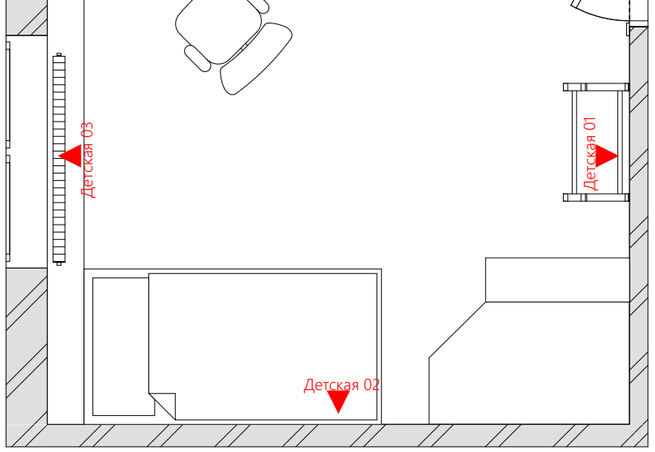

УСЛОВНЫЕ ОБОЗНАЧЕНИЯ:


	Обои Marburg 34215 S=28,7м² без запаса
	Фреска под заказ S=5,81м² без запаса

ПРИМЕЧАНИЯ:


1. Все размеры указаны в миллиметрах.
2. Размеры даны без учета отделочных слоев.
3. Все площади даны без запаса.
4. Привязки плинтуса см. на плане раскладки напольных покрытий, лист №18.
5. Привязка электрики возле двери дана от дверного проема, а не от полотна!
6. Лист смотреть совместно с 3D-визуализациями.

		Подпись	Дата		Стадия	Лист
					ДП	21
Дизайнер:						
Выполнил:				Развертка стен детской		
Заказчик:						


Развертка стен спальни

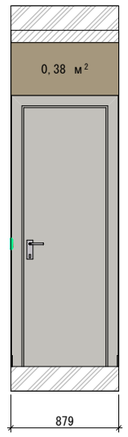


01
Спальня 1:50

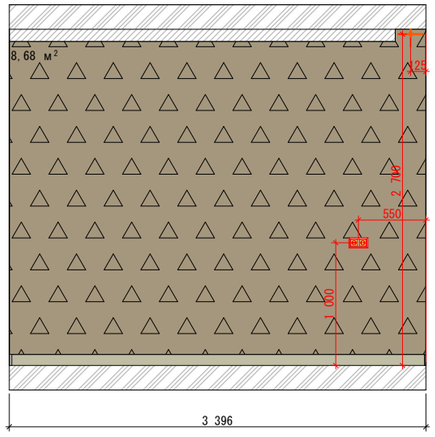


Спальня 02 1:50

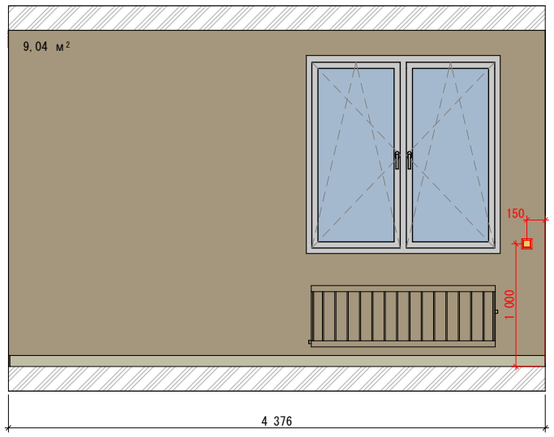


Спальня 03 1:50

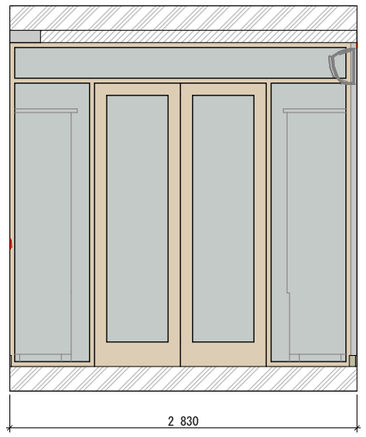


Спальня 04 1:50

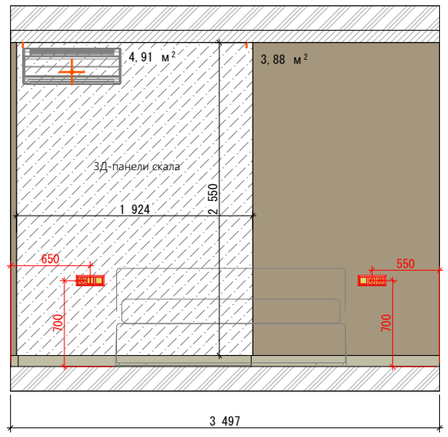

Спальня 05 1:50

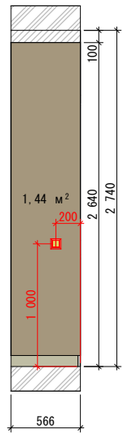

06
Спальня 1:50

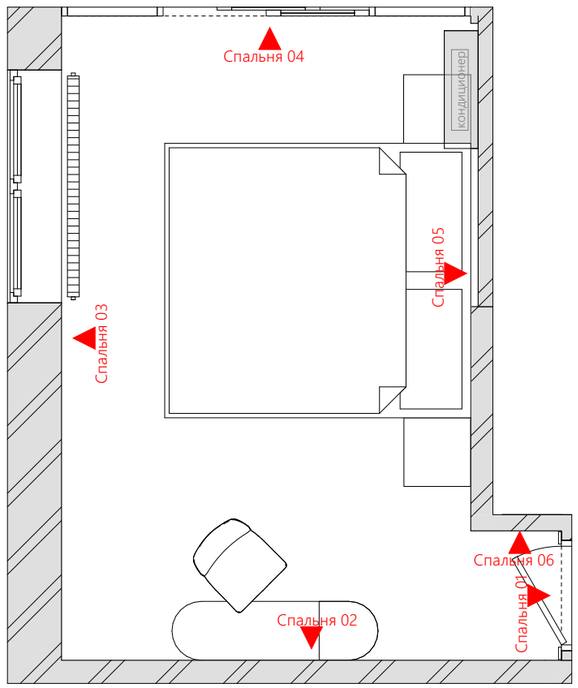

УСЛОВНЫЕ ОБОЗНАЧЕНИЯ:


	Обои Marburg 34215 S=14,9м² без запаса
	Обои Marburg 34202 S=8,7м² без запаса

ПРИМЕЧАНИЯ:

1. Все размеры указаны в миллиметрах.
2. Размеры даны без учета отделочных слоев.
3. Все площади даны без запаса.
4. Привязки плинтуса см. на плане раскладки напольных покрытий, лист №18.
5. Привязка электрики возле двери дана от дверного проема, а не от полотна!
6. Лист смотреть совместно с 3D-визуализациями.

		Подпись	Дата		Стадия	Лист
					ДП	22
Дизайнер:						
Выполнил:				Развертка стен спальни		
Заказчик:						

Развертка стен гардероба

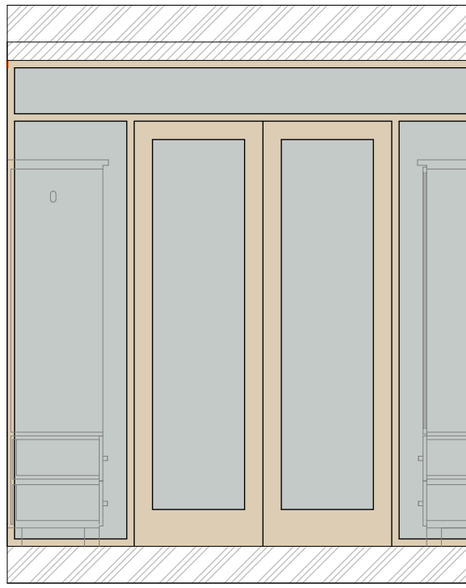


2 780

Гардероб 01 1:33,33




1 200

Гардероб 02 1:33,33

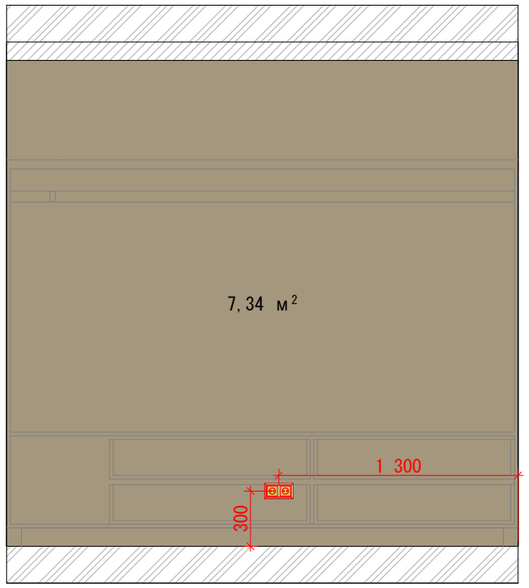


2 780

Гардероб 03 1:33,33

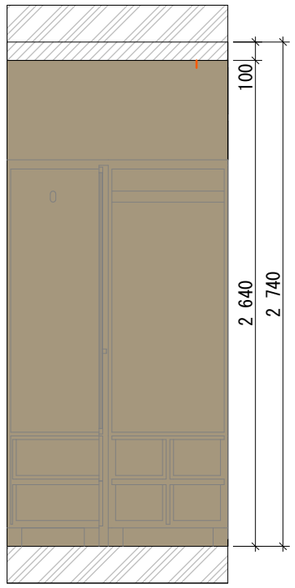

1 200

Гардероб 04 1:33,33

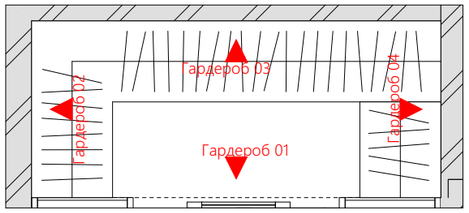

УСЛОВНЫЕ ОБОЗНАЧЕНИЯ:


	Обои Marburg 34215 S=14м² без запаса

ПРИМЕЧАНИЯ:


1. Все размеры указаны в миллиметрах.
2. Размеры даны без учета отделочных слоев.
3. Все площади даны без запаса.
4. Привязки плинтуса см. на плане раскладки напольных покрытий, лист №18.
5. Привязка электрики возле двери дана от дверного проема, а не от полотна!
6. Лист смотреть совместно с 3D-визуализациями.

		Подпись	Дата		Стадия	Лист
					ДП	23
Дизайнер:						
Выполнил:				Развертка стен гардероба		
Заказчик:						


Развертка стен балкона

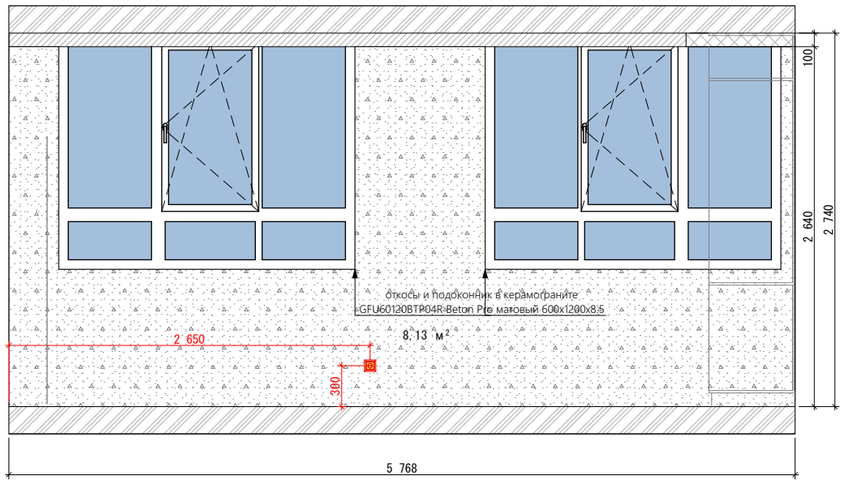


Балкон 01 1:45

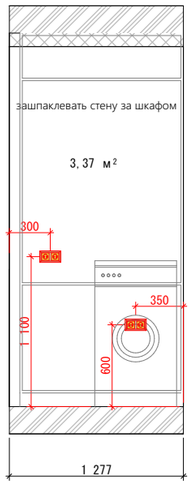


Балкон 02 1:45

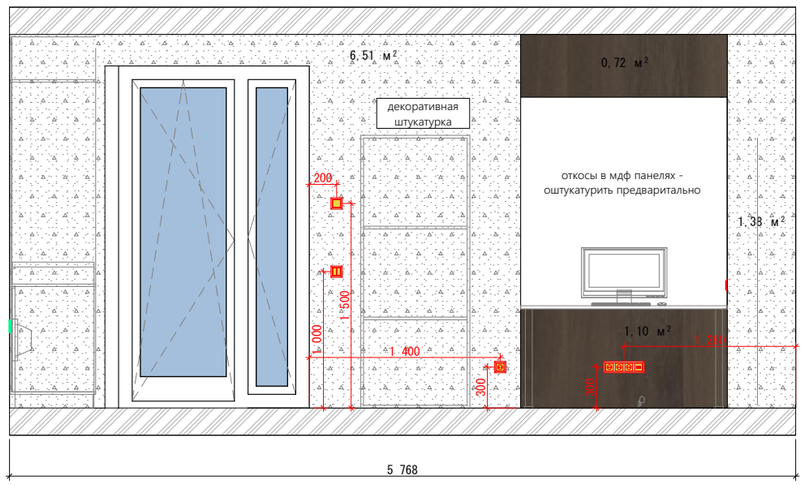

Балкон 03 1:45

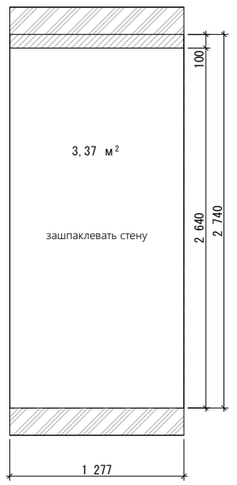

Балкон 04 1:45

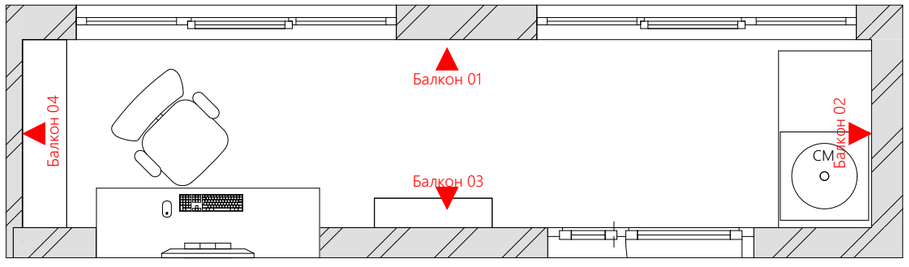

УСЛОВНЫЕ ОБОЗНАЧЕНИЯ:


	МДФ панели S=2м² без запаса
	Декоративная штукатурка S=16м² без запаса

ПРИМЕЧАНИЯ:

1. Все размеры указаны в миллиметрах.
2. Размеры даны без учета отделочных слоев.
3. Все площади даны без запаса.
4. Привязки плинтуса см. на плане раскладки напольных покрытий, лист №18.
5. Привязка электрики возле двери дана от дверного проема, а не от полотна!
6. Лист смотреть совместно с 3D-визуализациями.

		Подпись	Дата		Стадия	Лист
					ДП	24
Дизайнер:						
Выполнил:				Развертка стен балкона		
Заказчик:						

РАЗВЕРТКА ПО КУХОННОМУ ГАРНИТУРУ

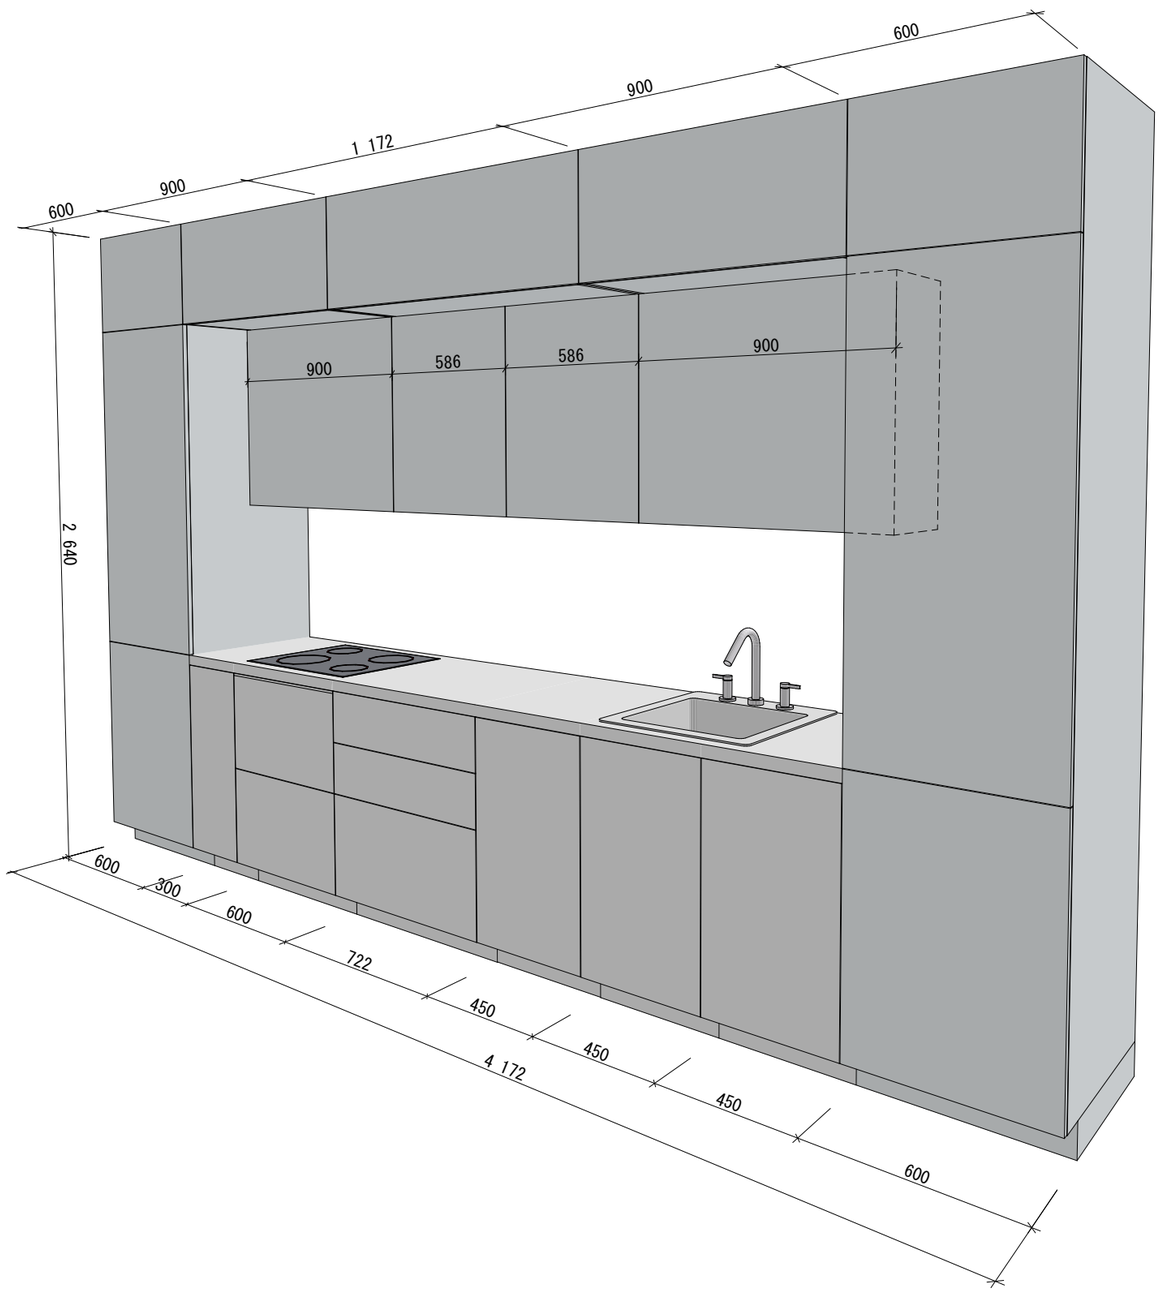

		Подпись	Дата		Стадия	Лист
					ДП	25
Дизайнер:						
Выполнил:				Развертка по кухонному гарнитуру		
Заказчик:						


























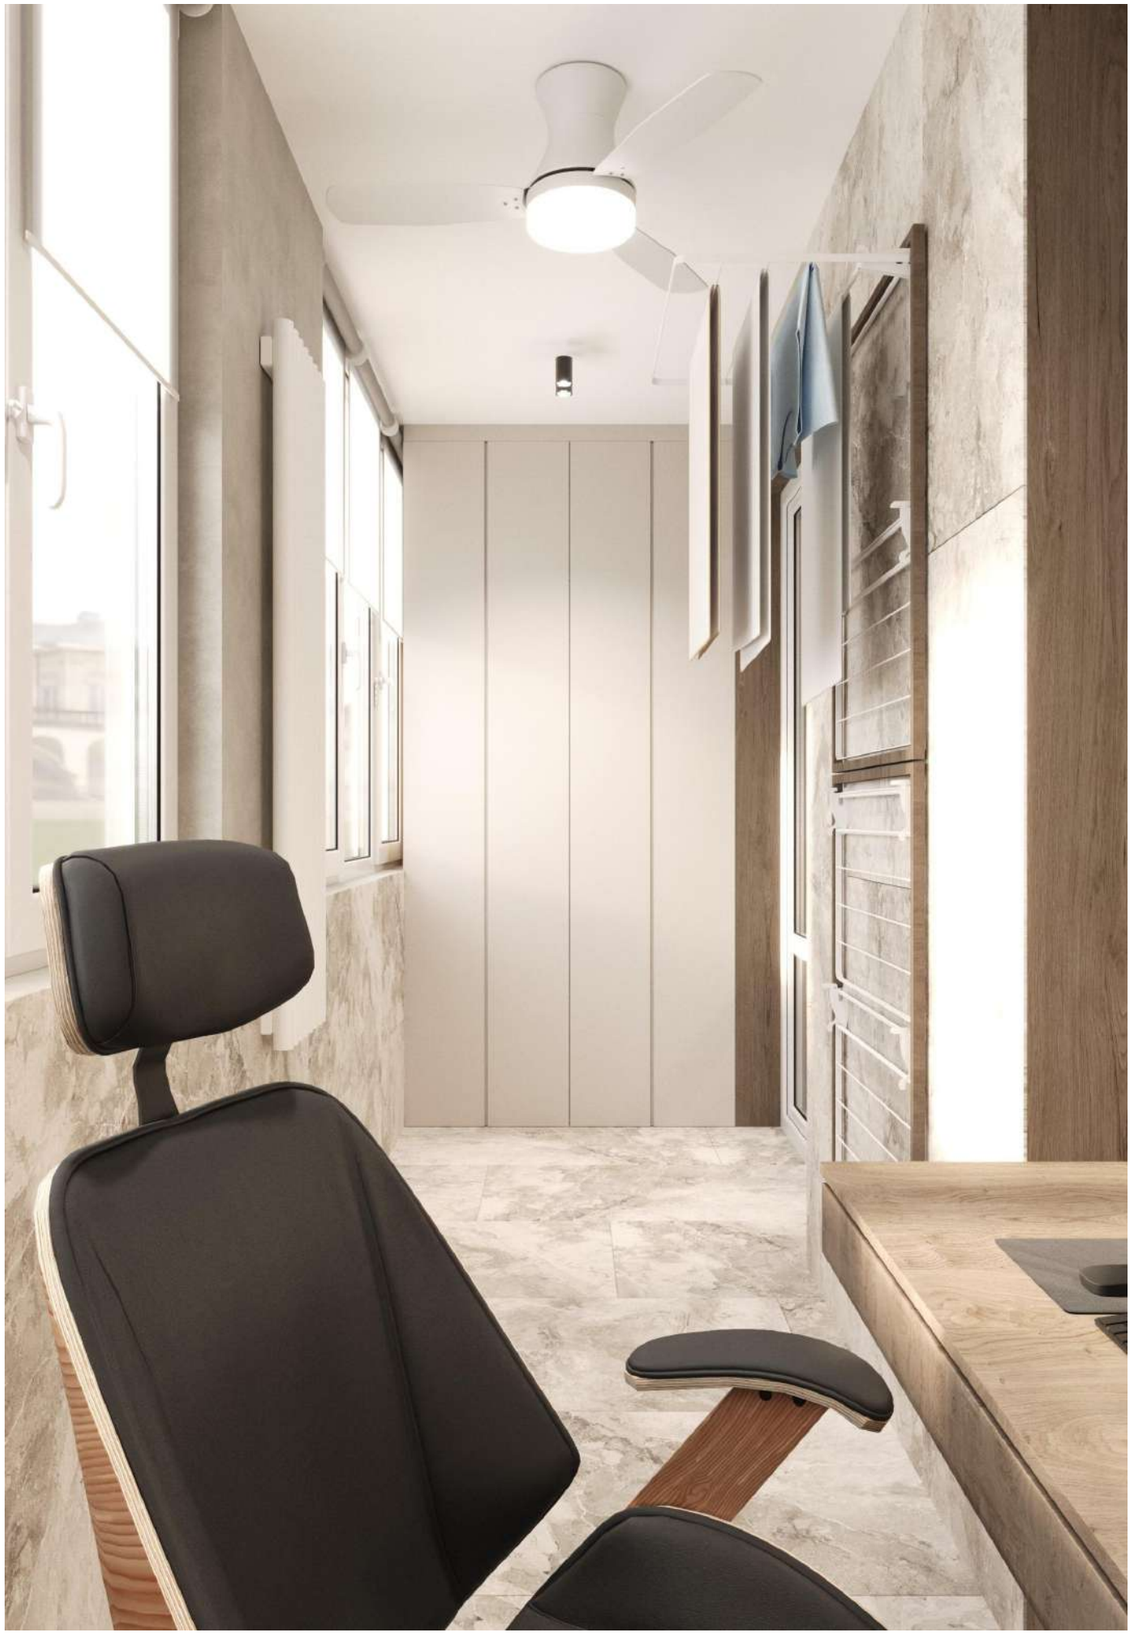

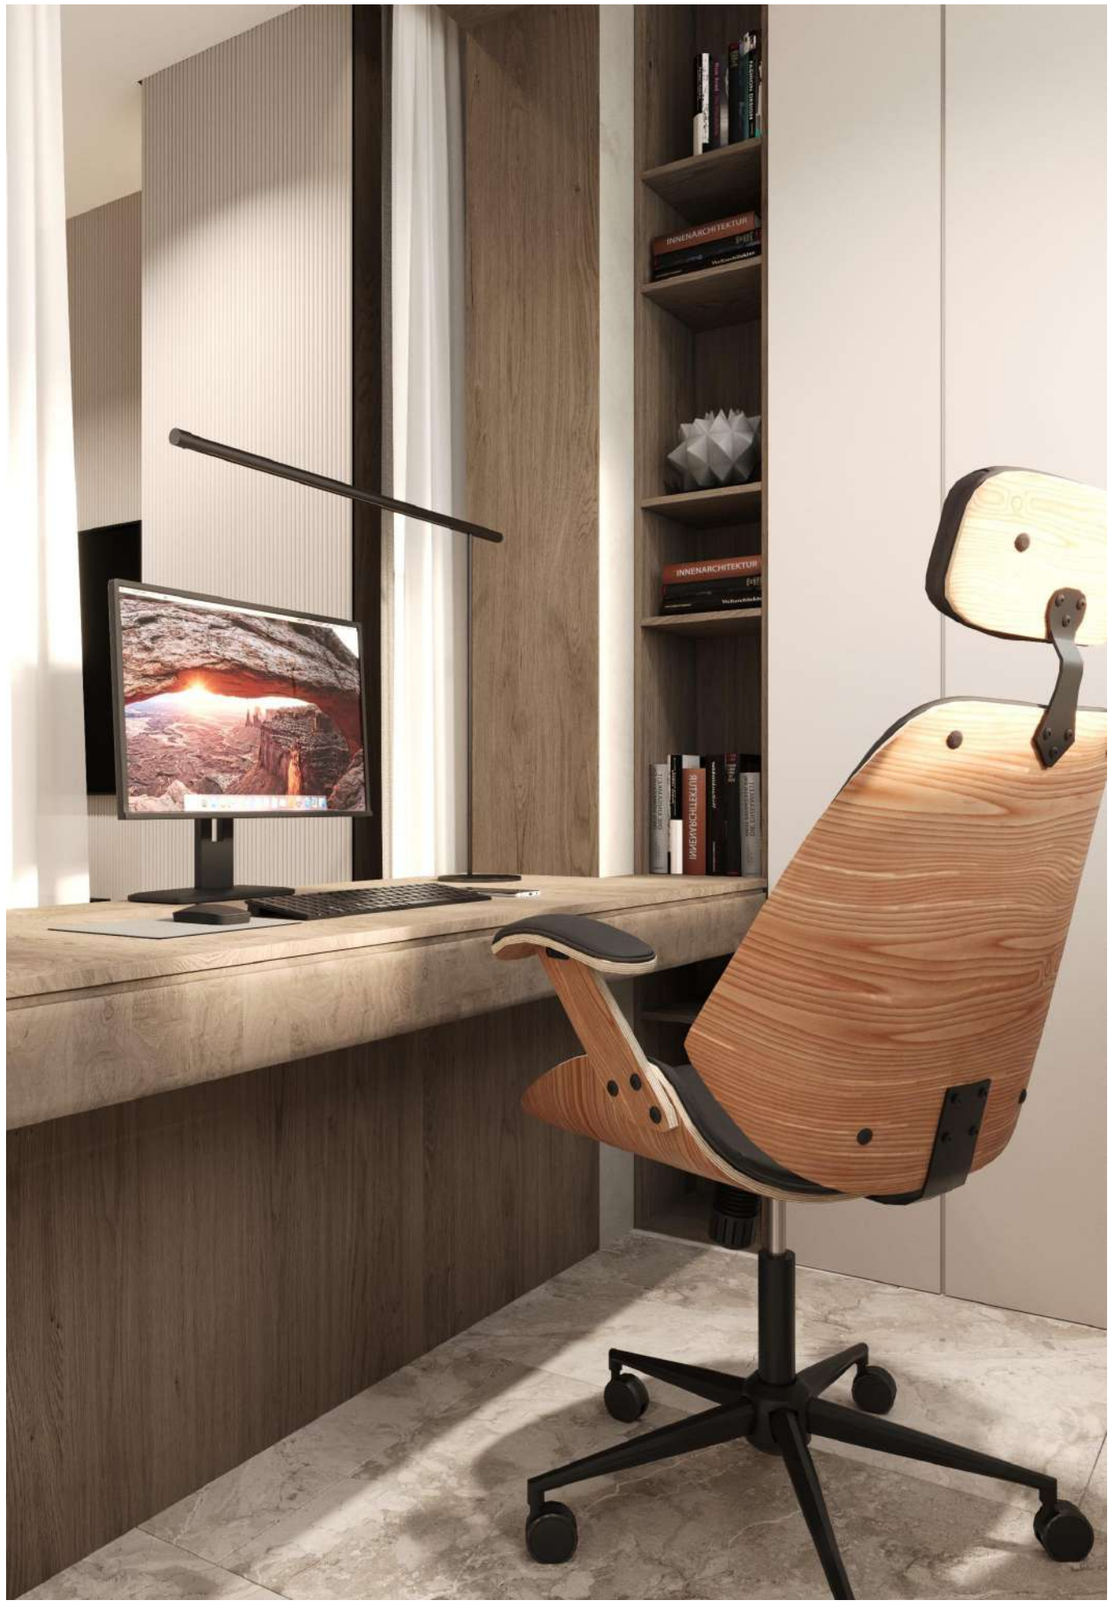
INNENARCHITEKTUR
INNENARCHITEKTUR

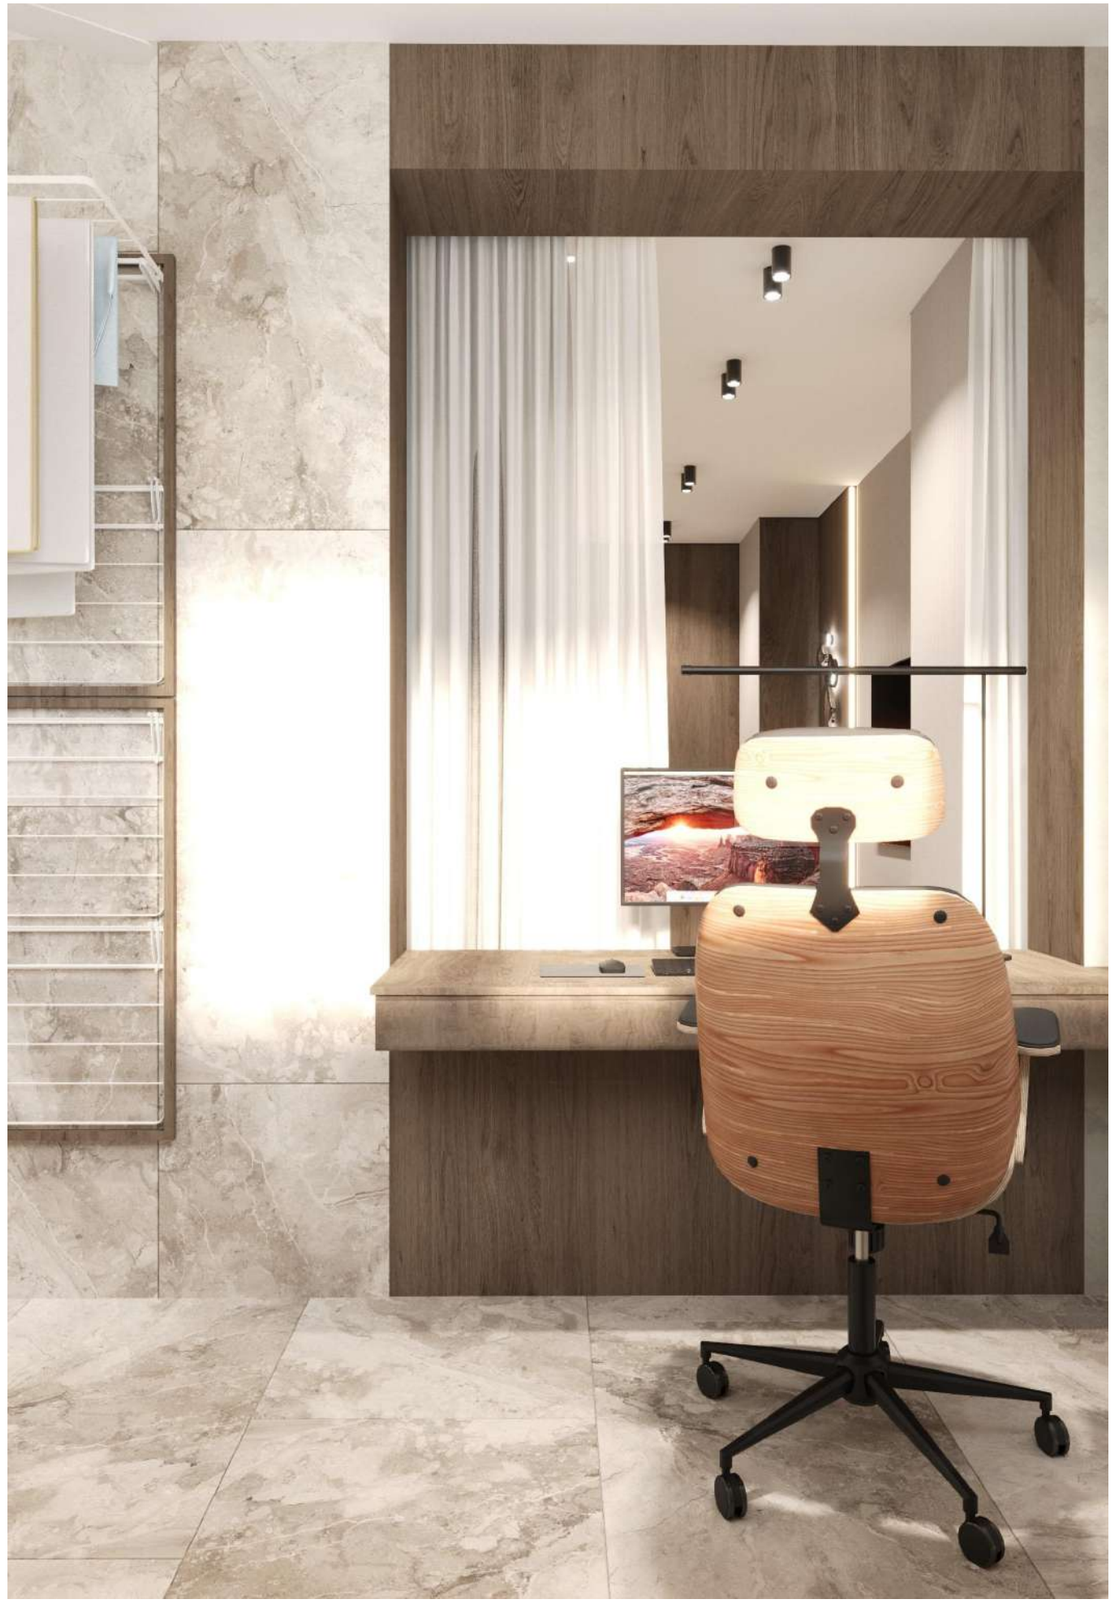










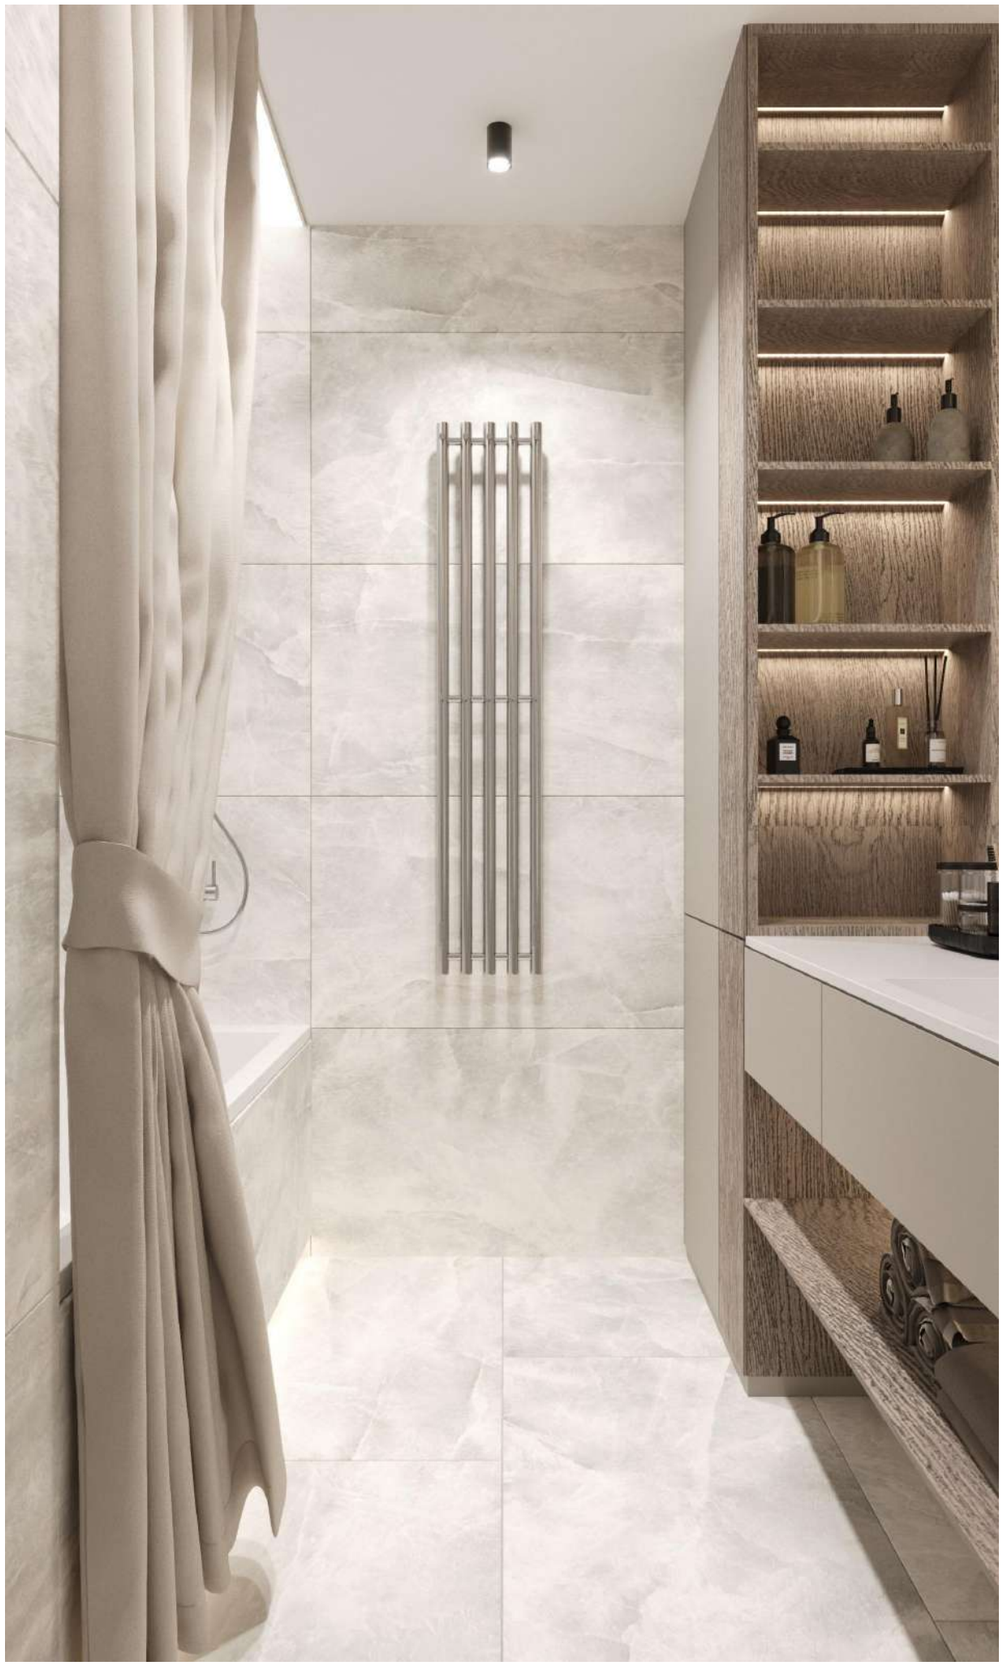




SAMSUNG






GIVENCHY
CHANEL
GIVENCHY

